


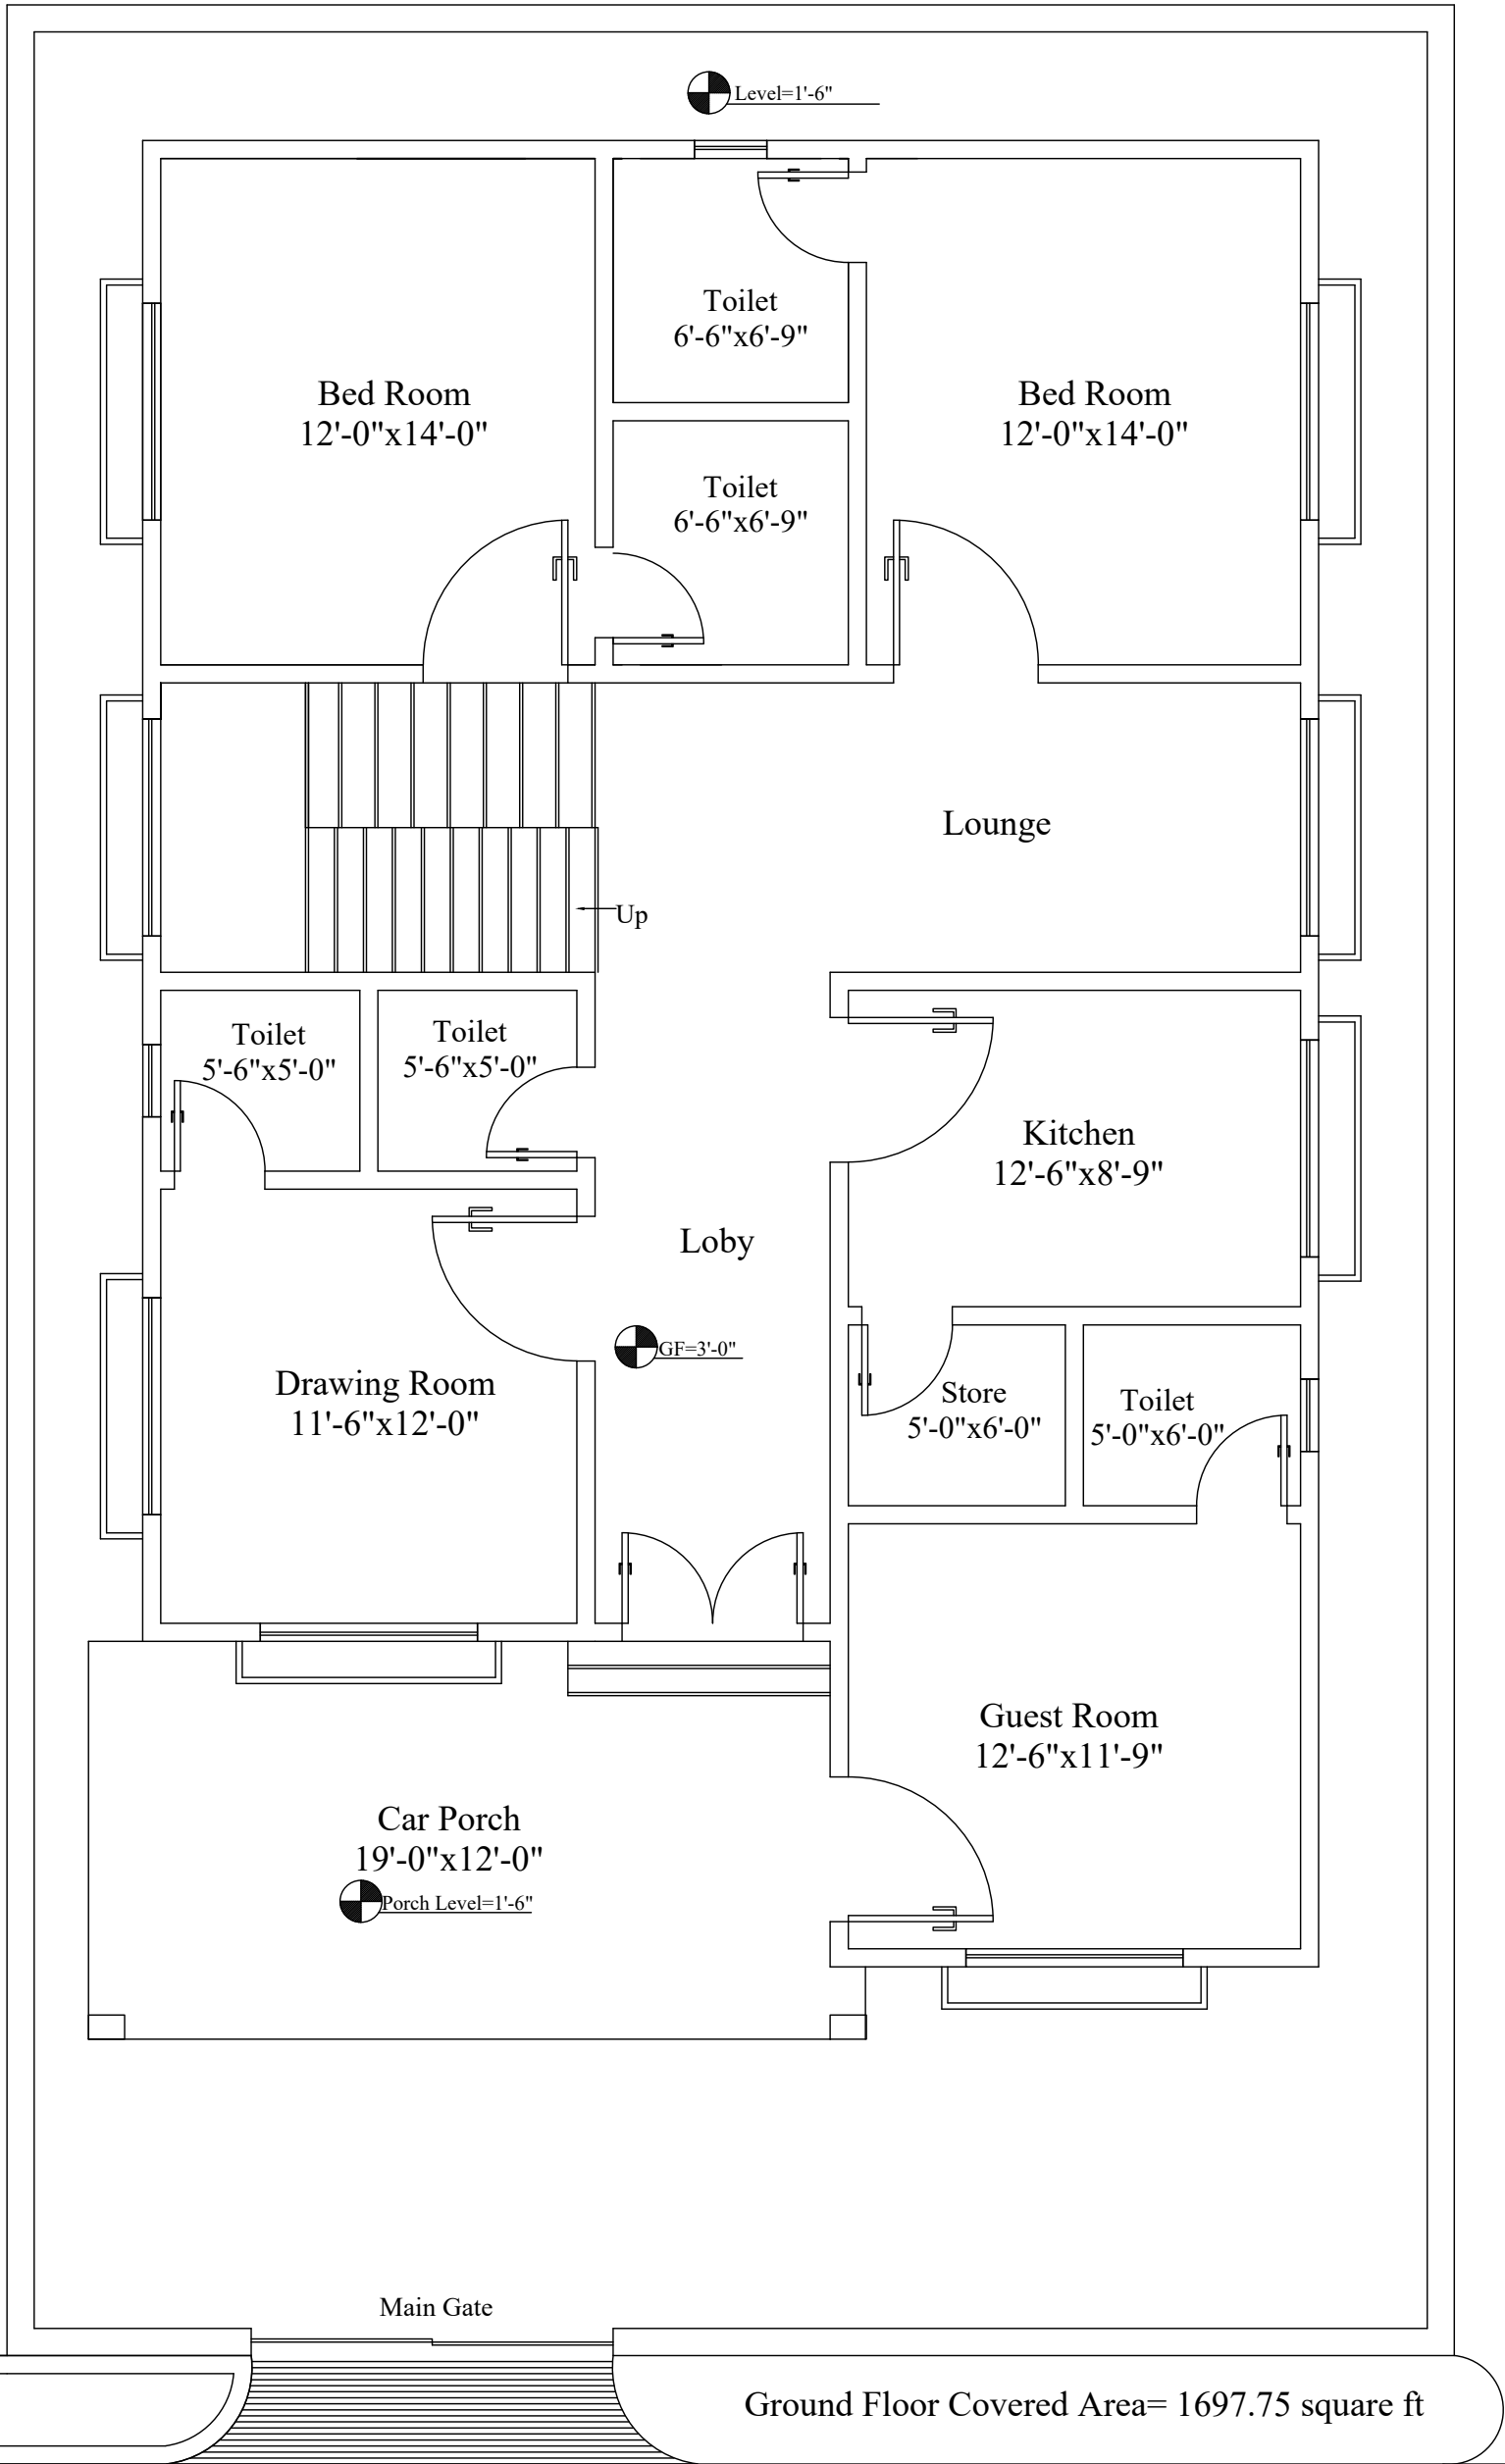


Design&Render By: Wajid Khan




Road Level=0'-0"

Project: Residential	Drawing:	Drawing Code:	Design By Wajid Khan: 0342-2421701
		S.No:	

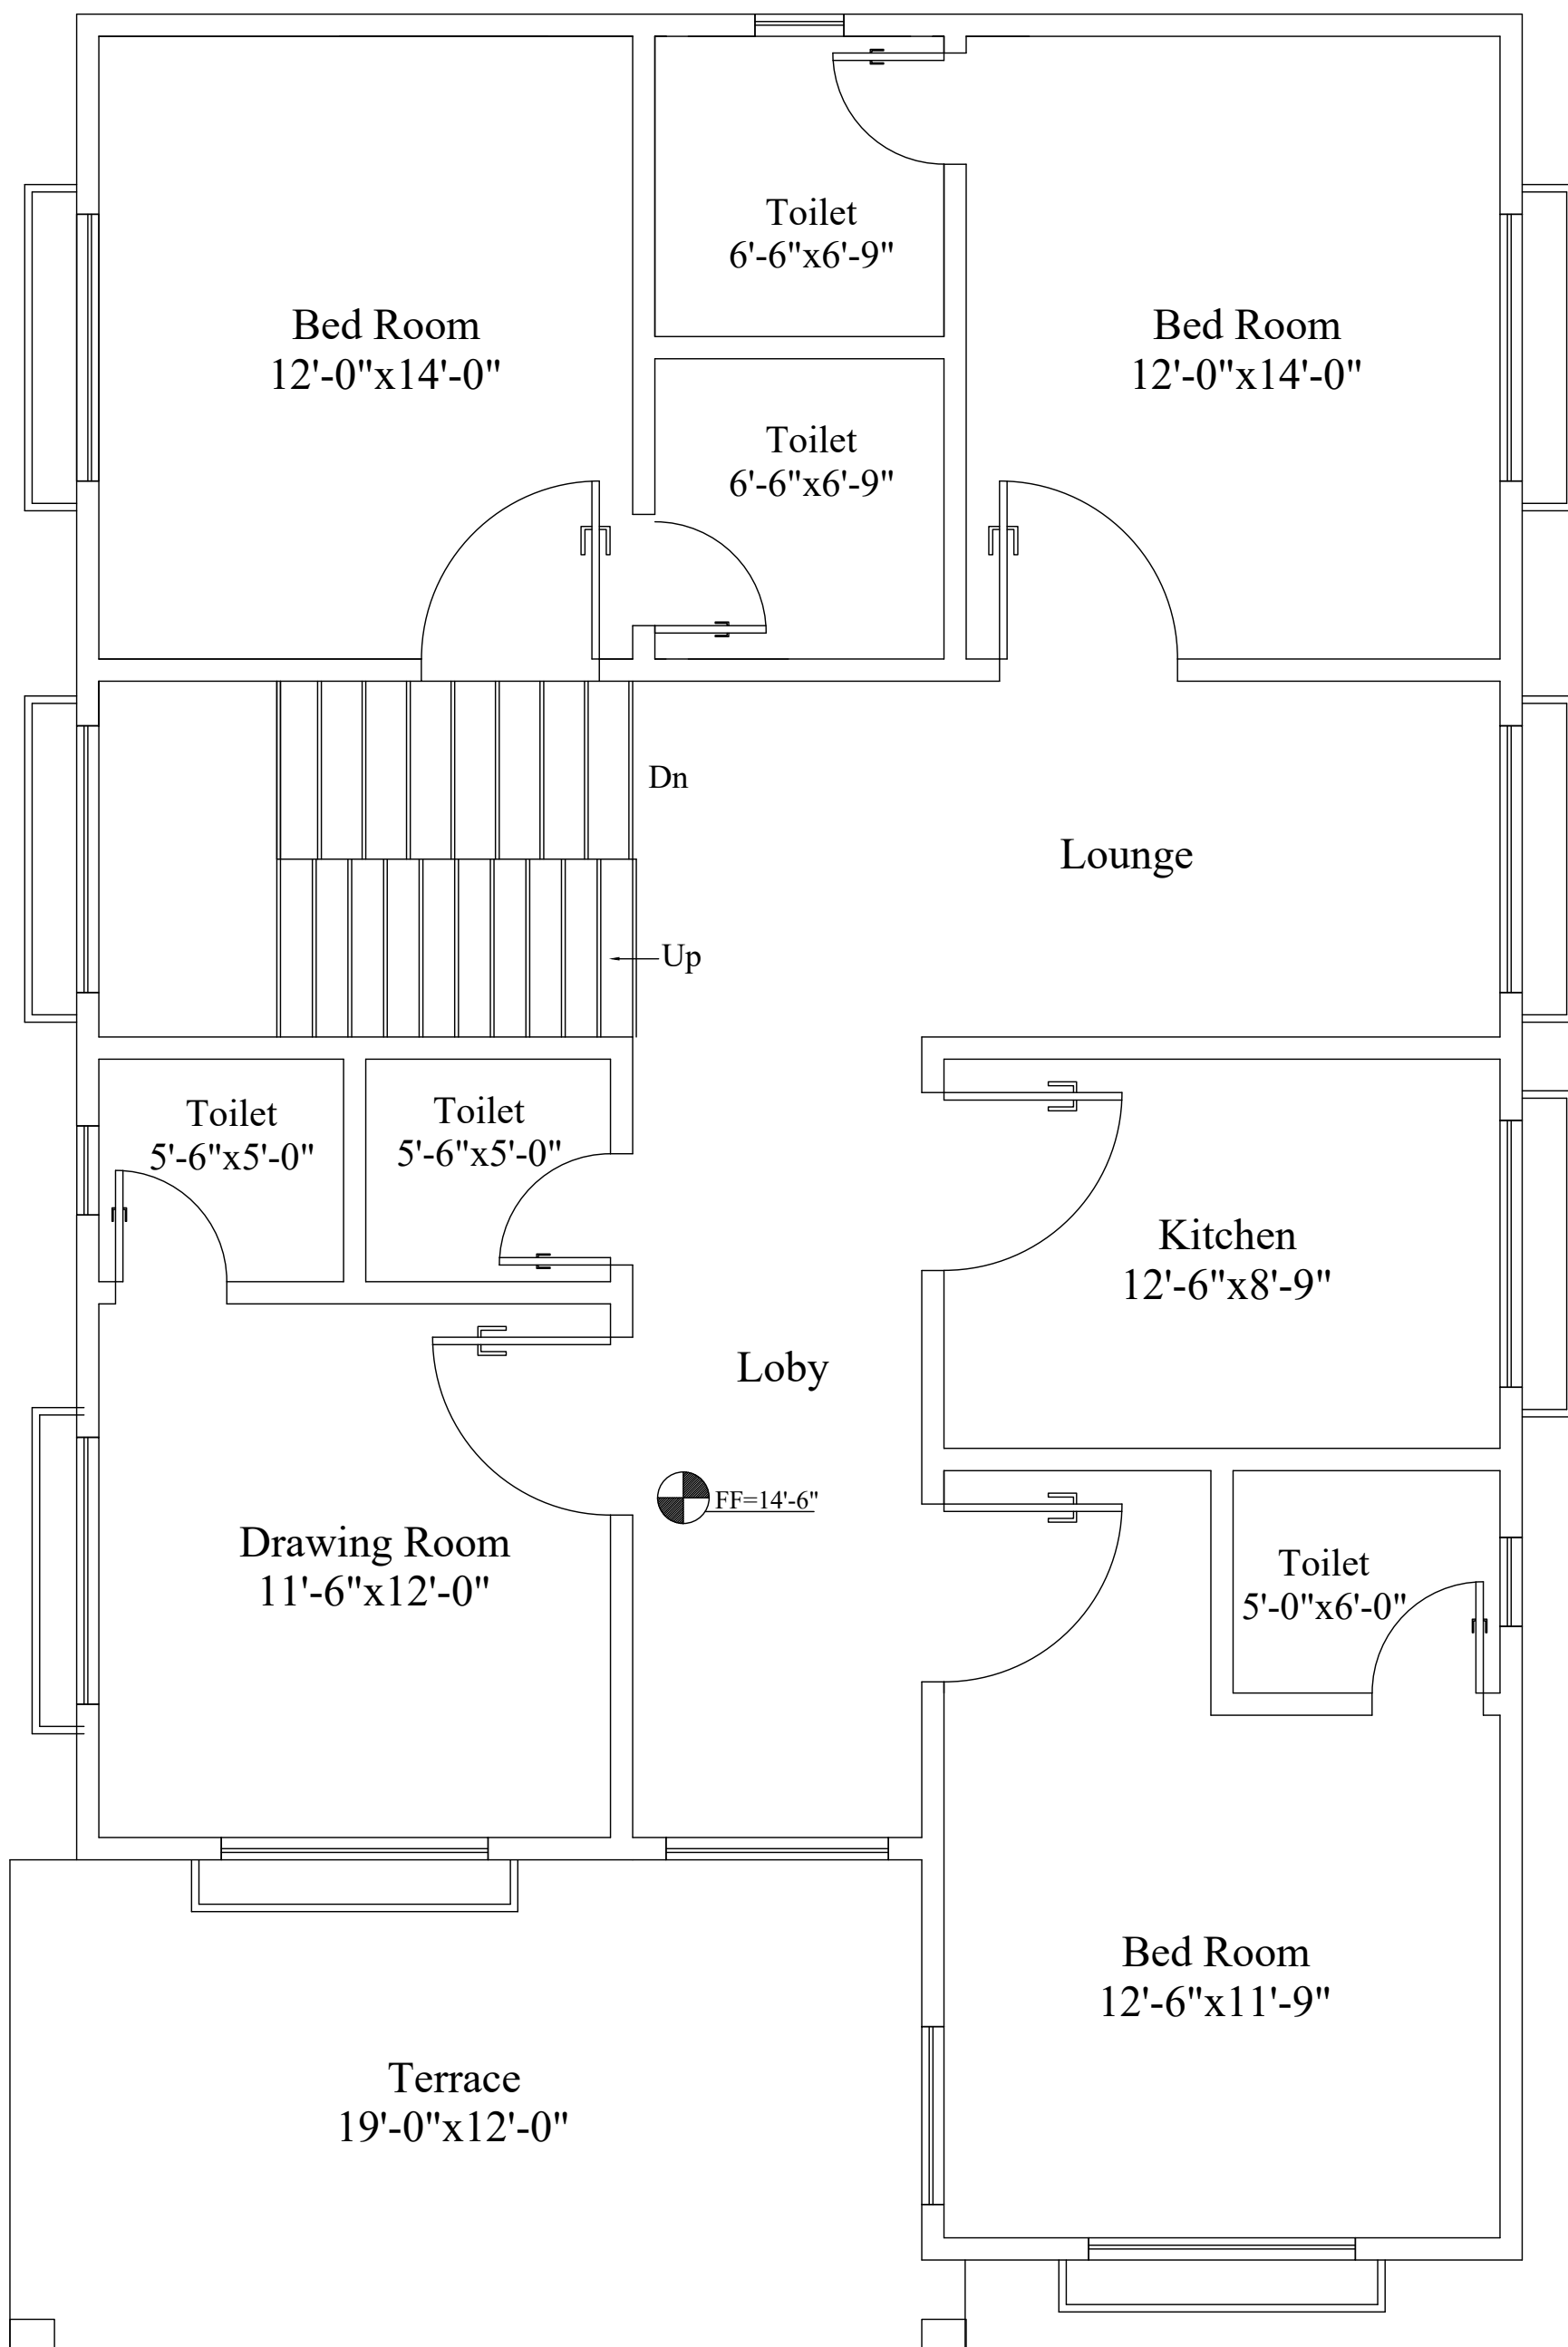


First Floor Covered Area= 1697.75 square ft

Project: Residential	Drawing:	Drawing Code:	Design By Wajid Khan: 0342-2421701
		S.No:	

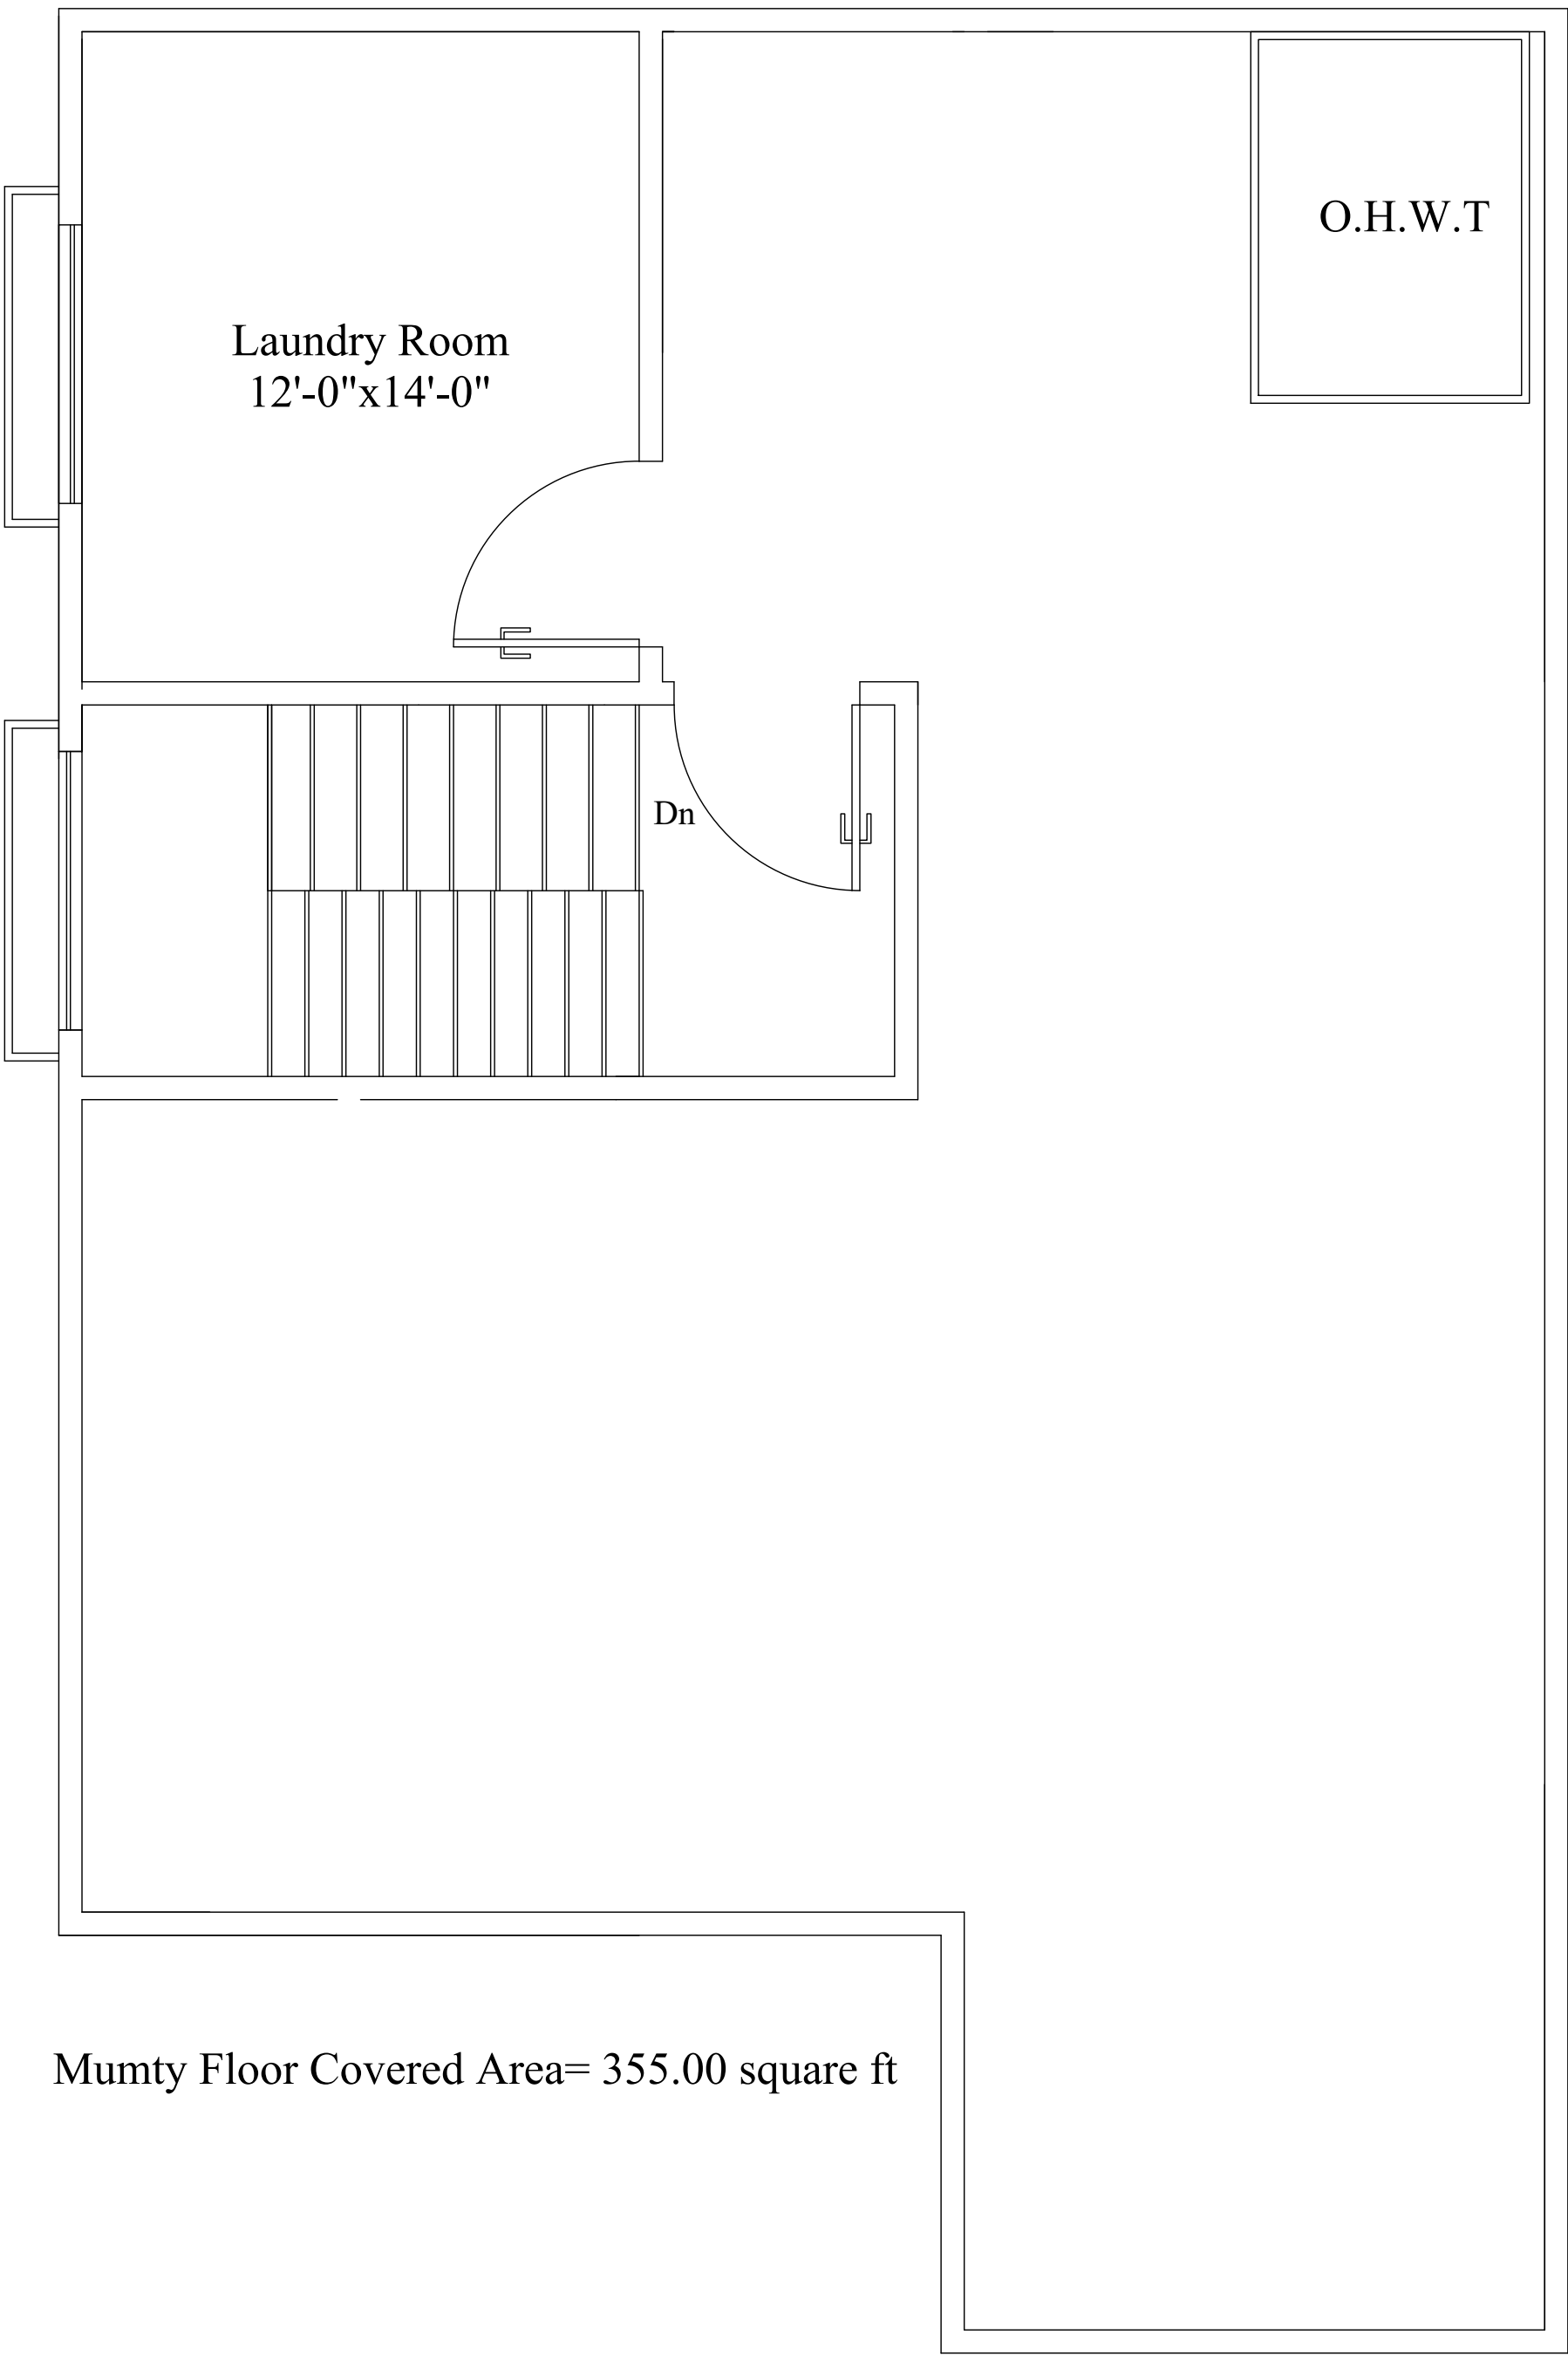


Mumty Floor Covered Area= 355.00 square ft


Project: Residential	Drawing:	Drawing Code:	Design By Wajid Khan: 0342-2421701
		S.No:	

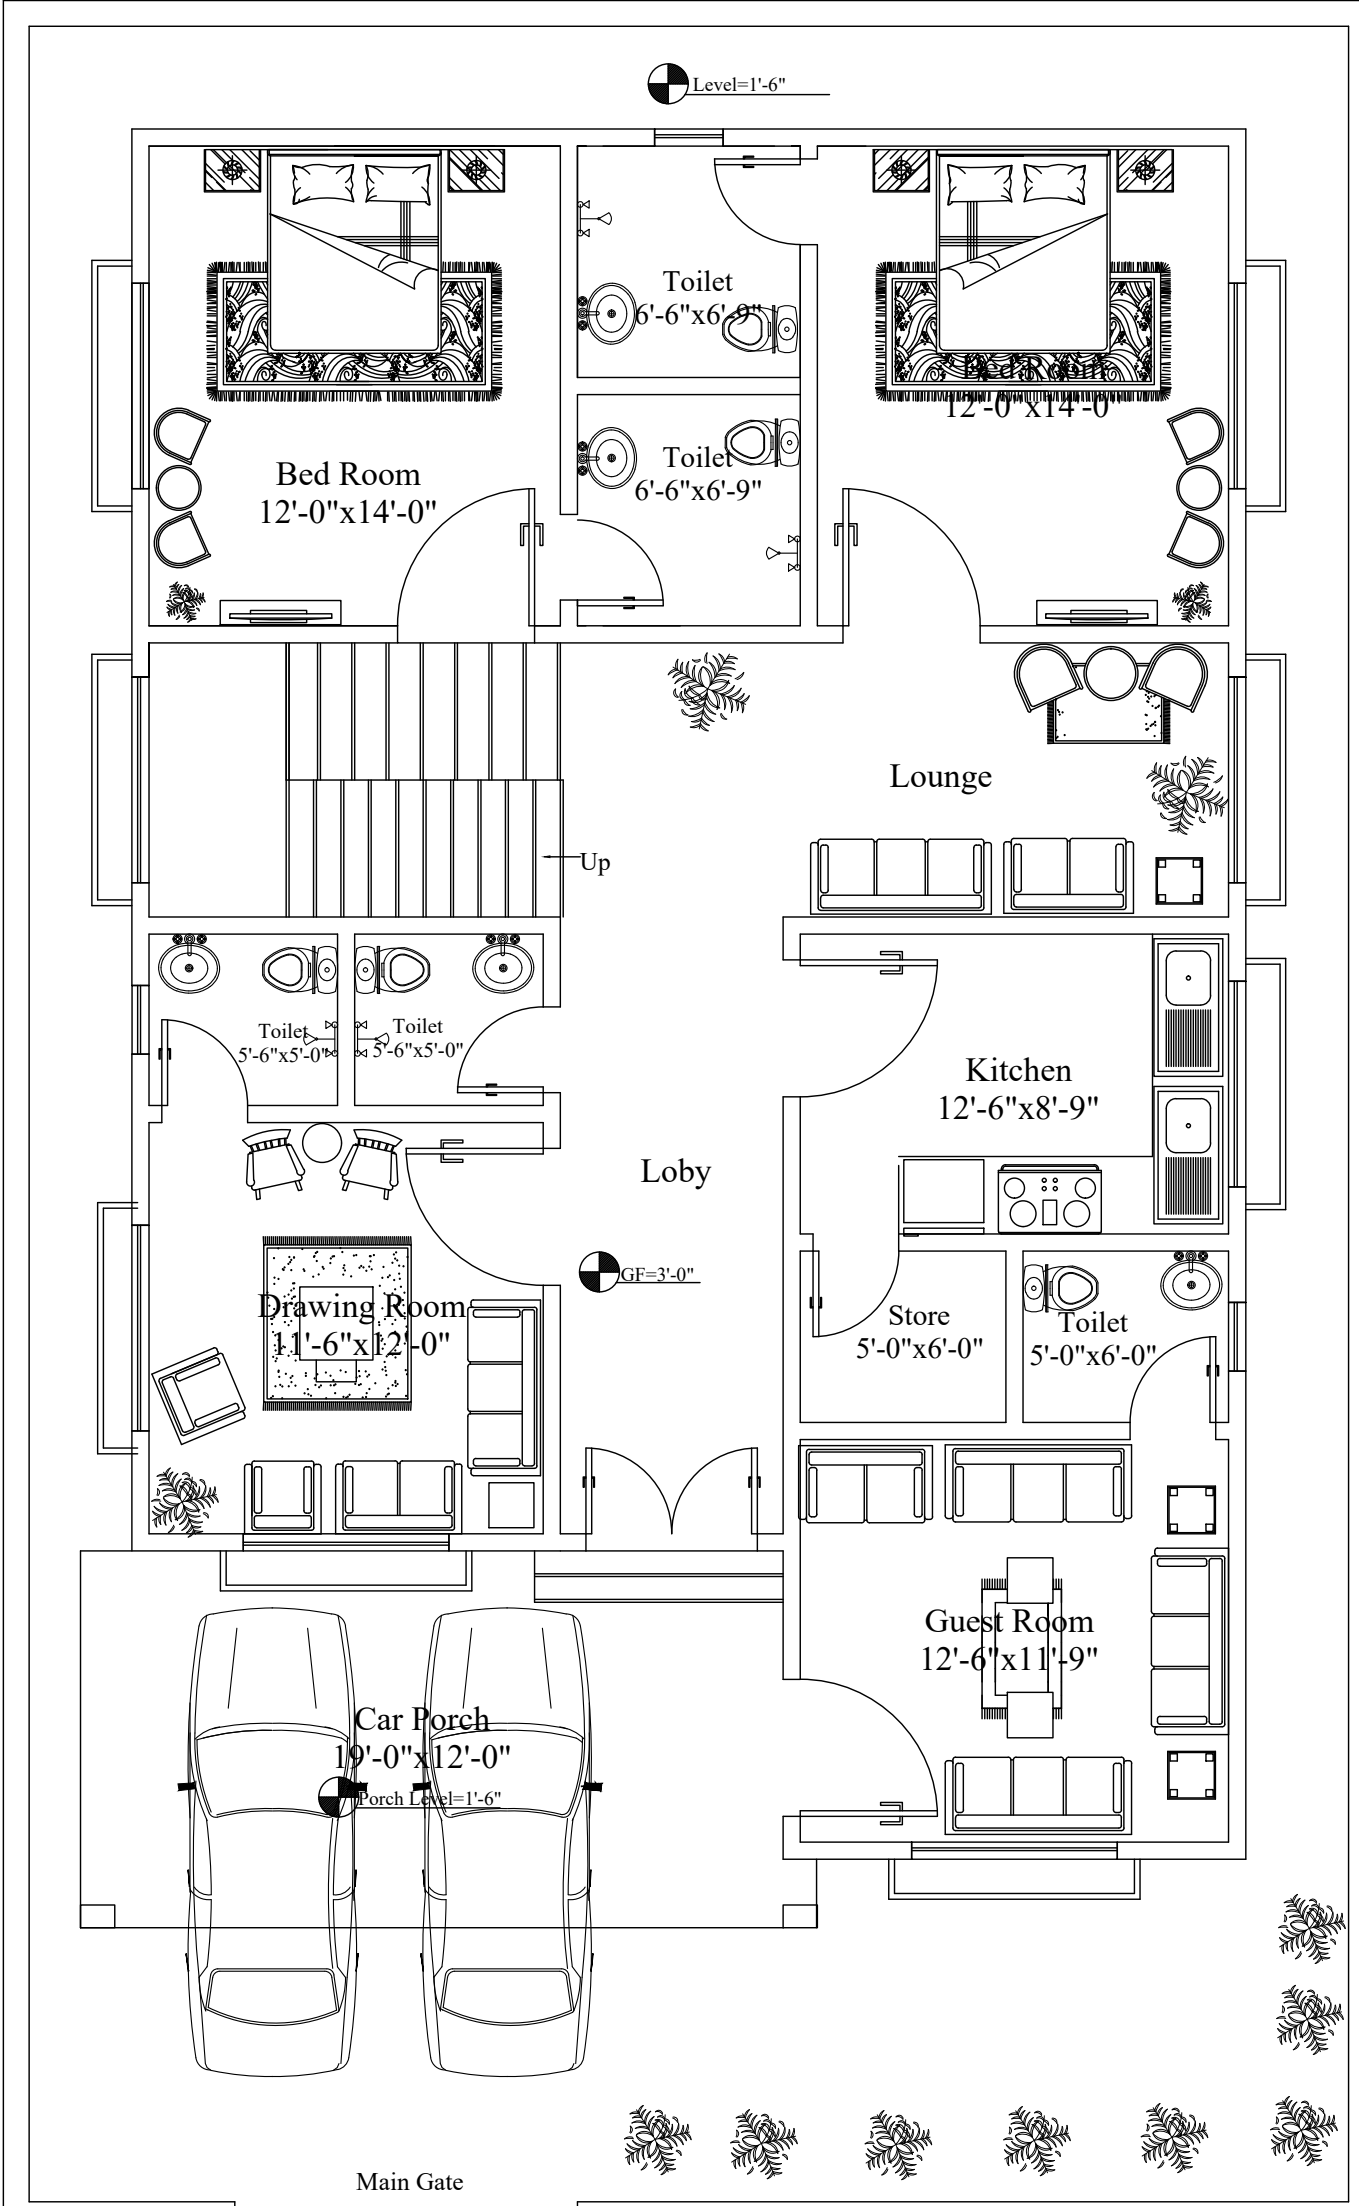

Ground Floor Covered Area= 1697.75 square ft

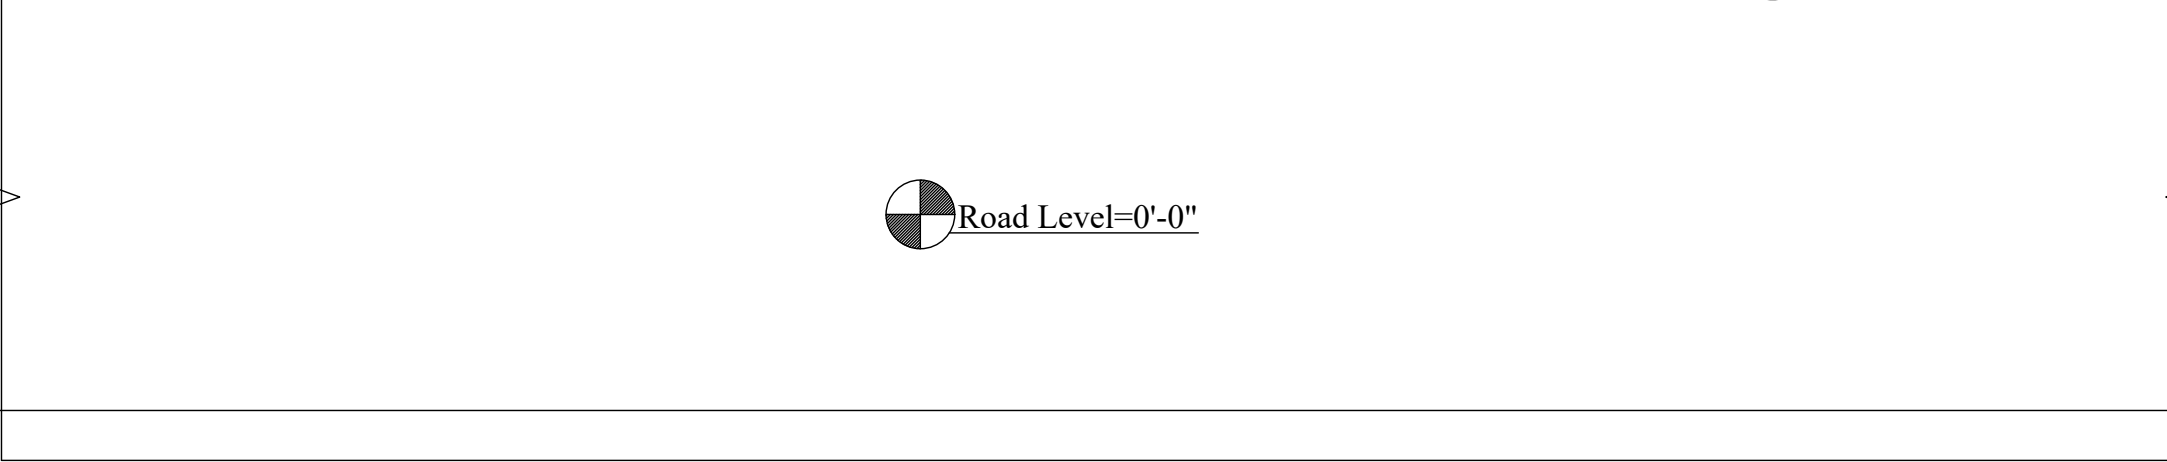

Project: Residential	Drawing:	Drawing Code:	Design By Wajid Khan: 0342-2421701
		S.No:	

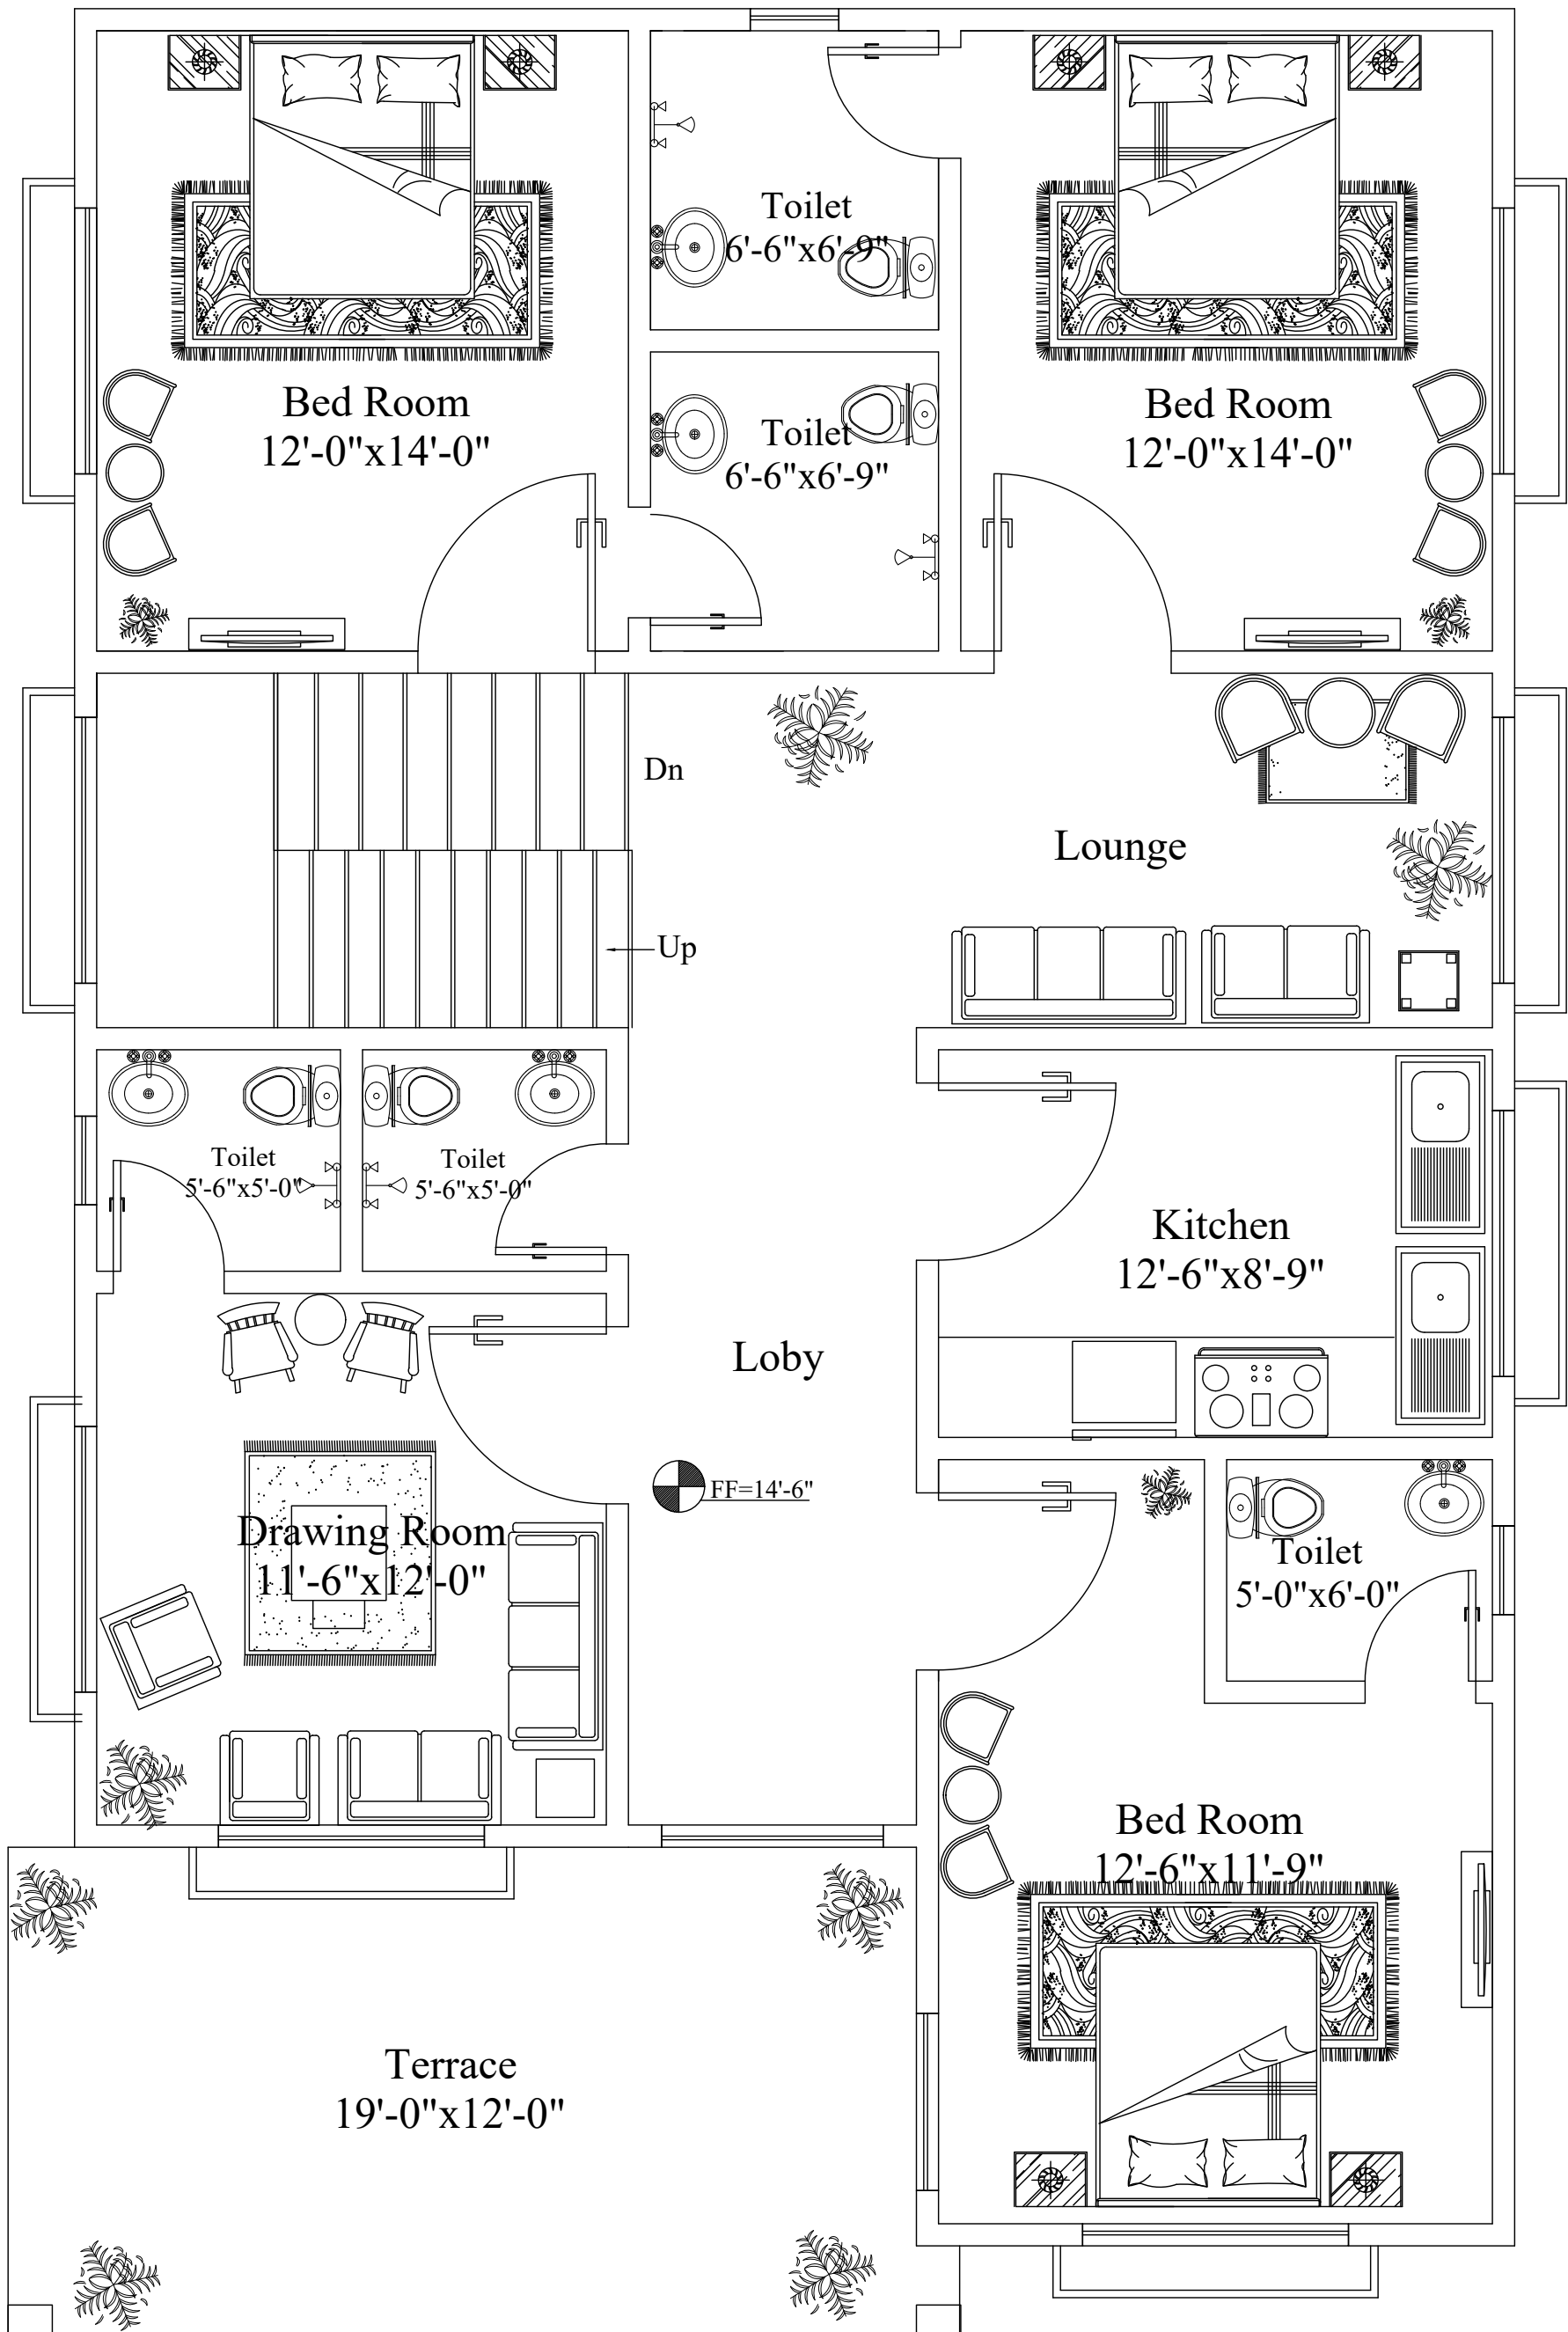

First Floor Covered Area= 1697.75 square ft


Project:
Residential

Drawing:

Drawing Code:


S.No:

Design By
Wajid Khan: 0342-2421701

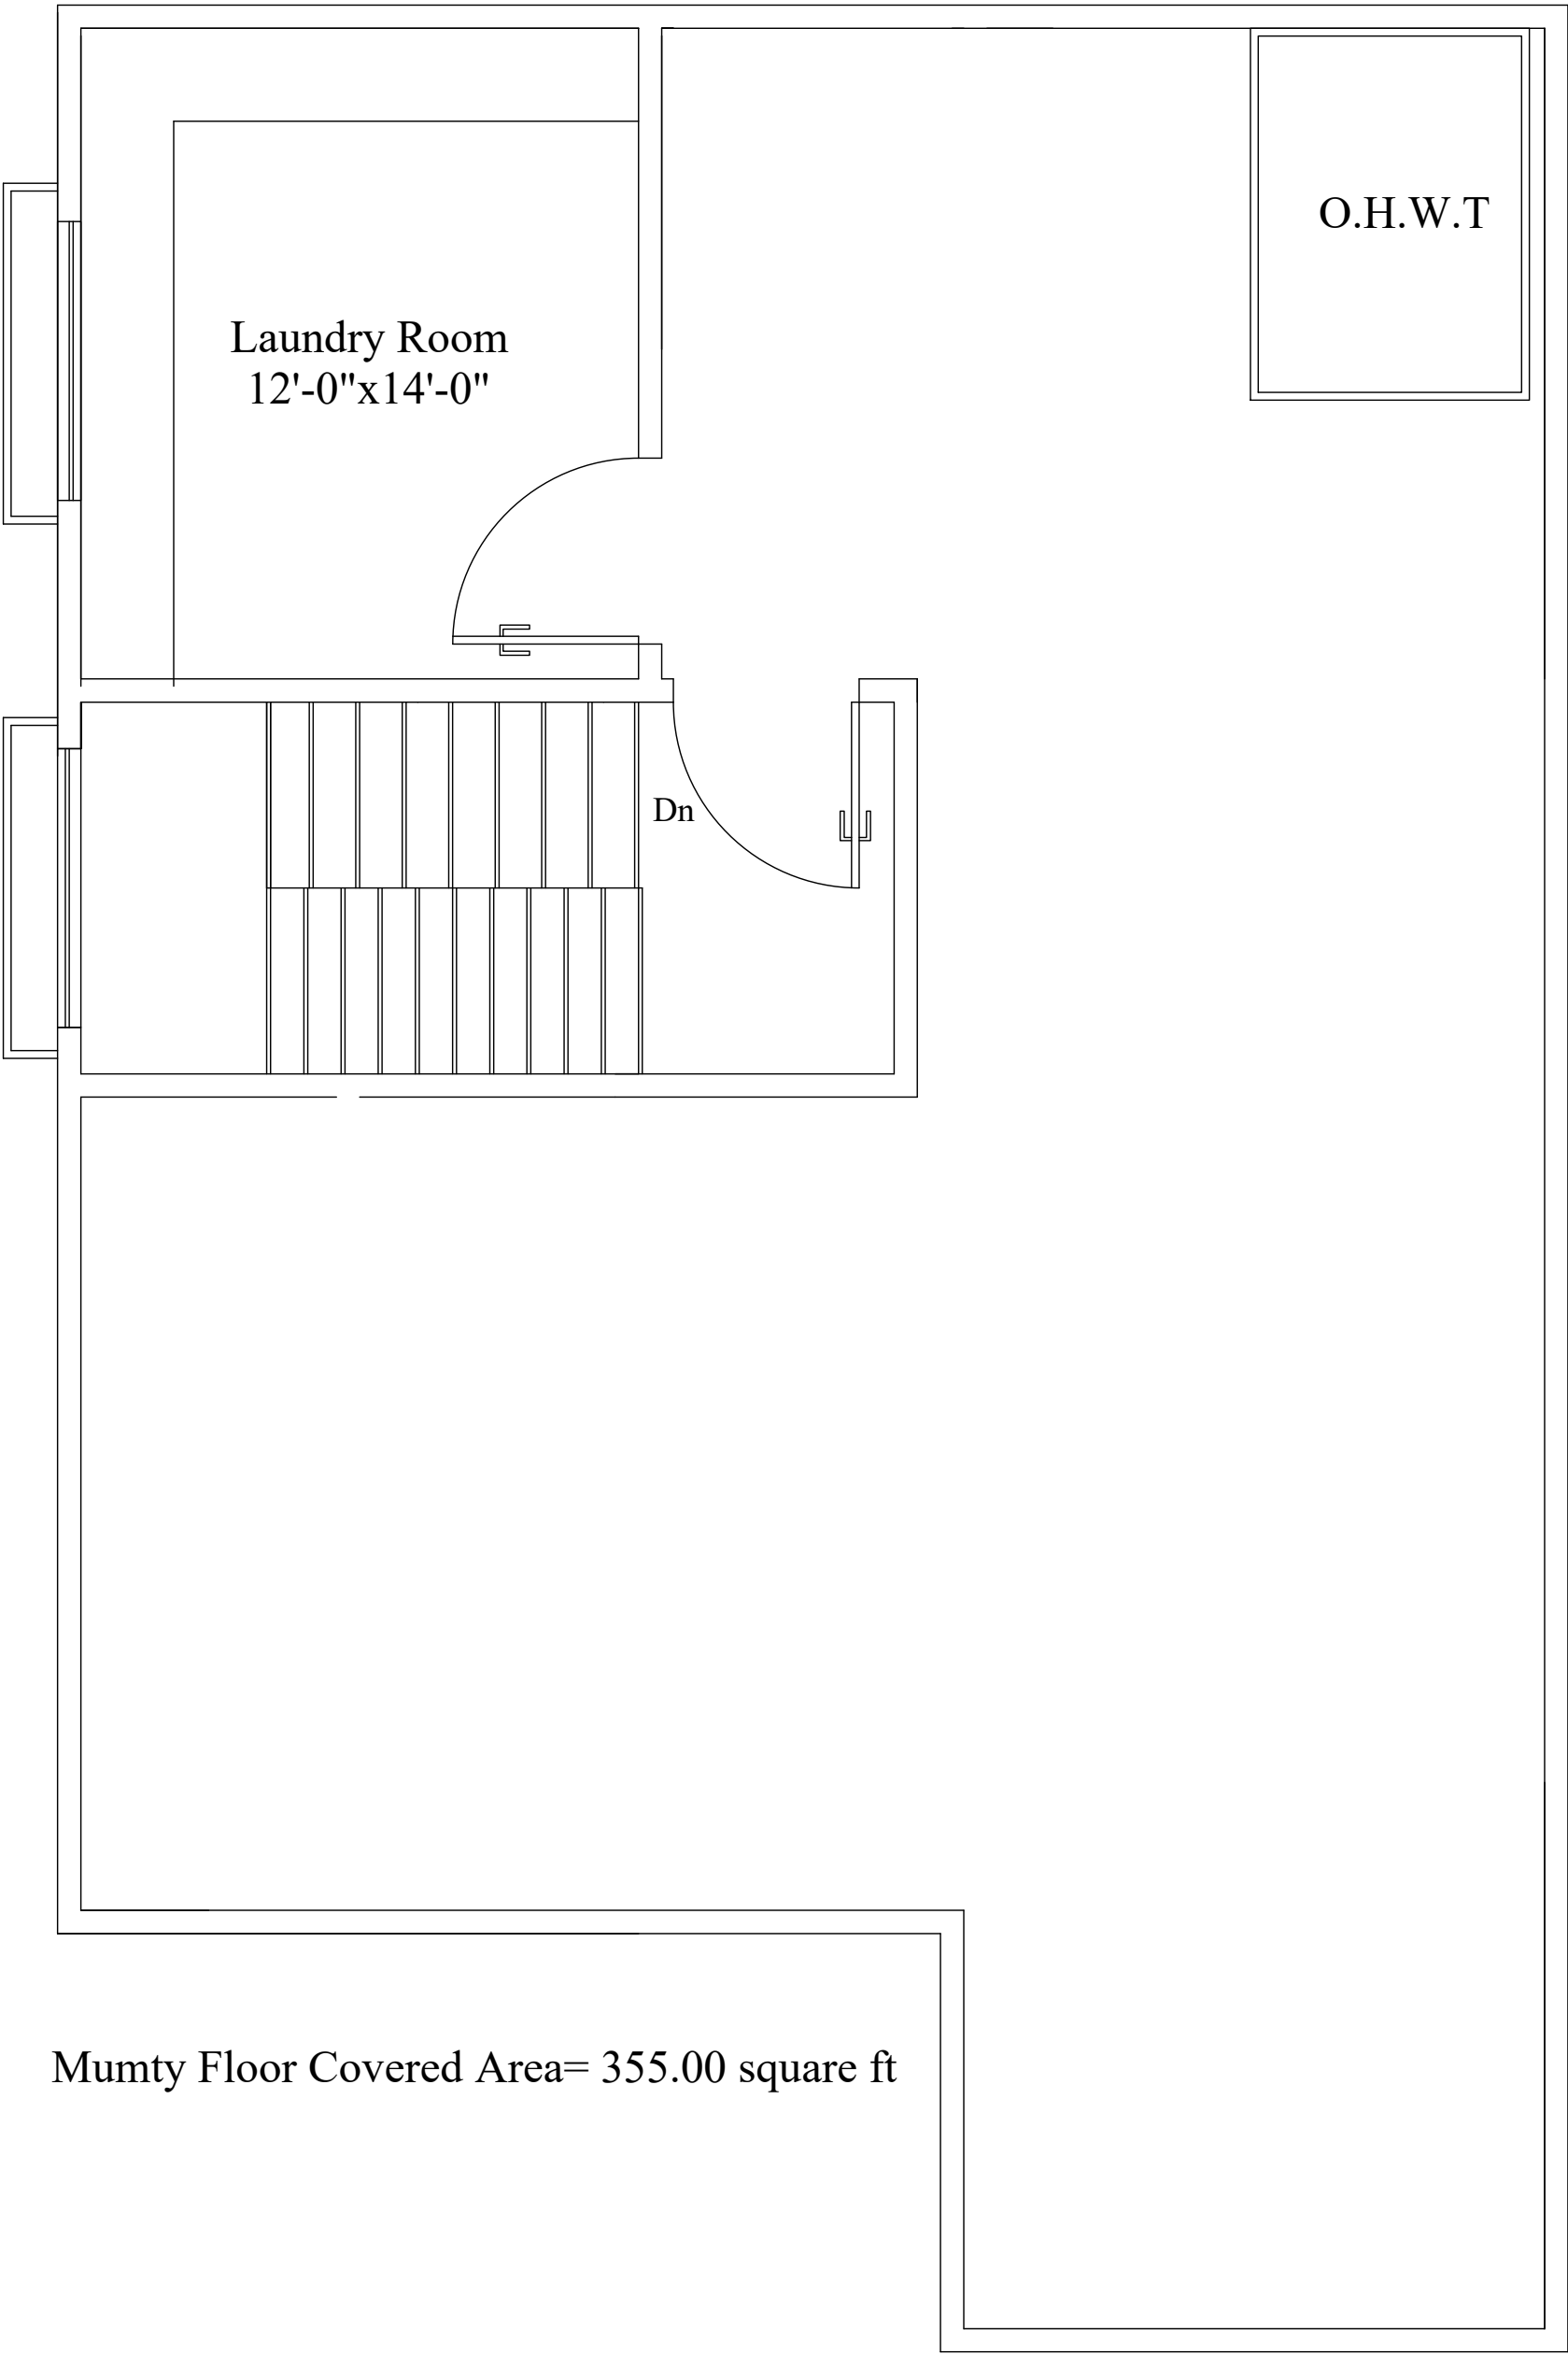

Mumty Floor Covered Area= 355.00 square ft


Project: Residential	Drawing:	Drawing Code:	Design By Wajid Khan: 0342-2421701
		S.No:	

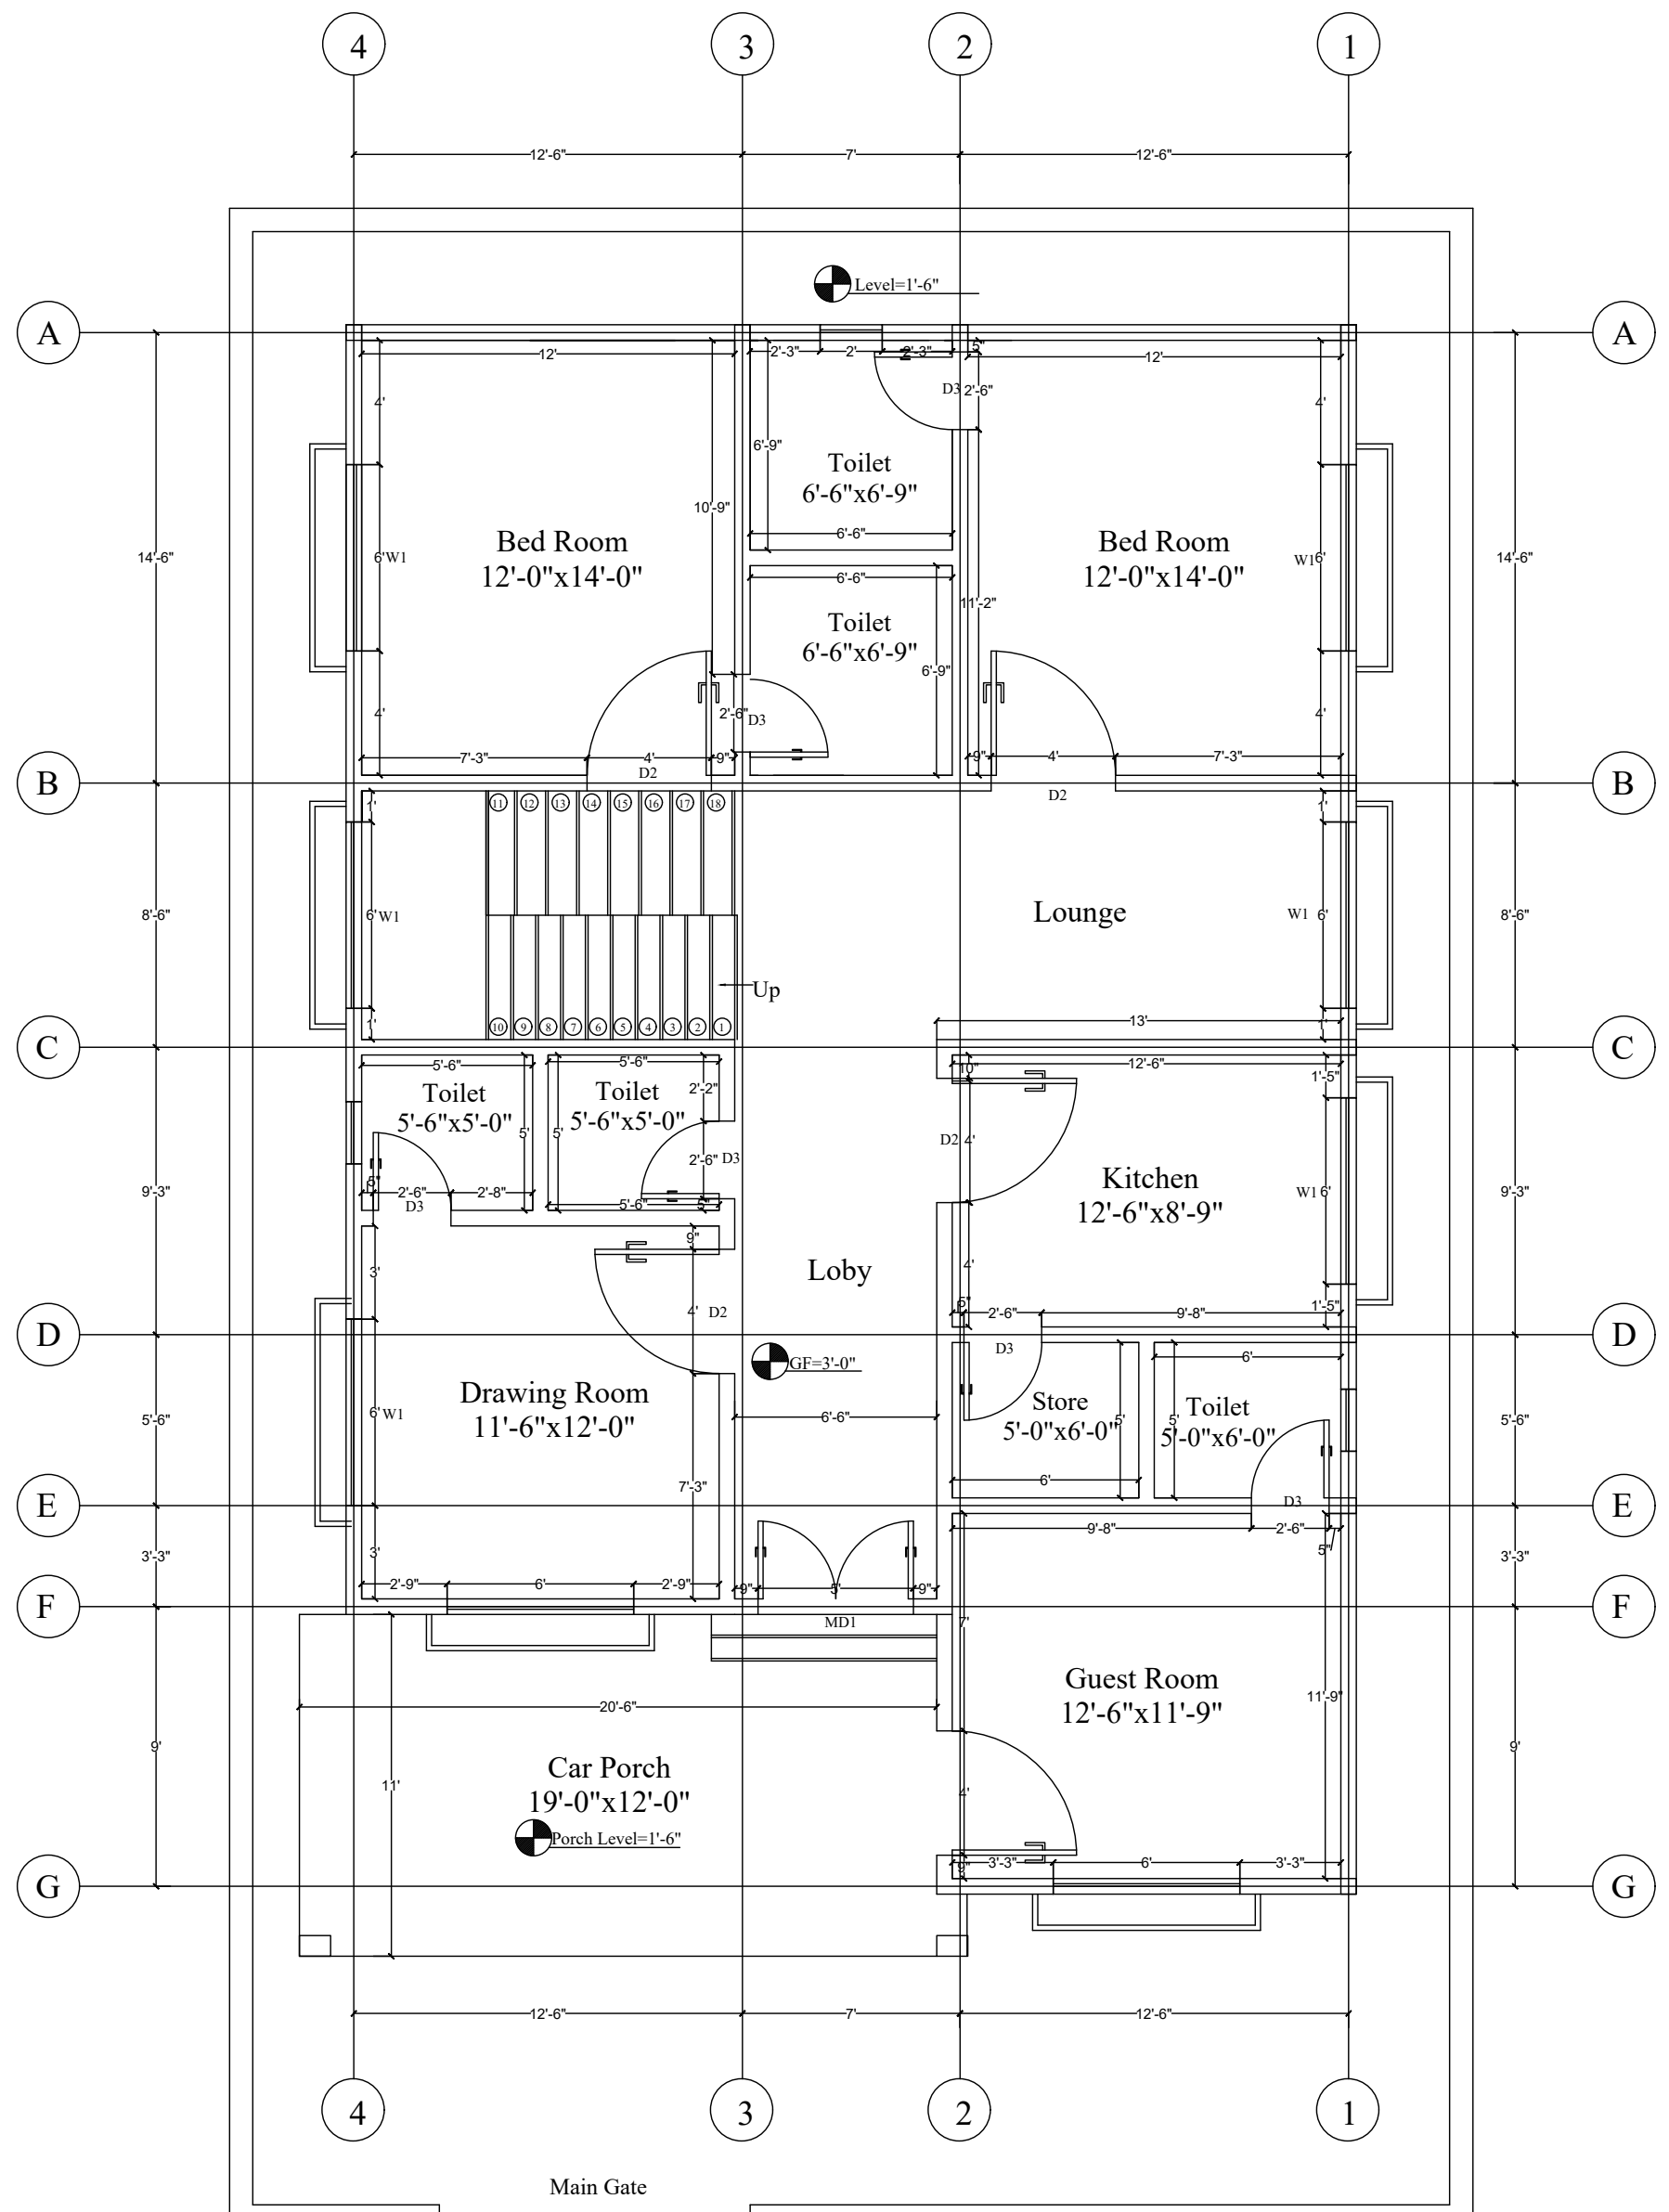

Ground Floor Covered Area= 1697.75 square ft

Road Level=0'-0"

Project: Residential	Drawing:	Drawing Code: S.No:	Design By Wajid Khan: 0342-2421701
-------------------------	----------	------------------------	---------------------------------------

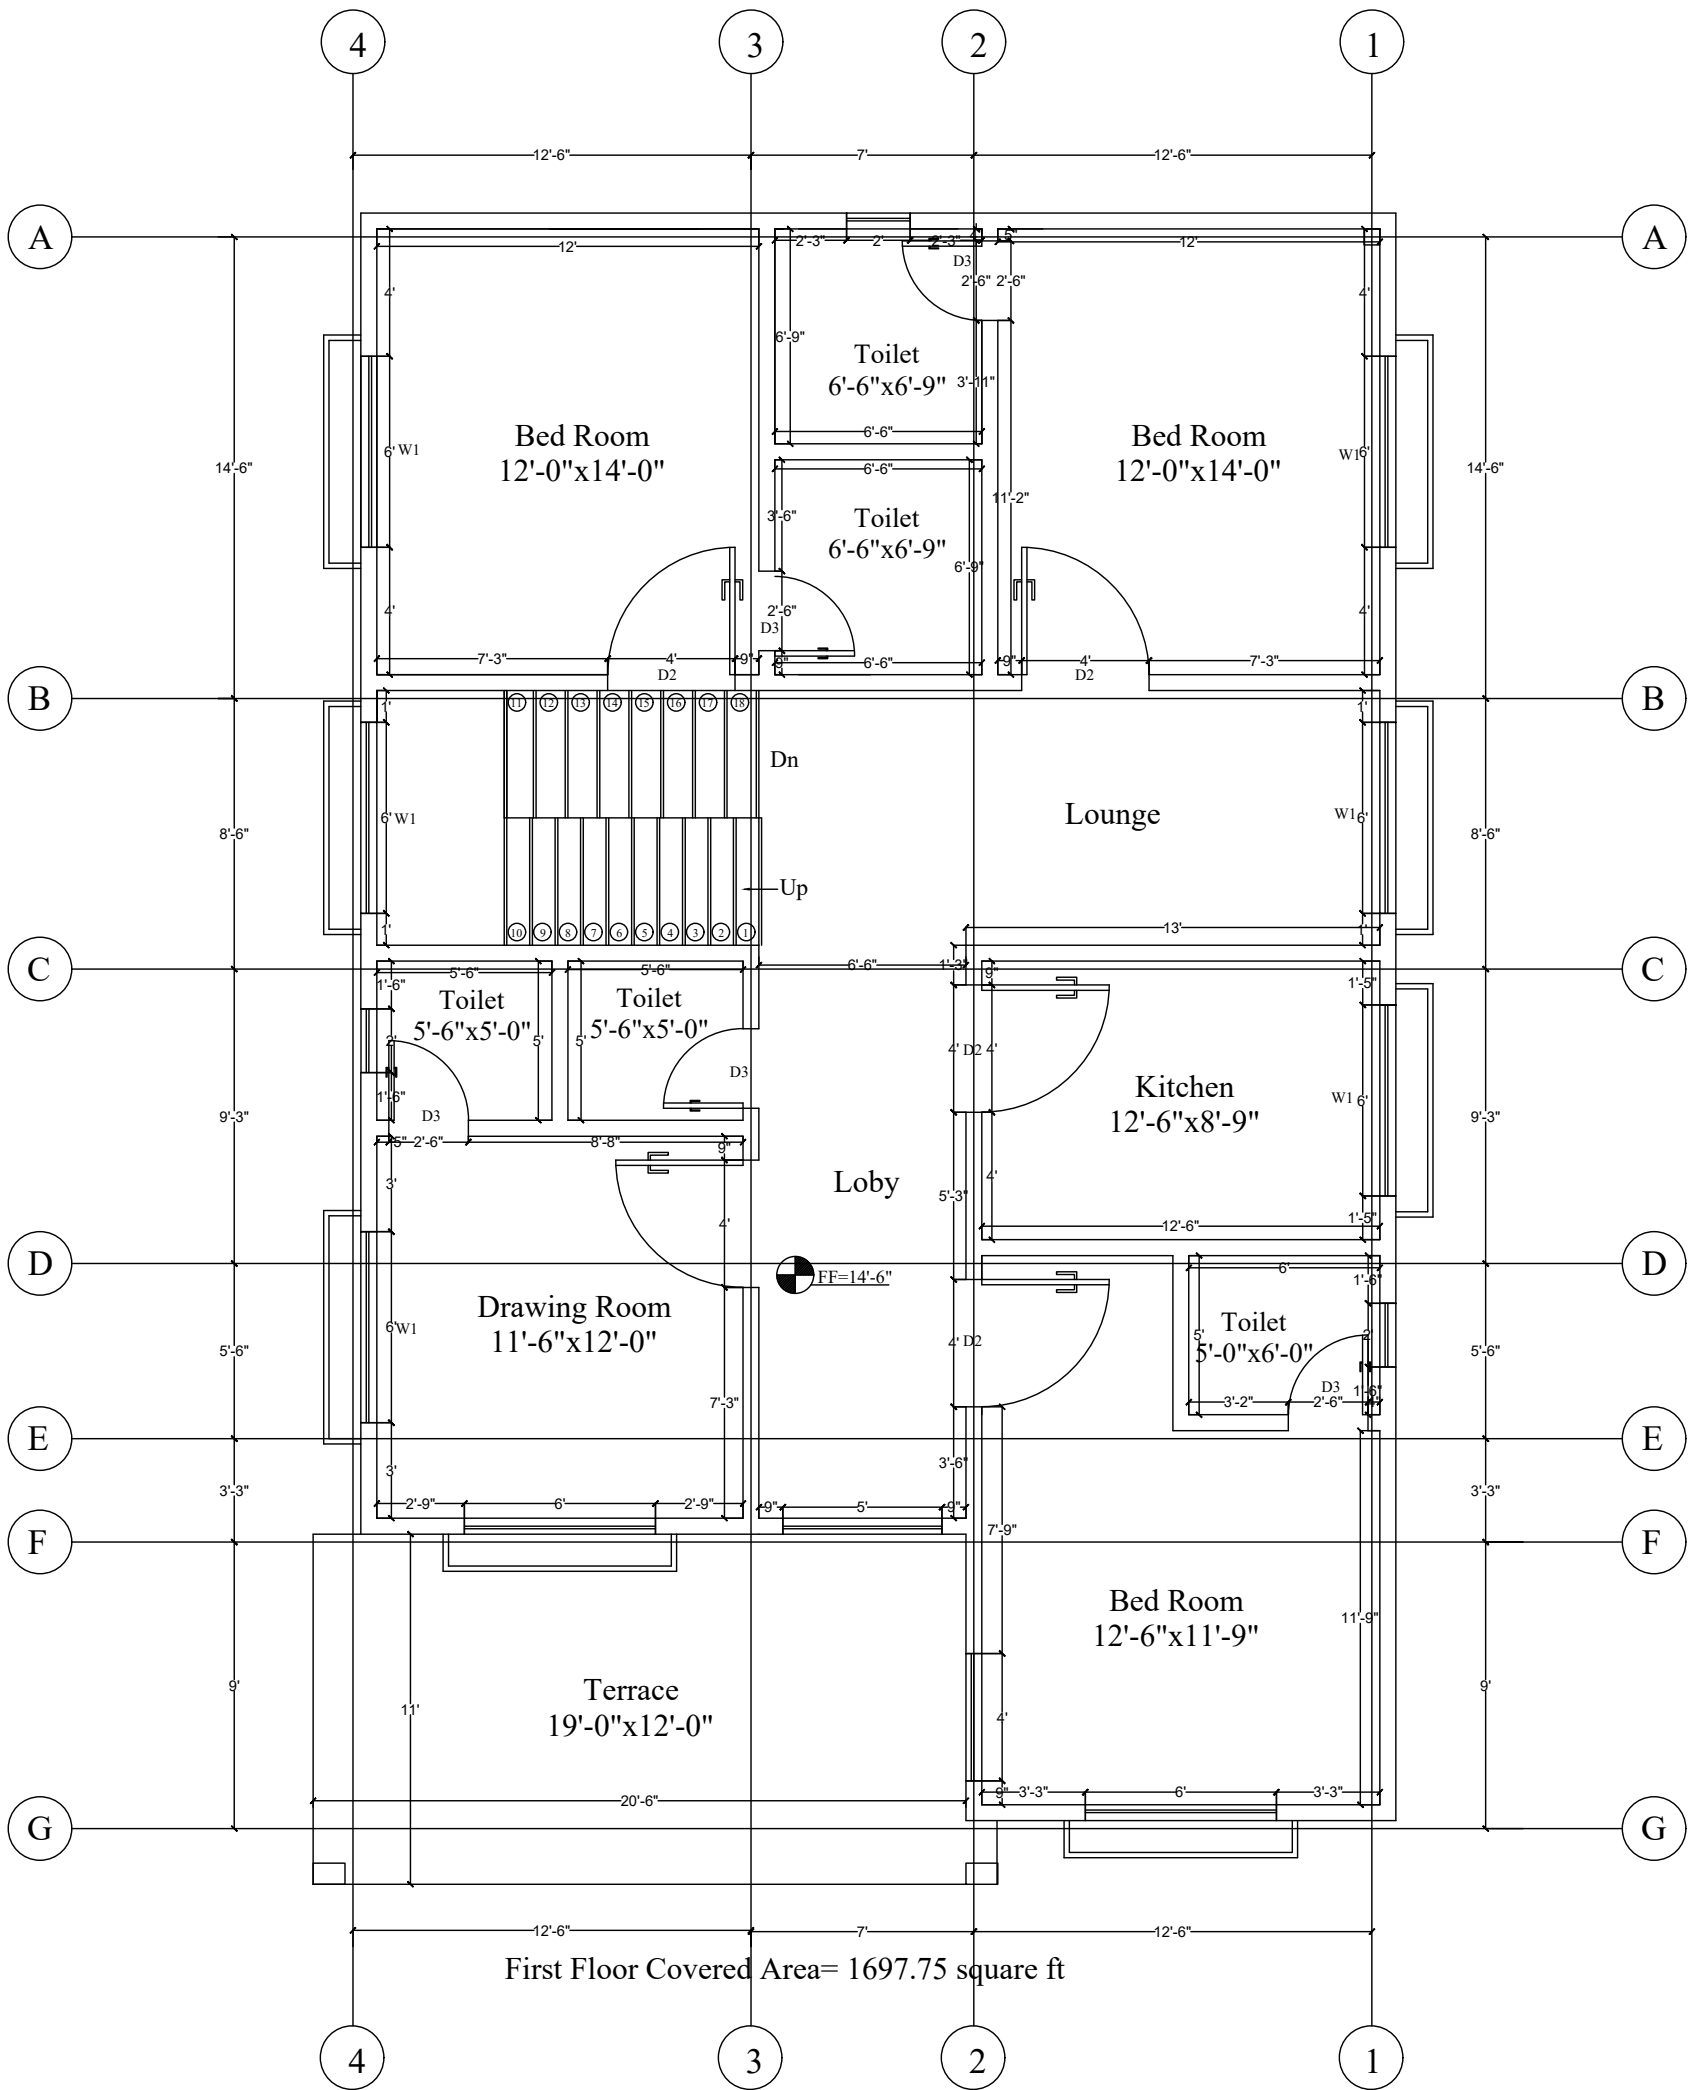


Project:
Residential


Drawing:

Drawing Code:

S.No:


Design By
Wajid Khan: 0342-2421701

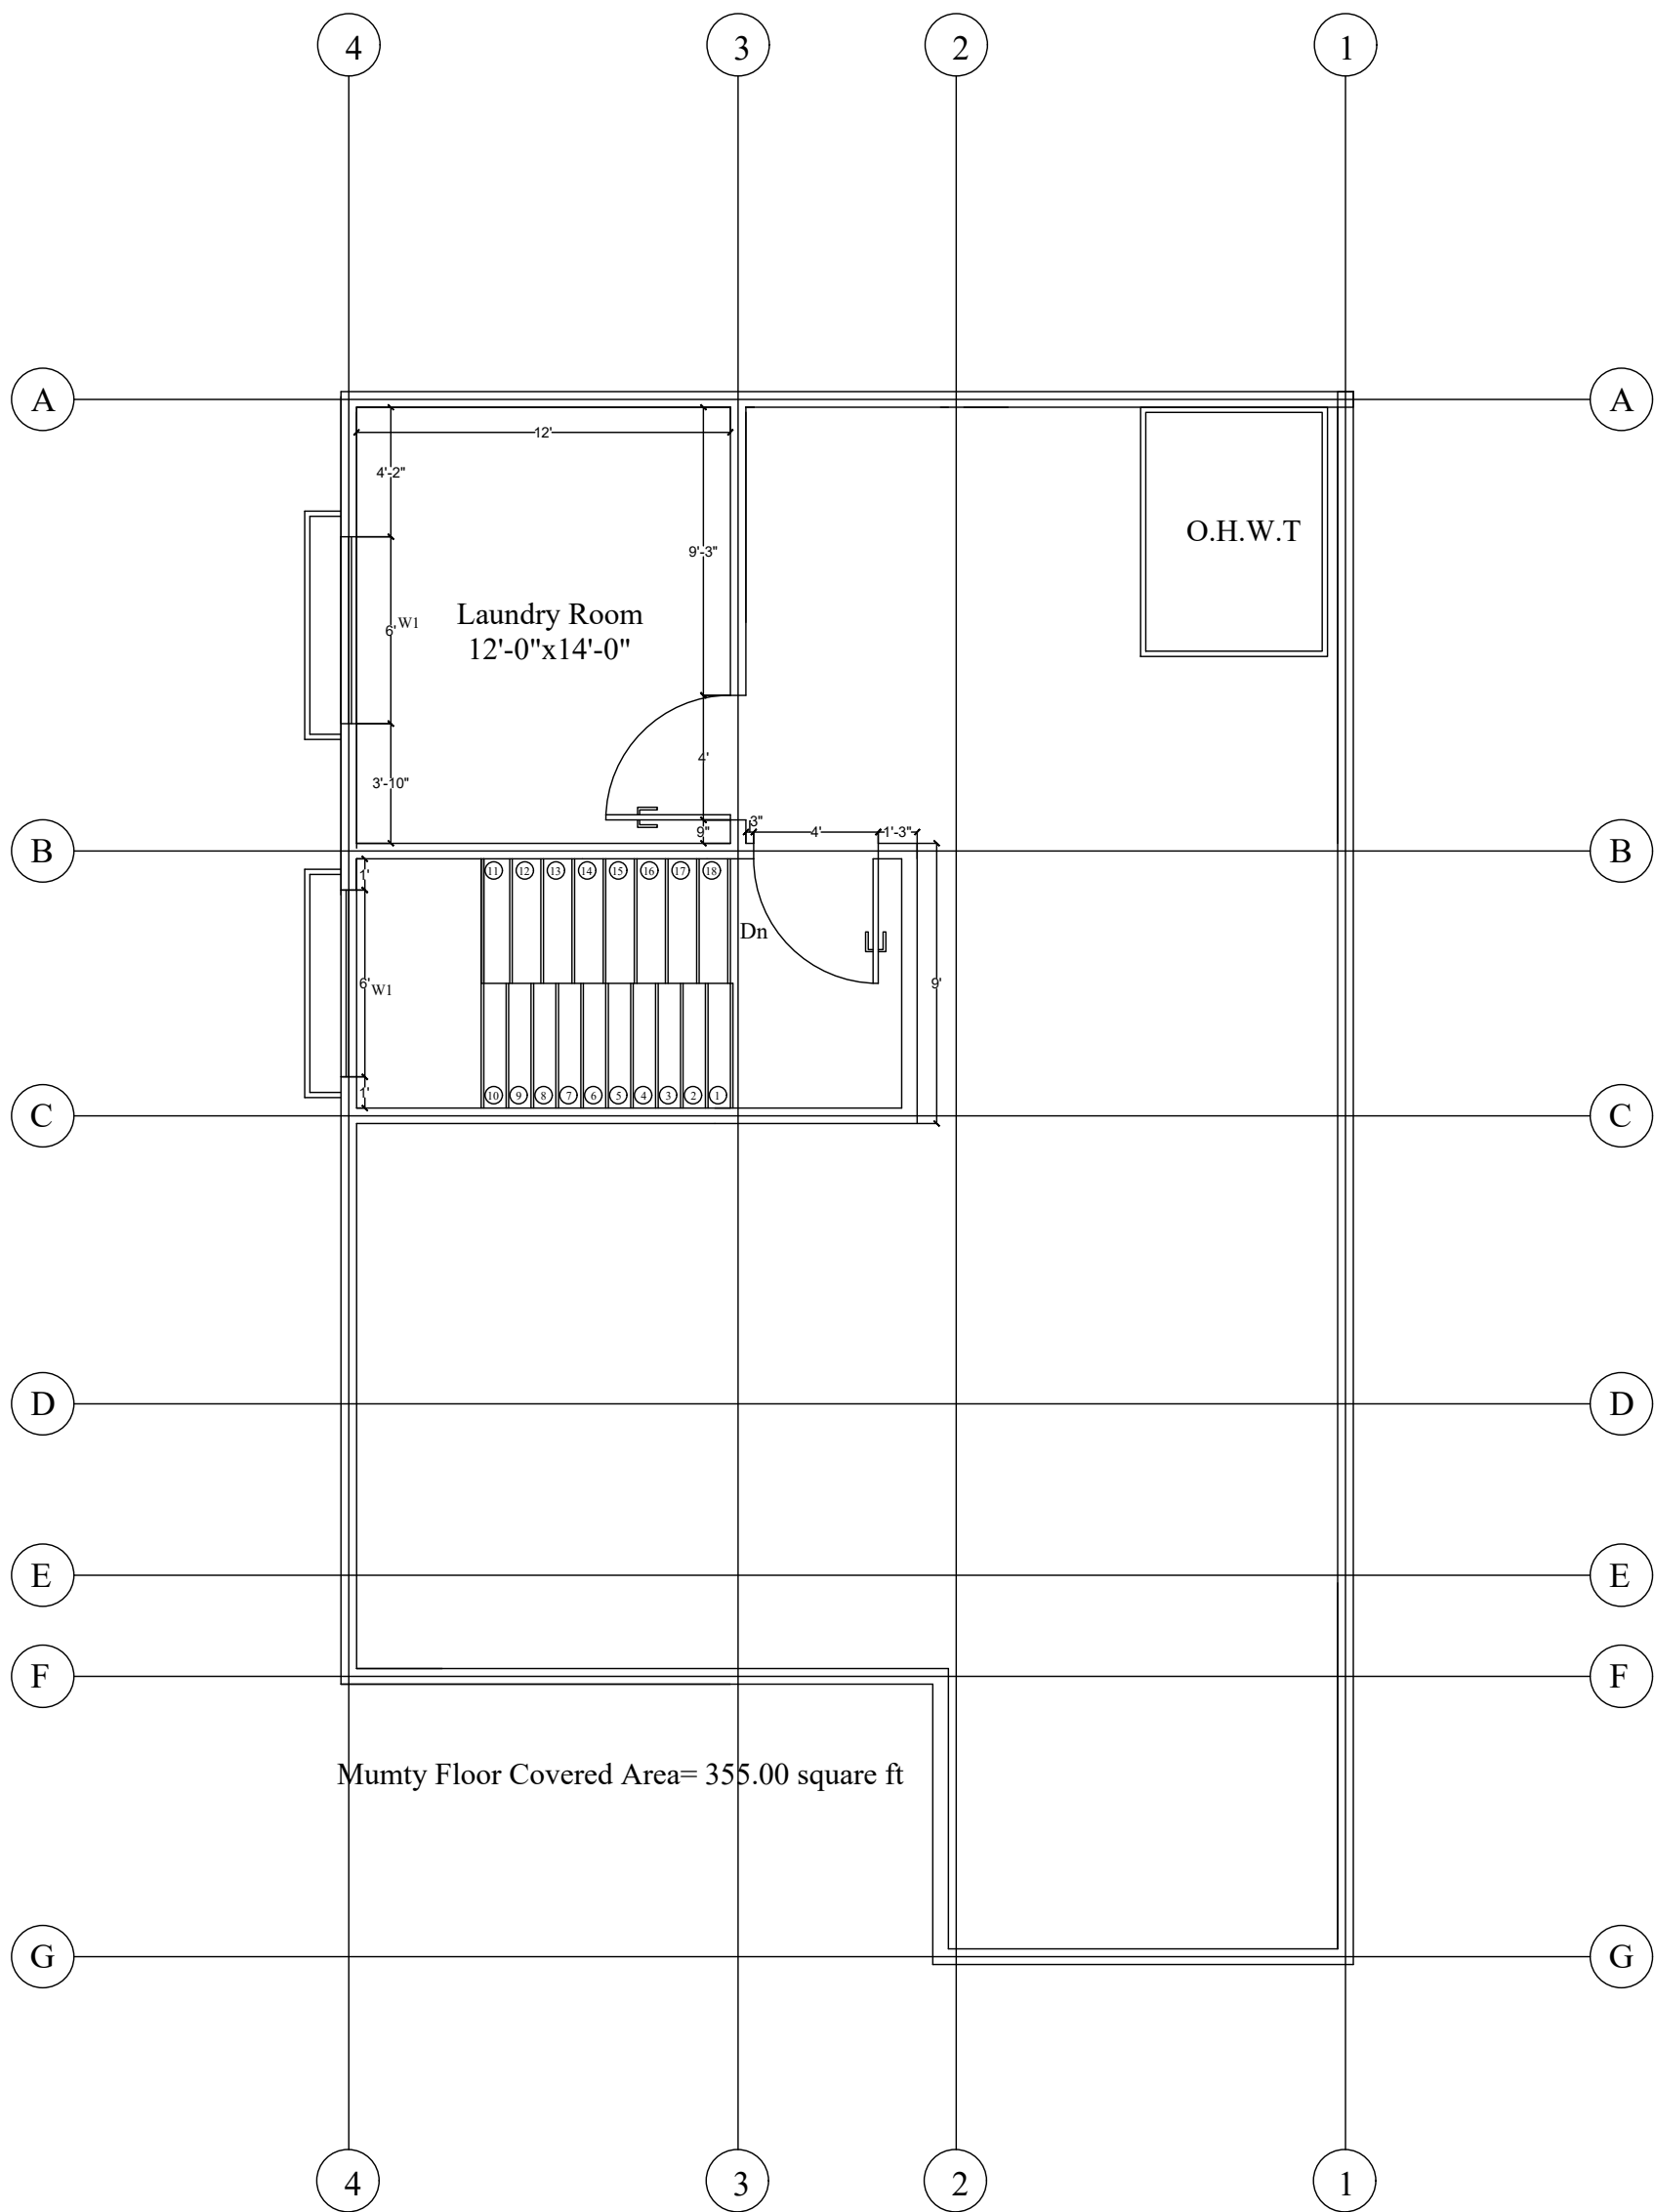

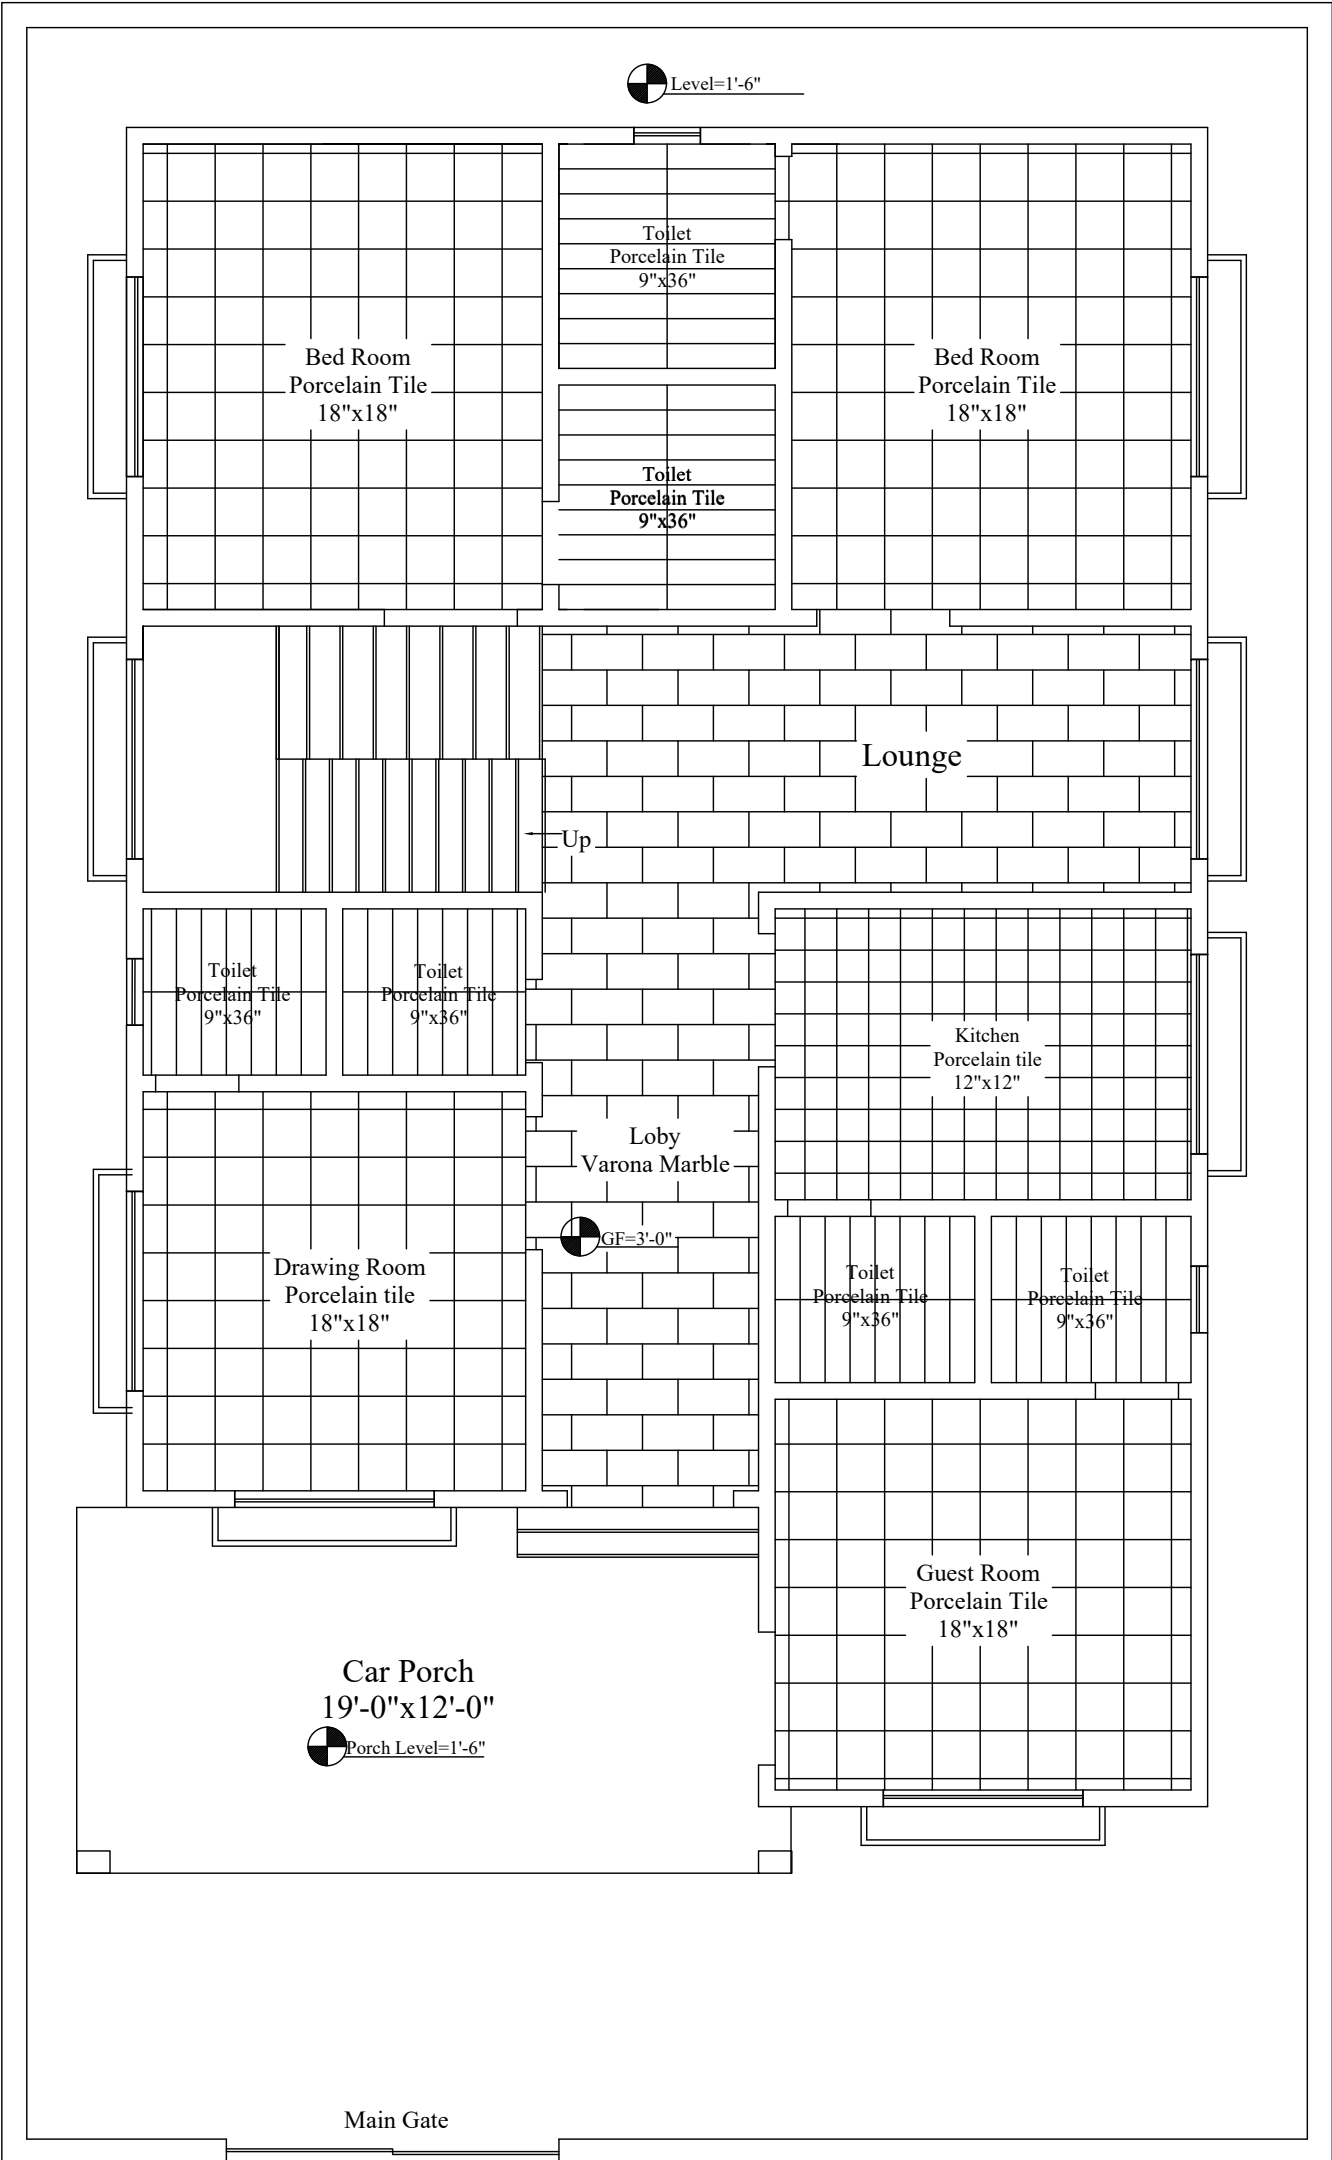

Road Level=0'-0"

Project: Residential	Drawing:	Drawing Code:	Design By Wajid Khan: 0342-2421701
		S.No:	

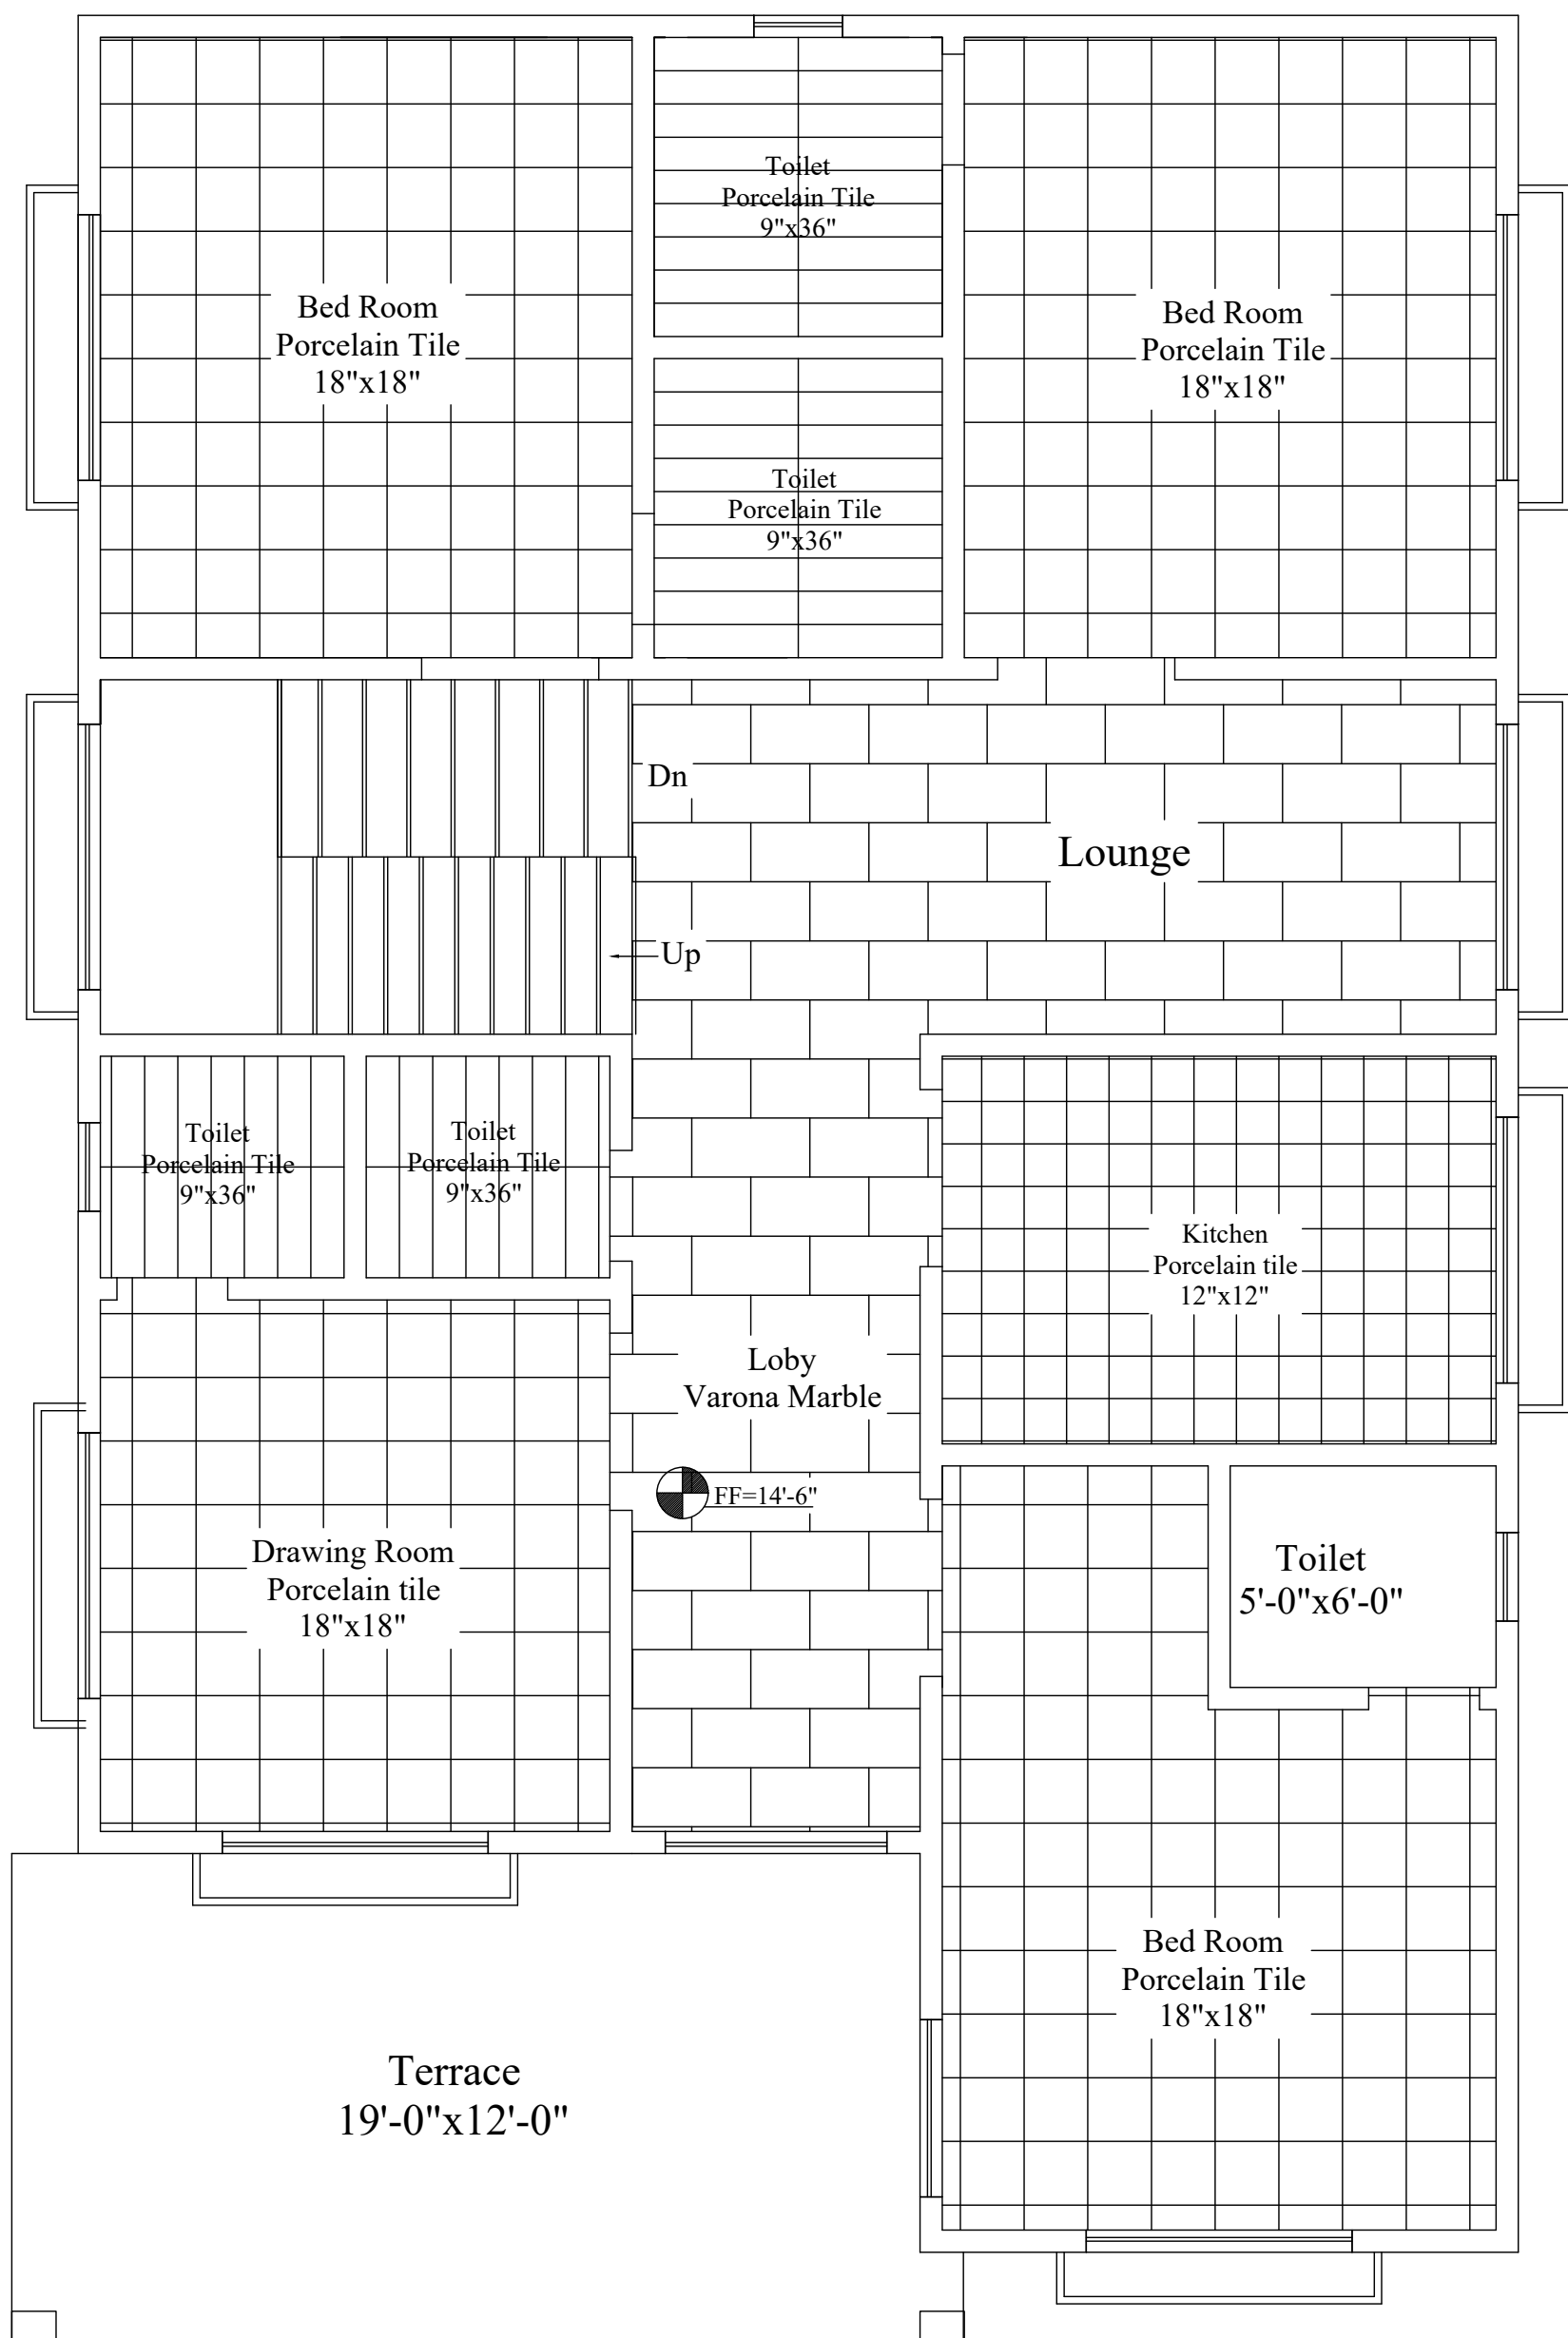

First Floor Covered Area= 1697.75 square ft


Project:
Residential

Drawing:


Drawing Code:

S.No:

Design By
Wajid Khan: 0342-2421701

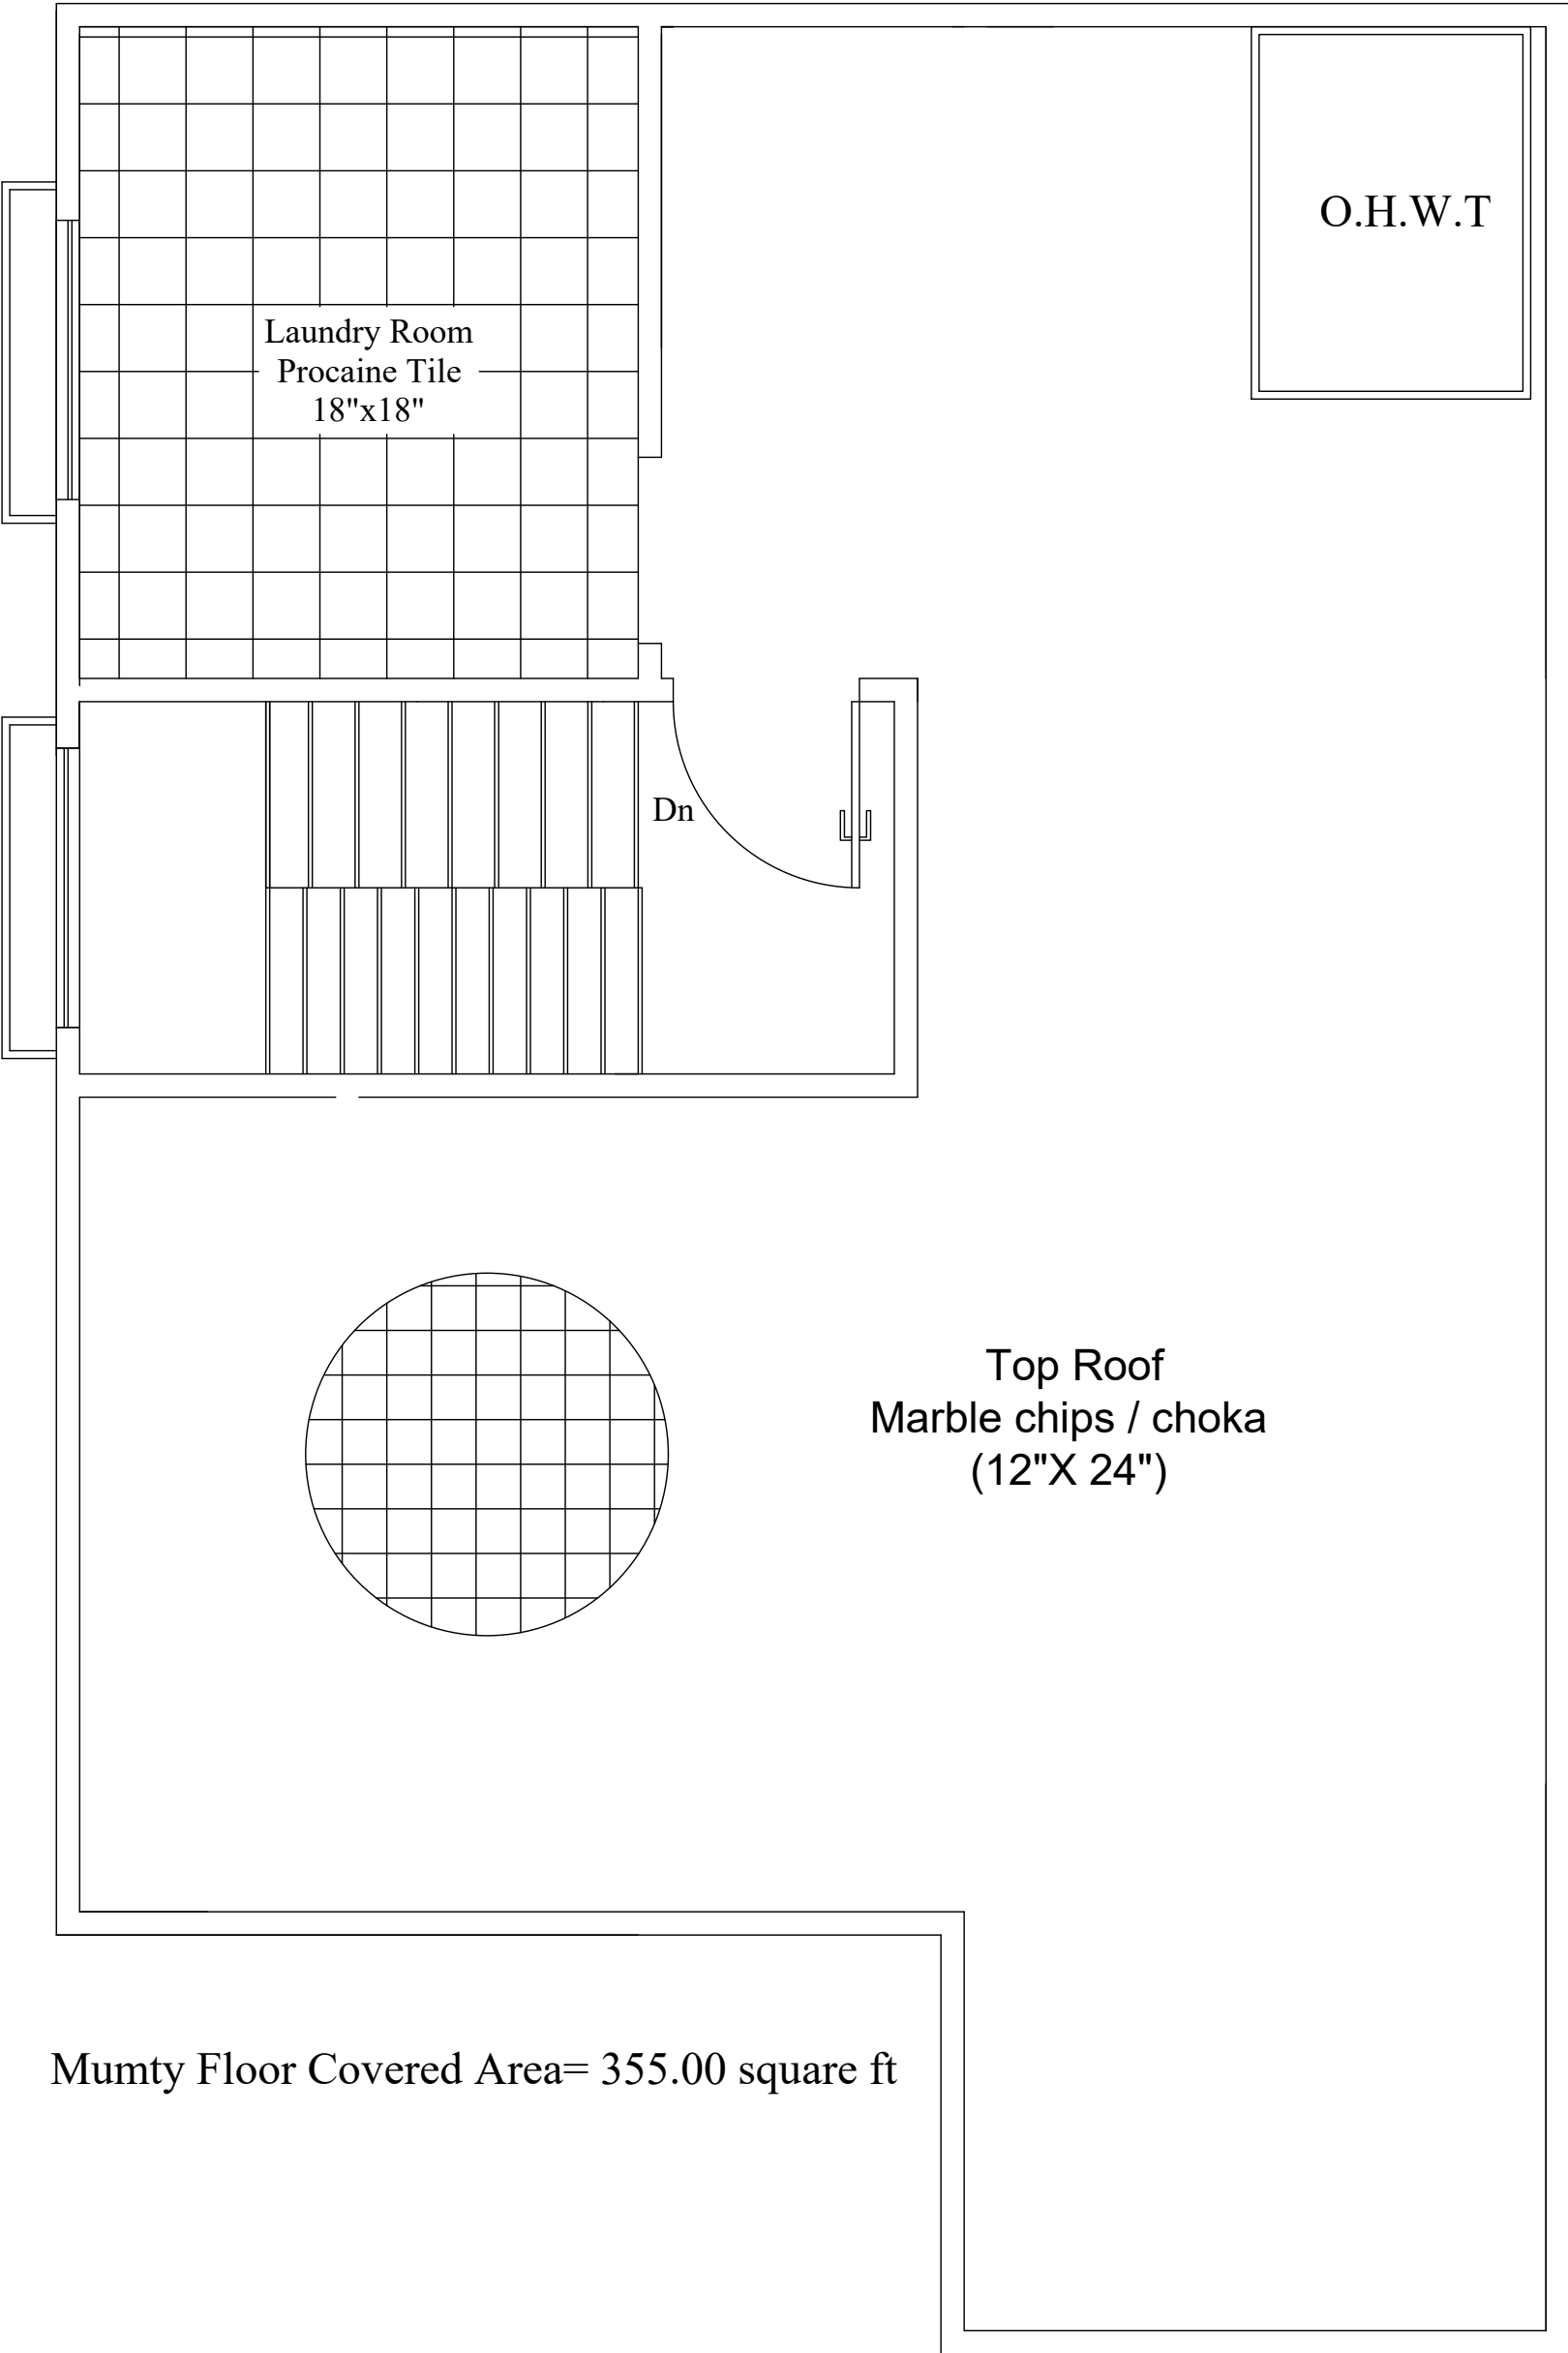


Project: Residential	Drawing:	Drawing Code:	Design By Wajid Khan: 0342-2421701
		S.No:	

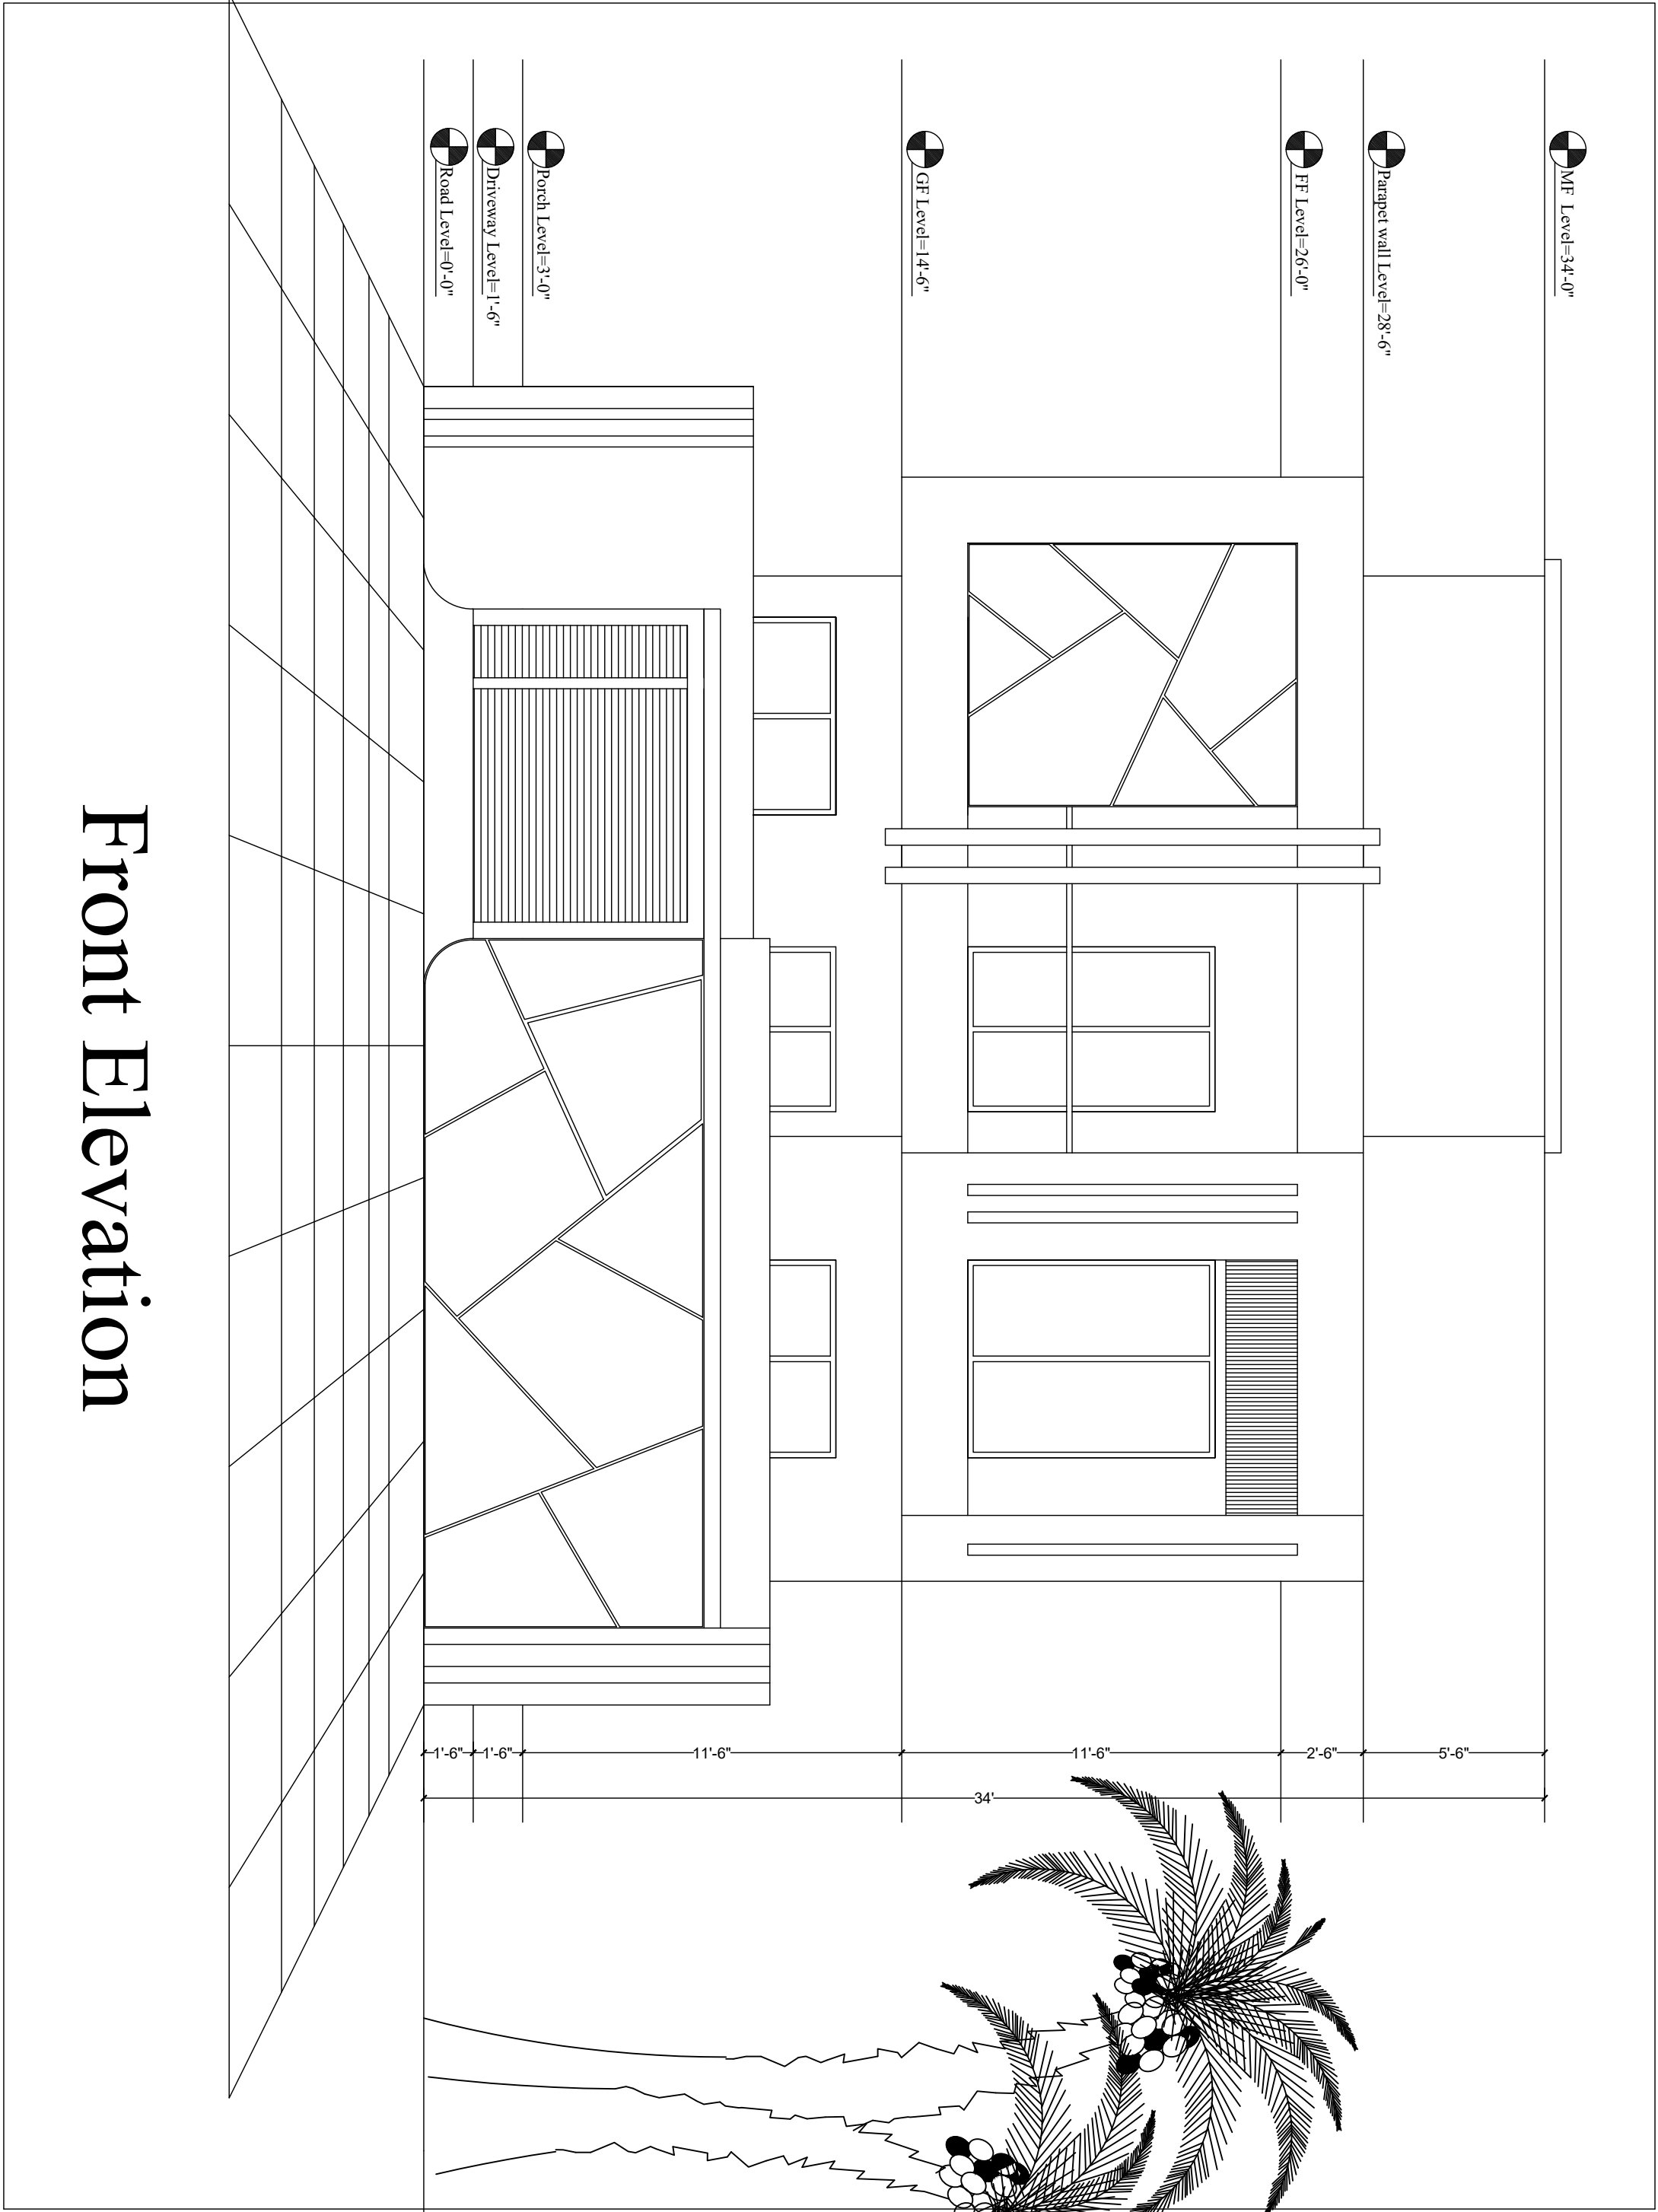

Front Elevation

Project: Residential	Drawing:	Drawing Code:	Design By
		S.No:	Wajid Khan: 0342-2421701

Right Elevation

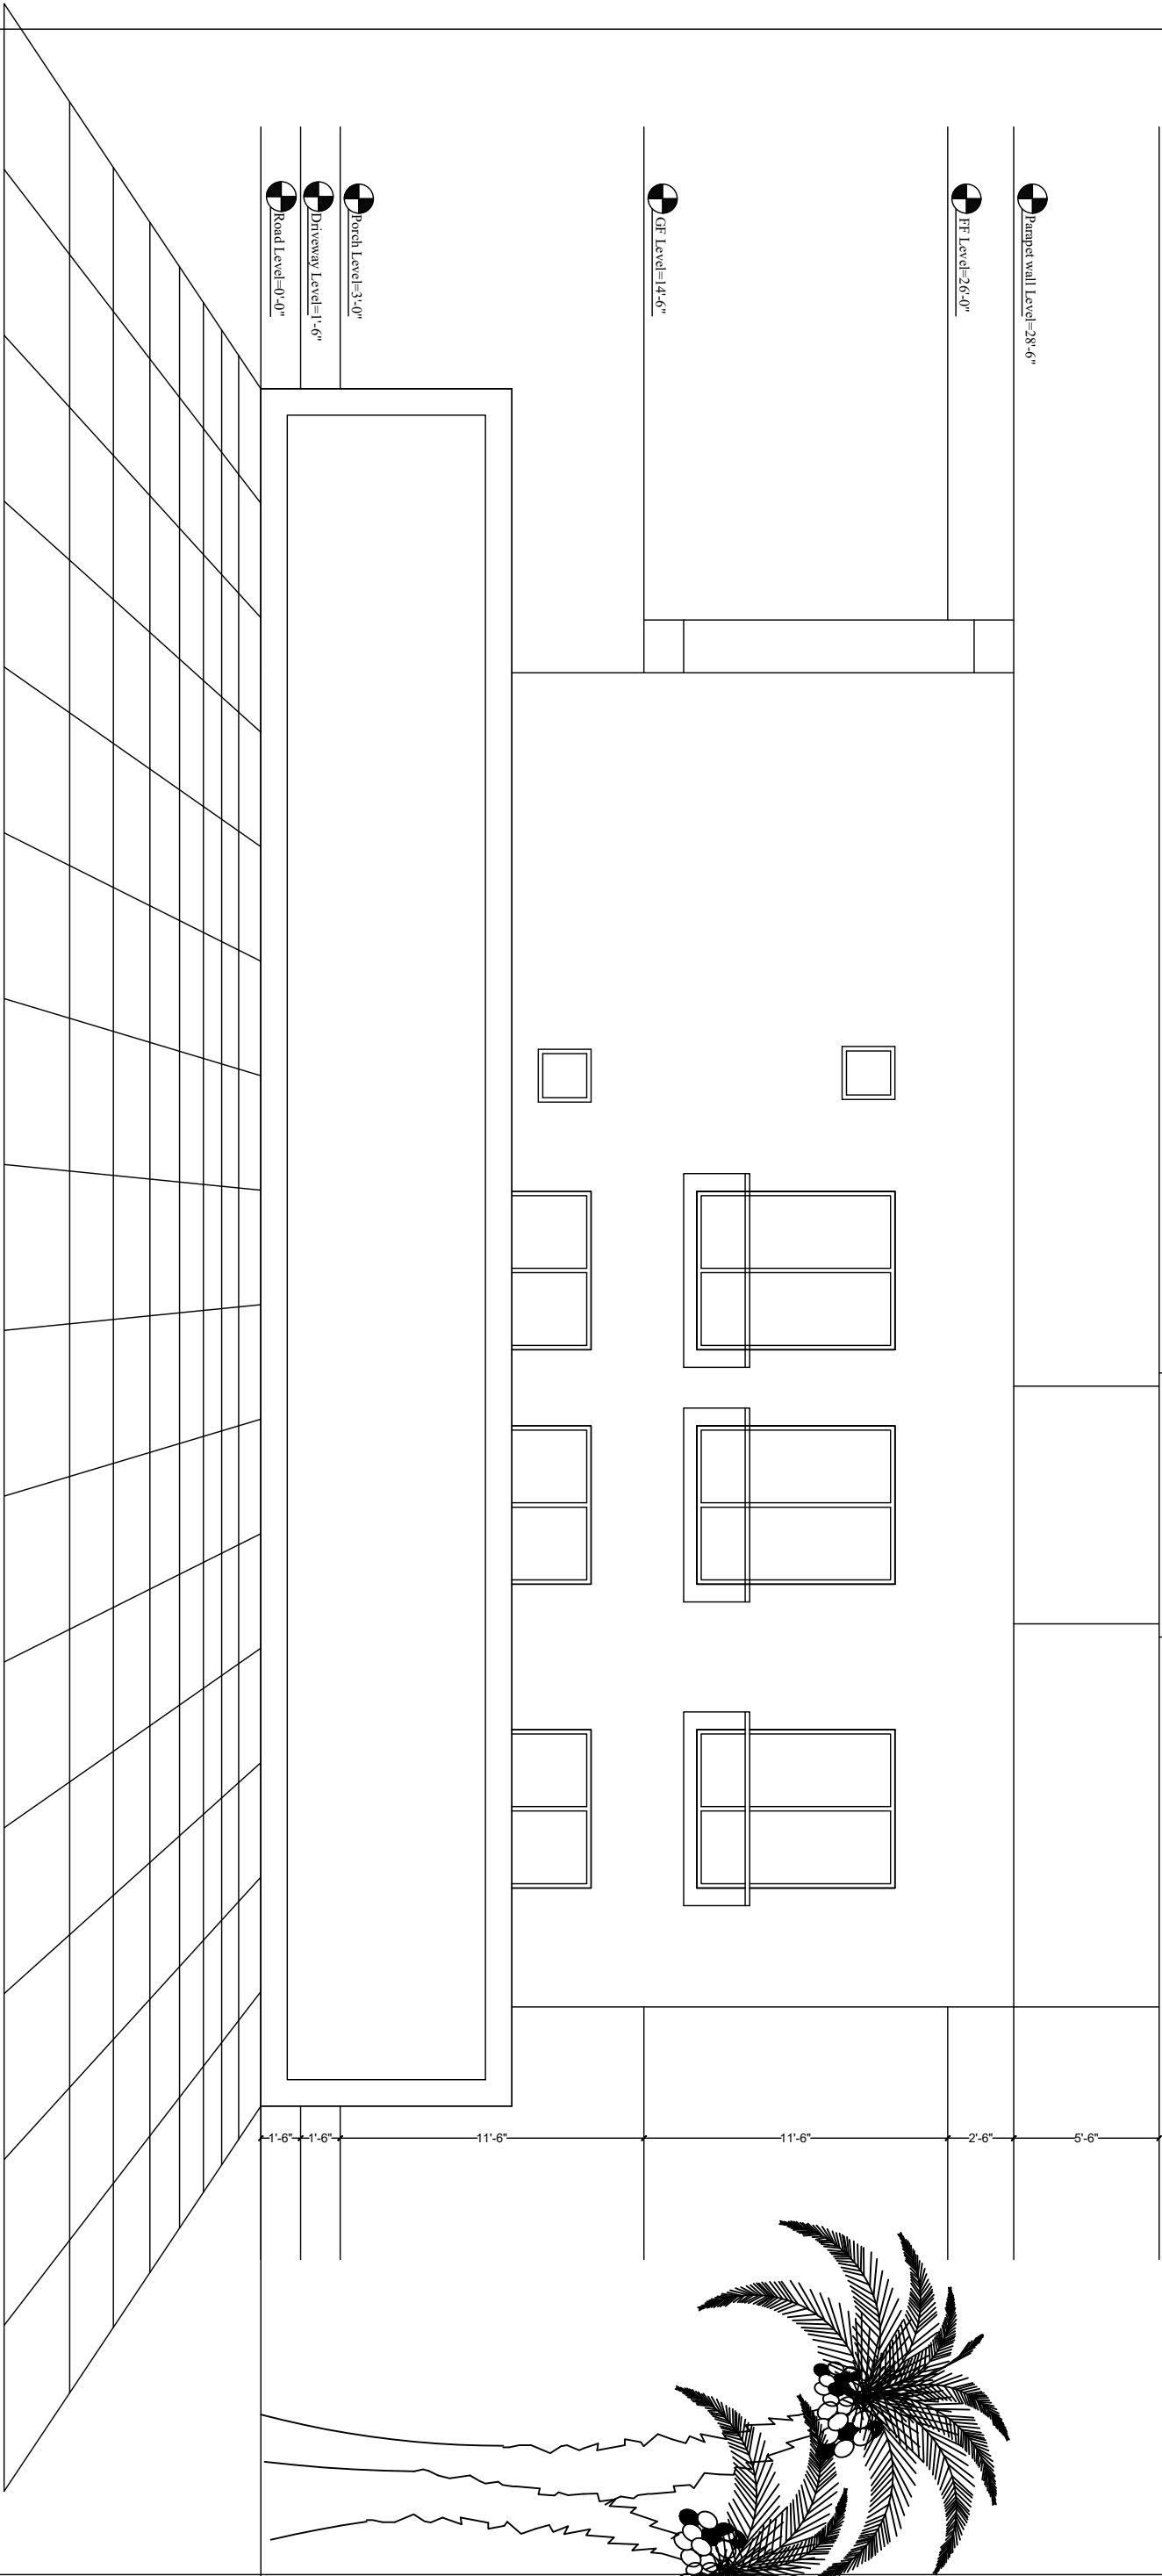


Project:
Residential


Drawing:

Drawing Code
S.No:


Design By
Wajid Khan: 0342-2421701

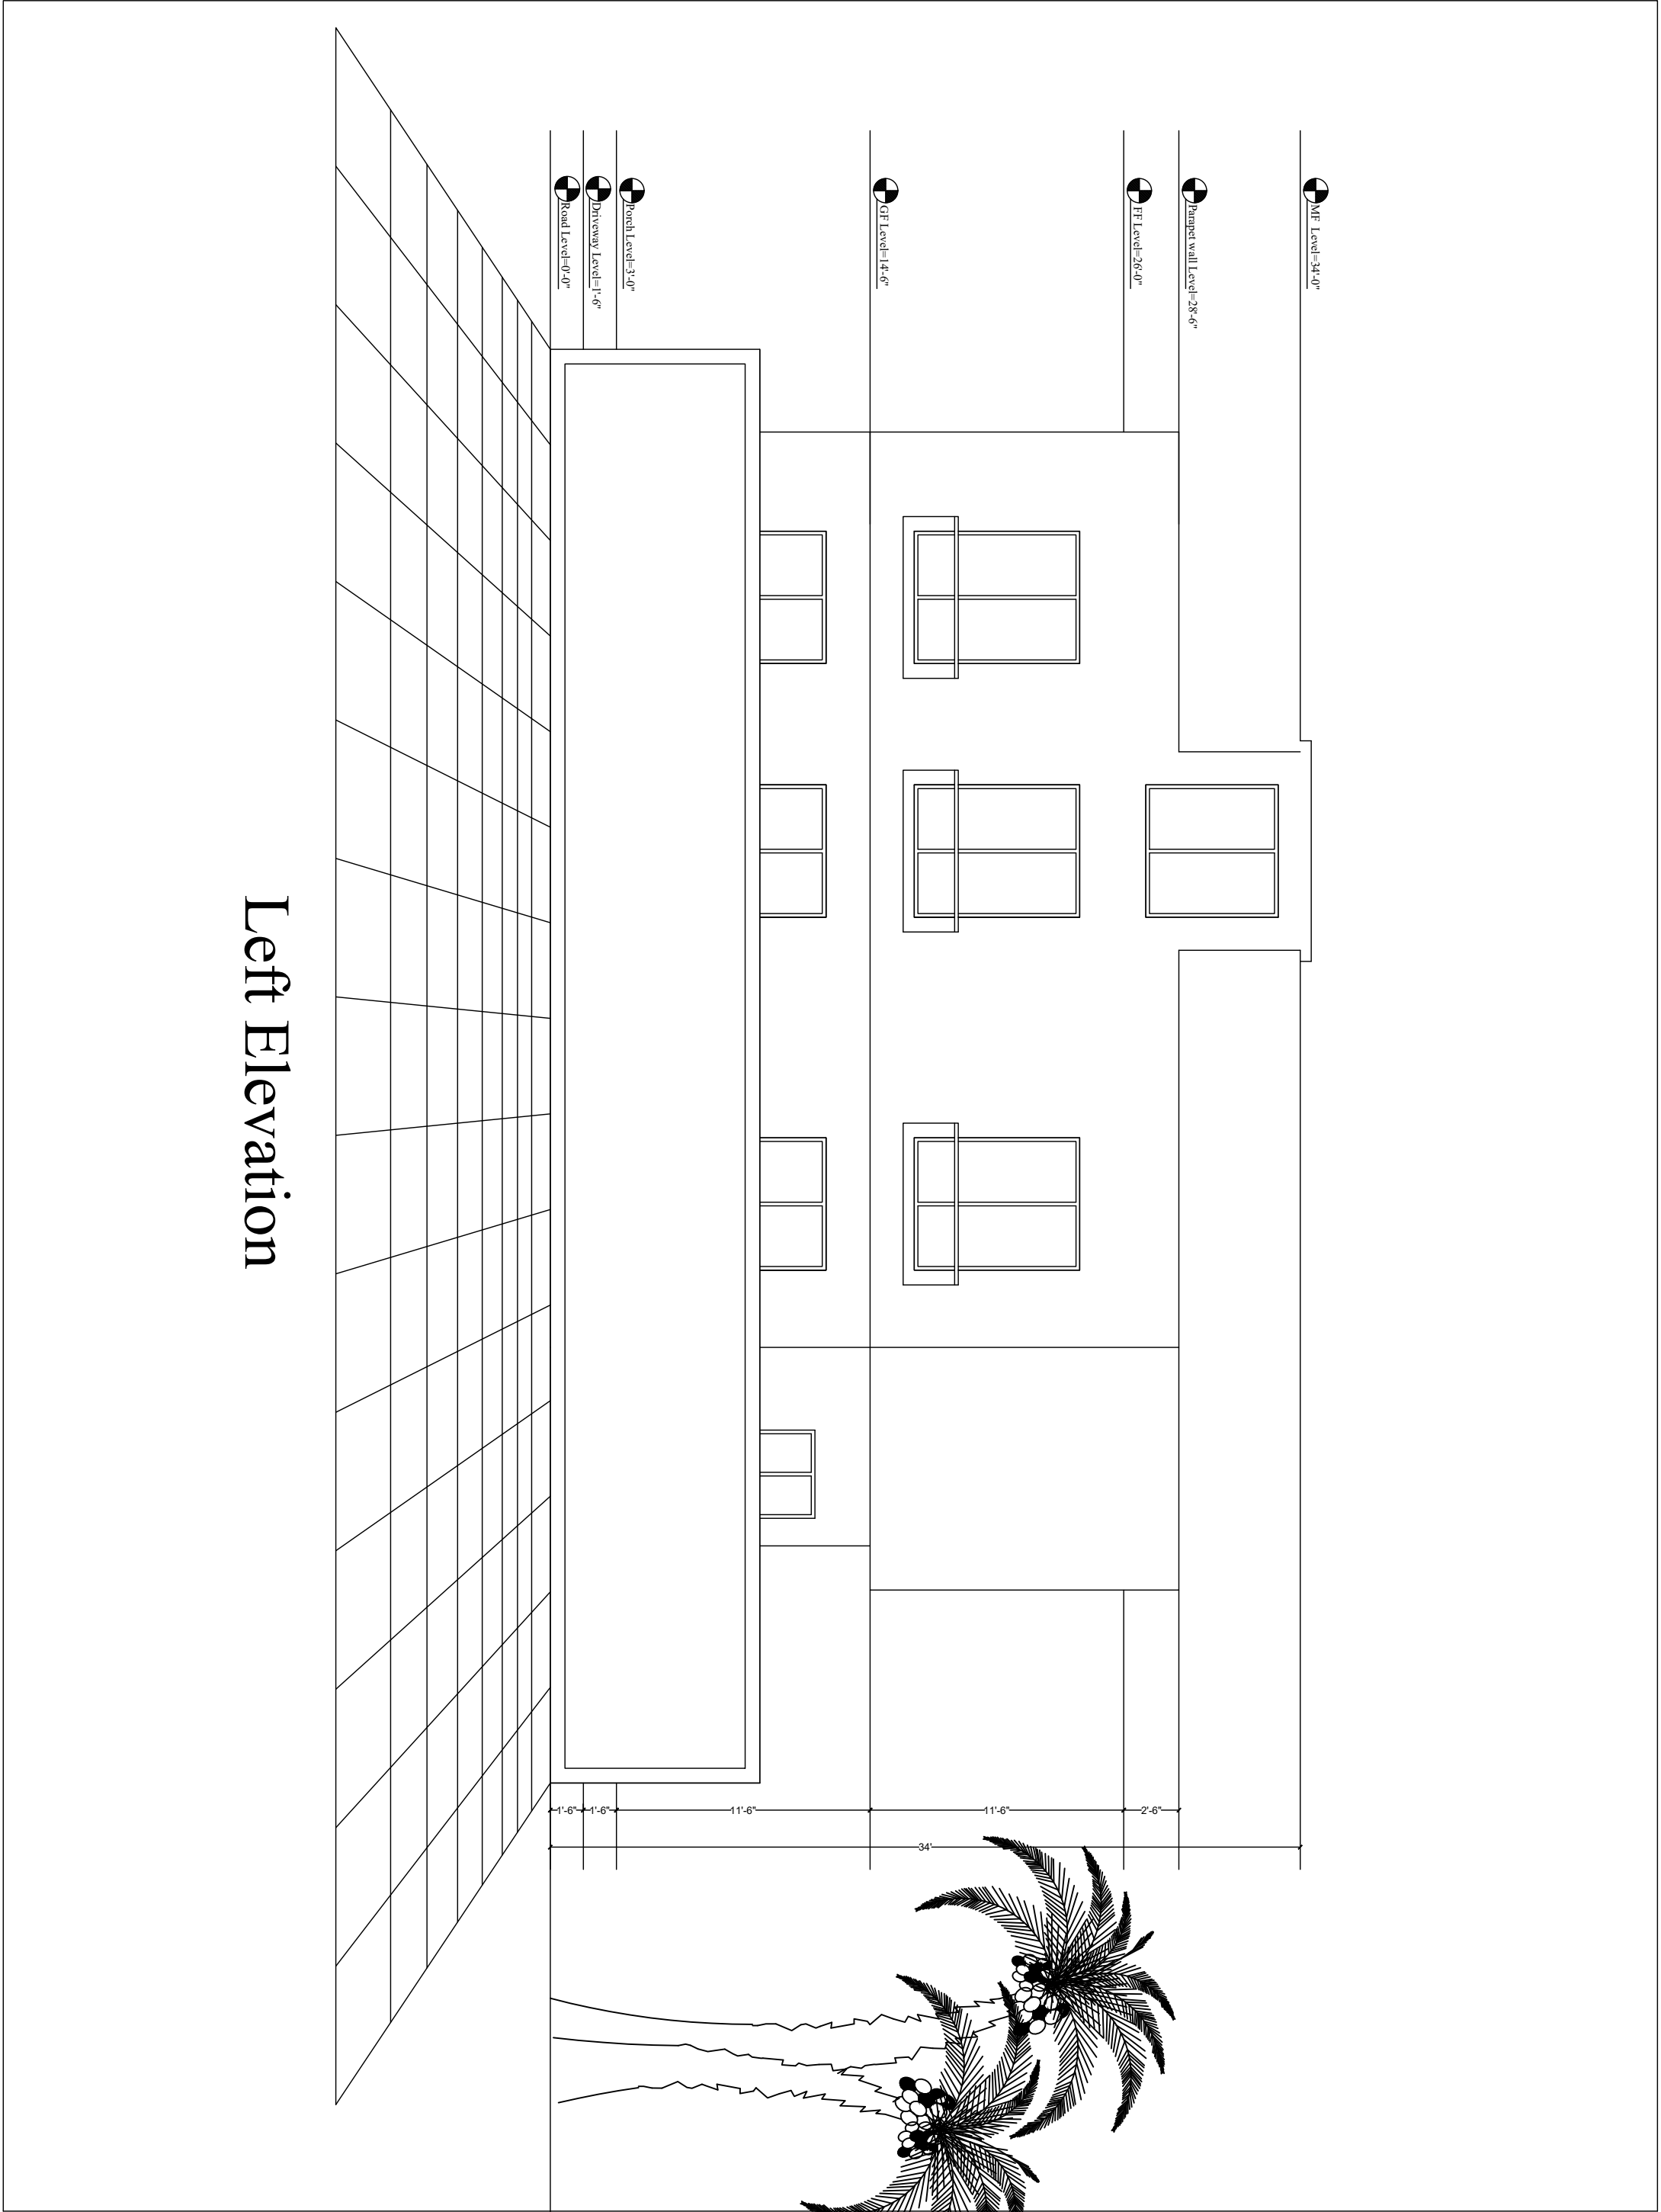

Project: Residential	Drawing:	Drawing Code:	Design By Wajid Khan: 0342-2421701
		S.No:	

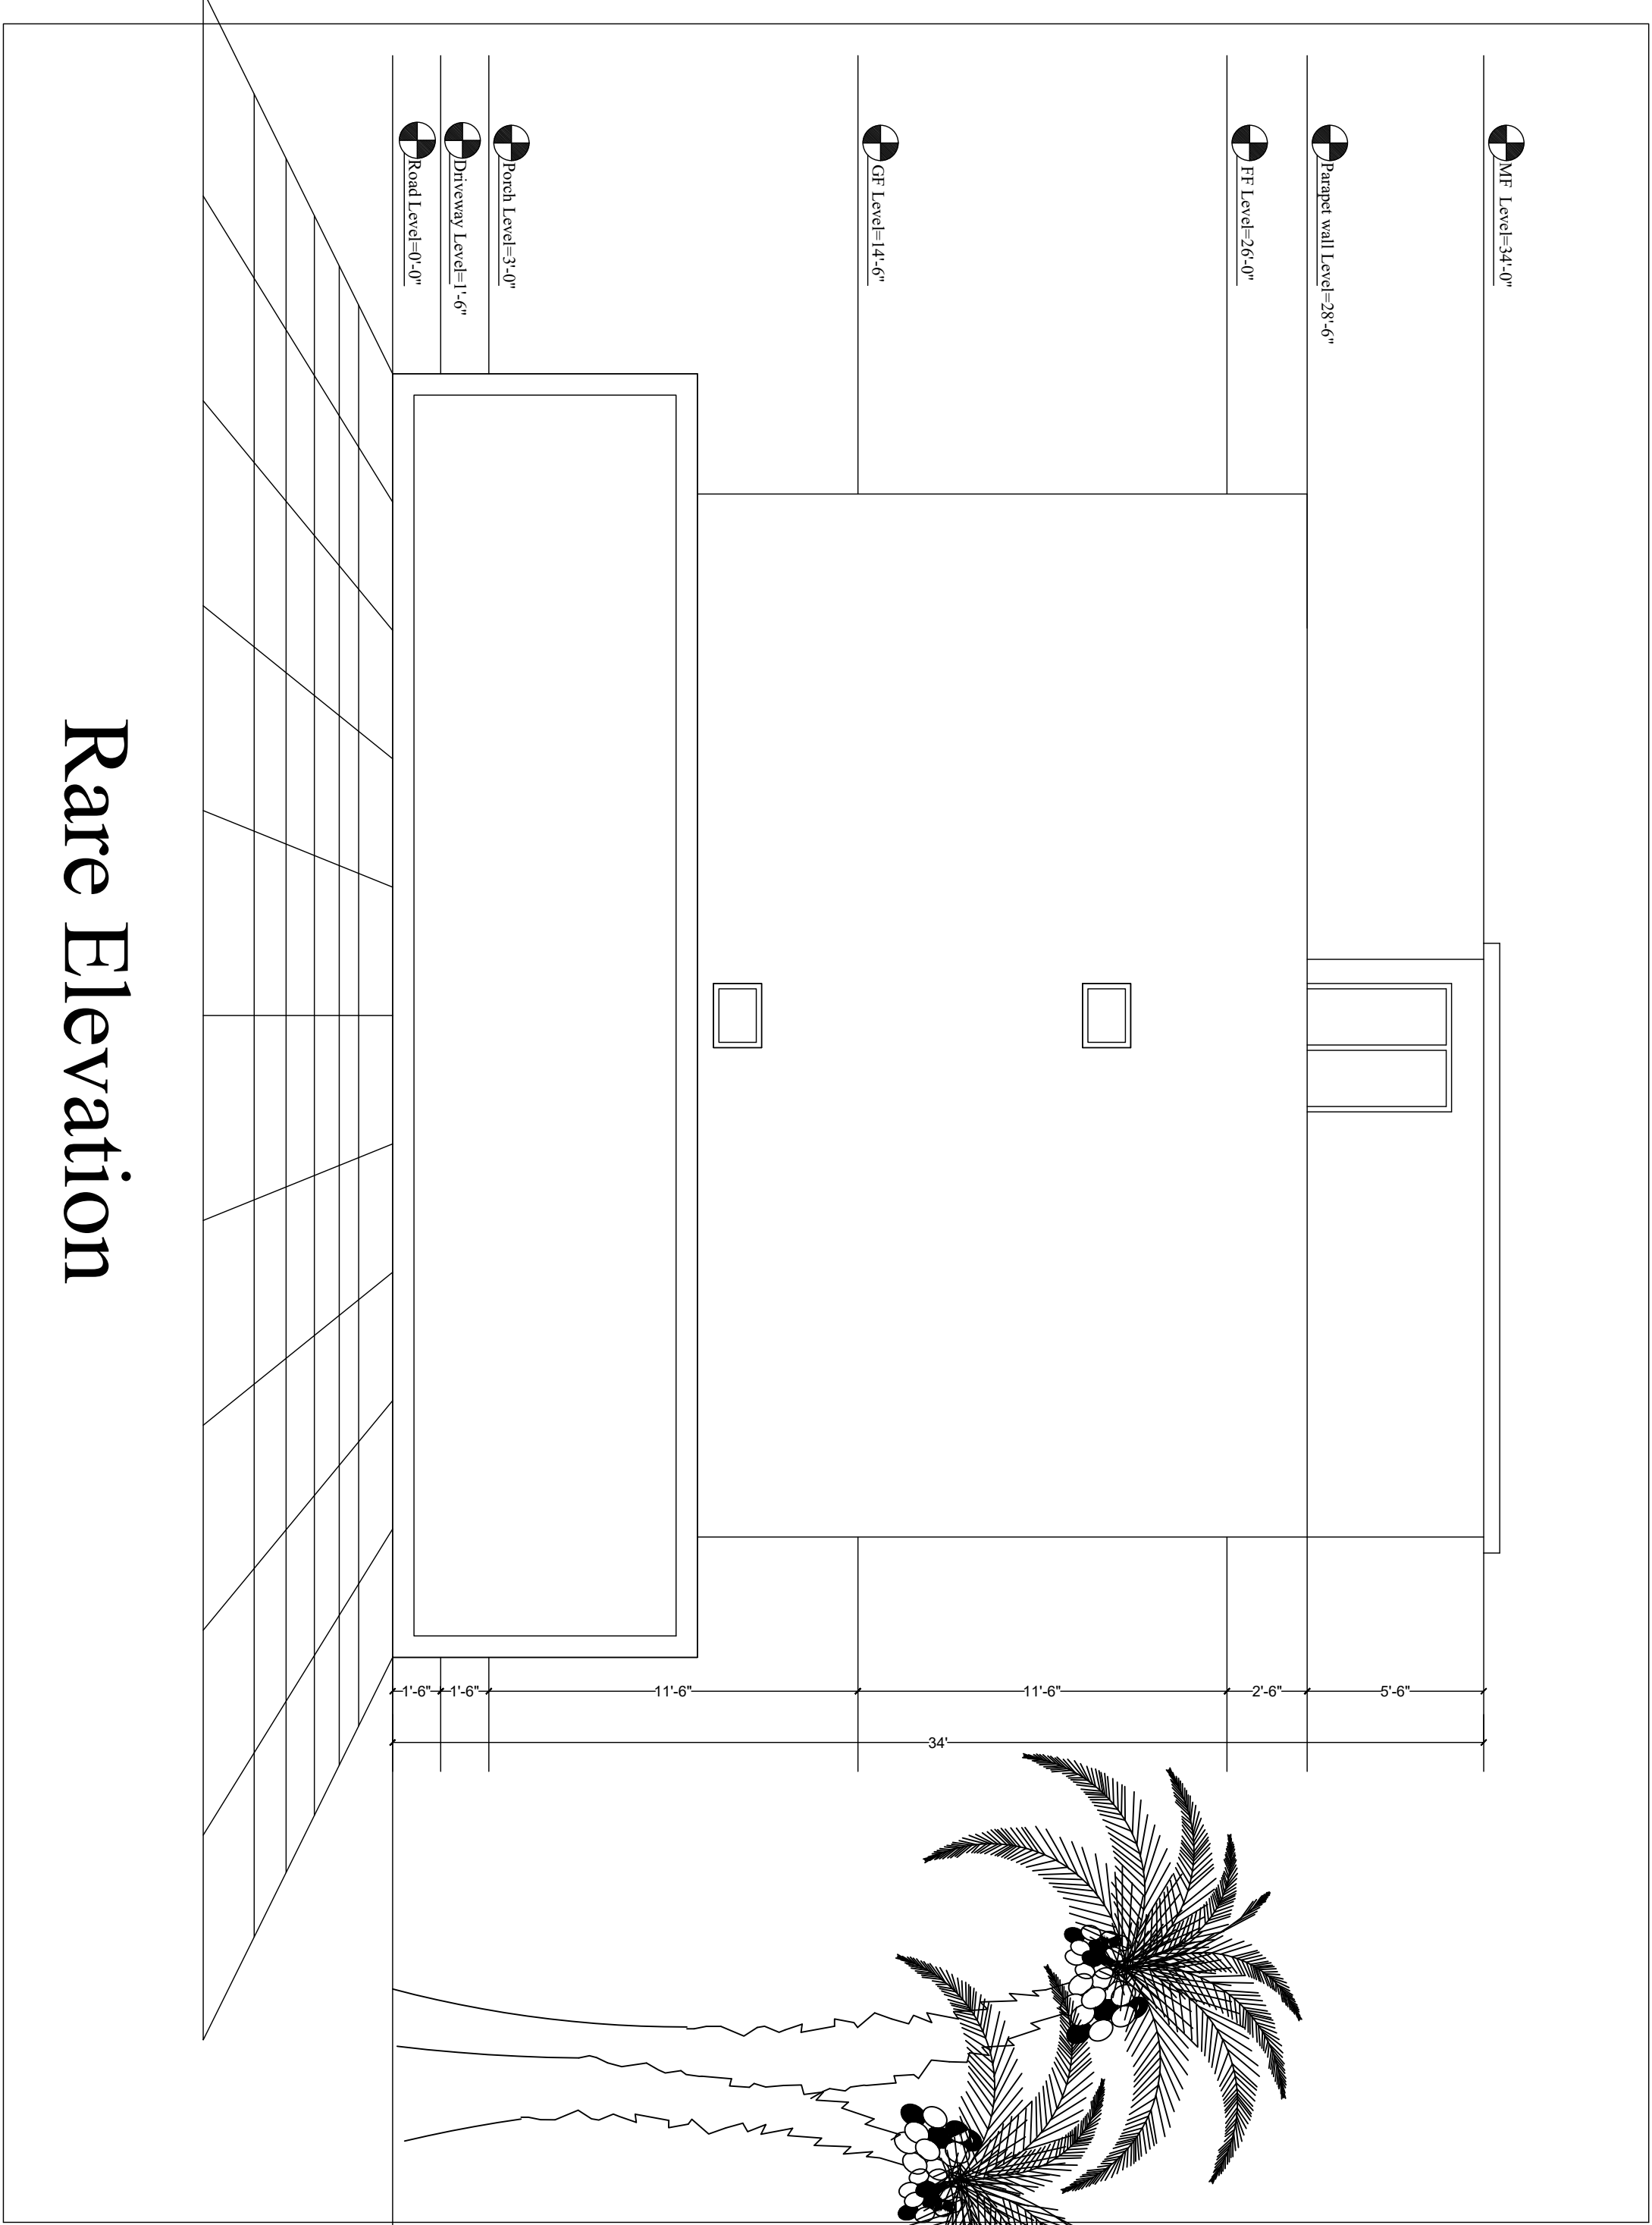

Project: Residential		Drawing:	Drawing Code:	Design By Wajid Khan: 0342-2421701
			S.No:	

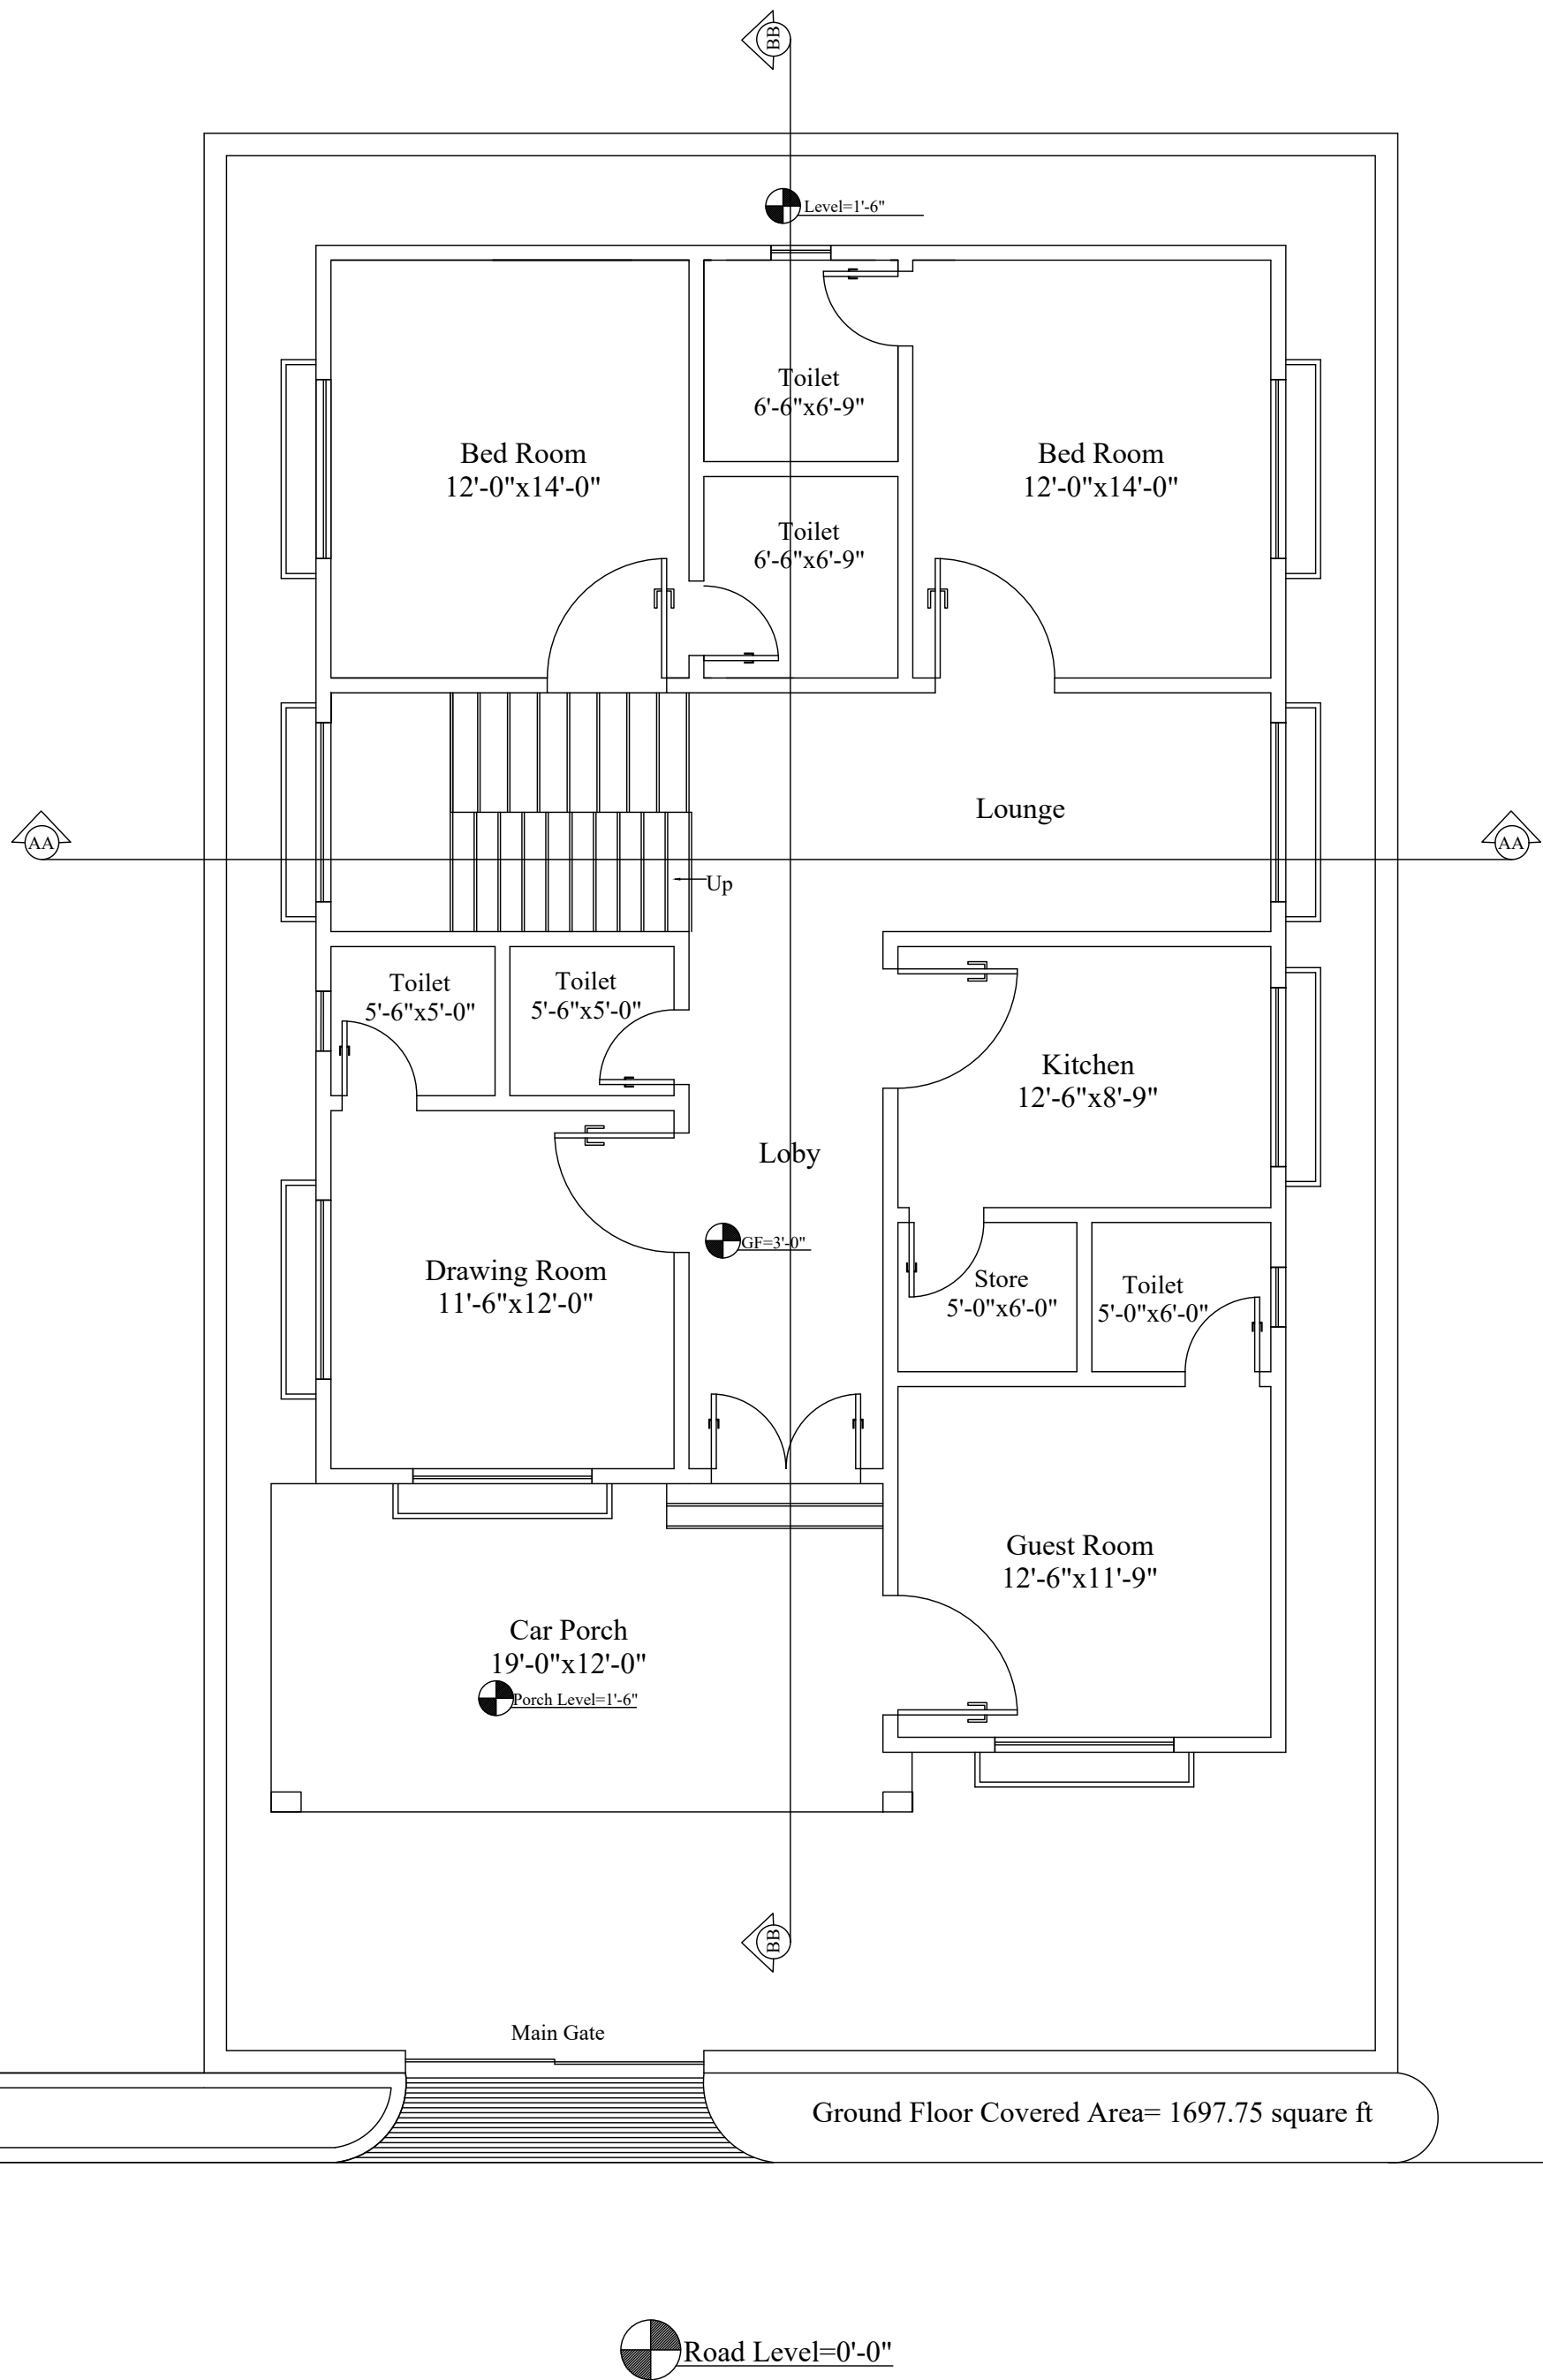


Ground Floor Covered Area= 1697.75 square ft

Project:
Residential


Drawing:


Drawing Code:
S.No:

Design By
Wajid Khan: 0342-2421701

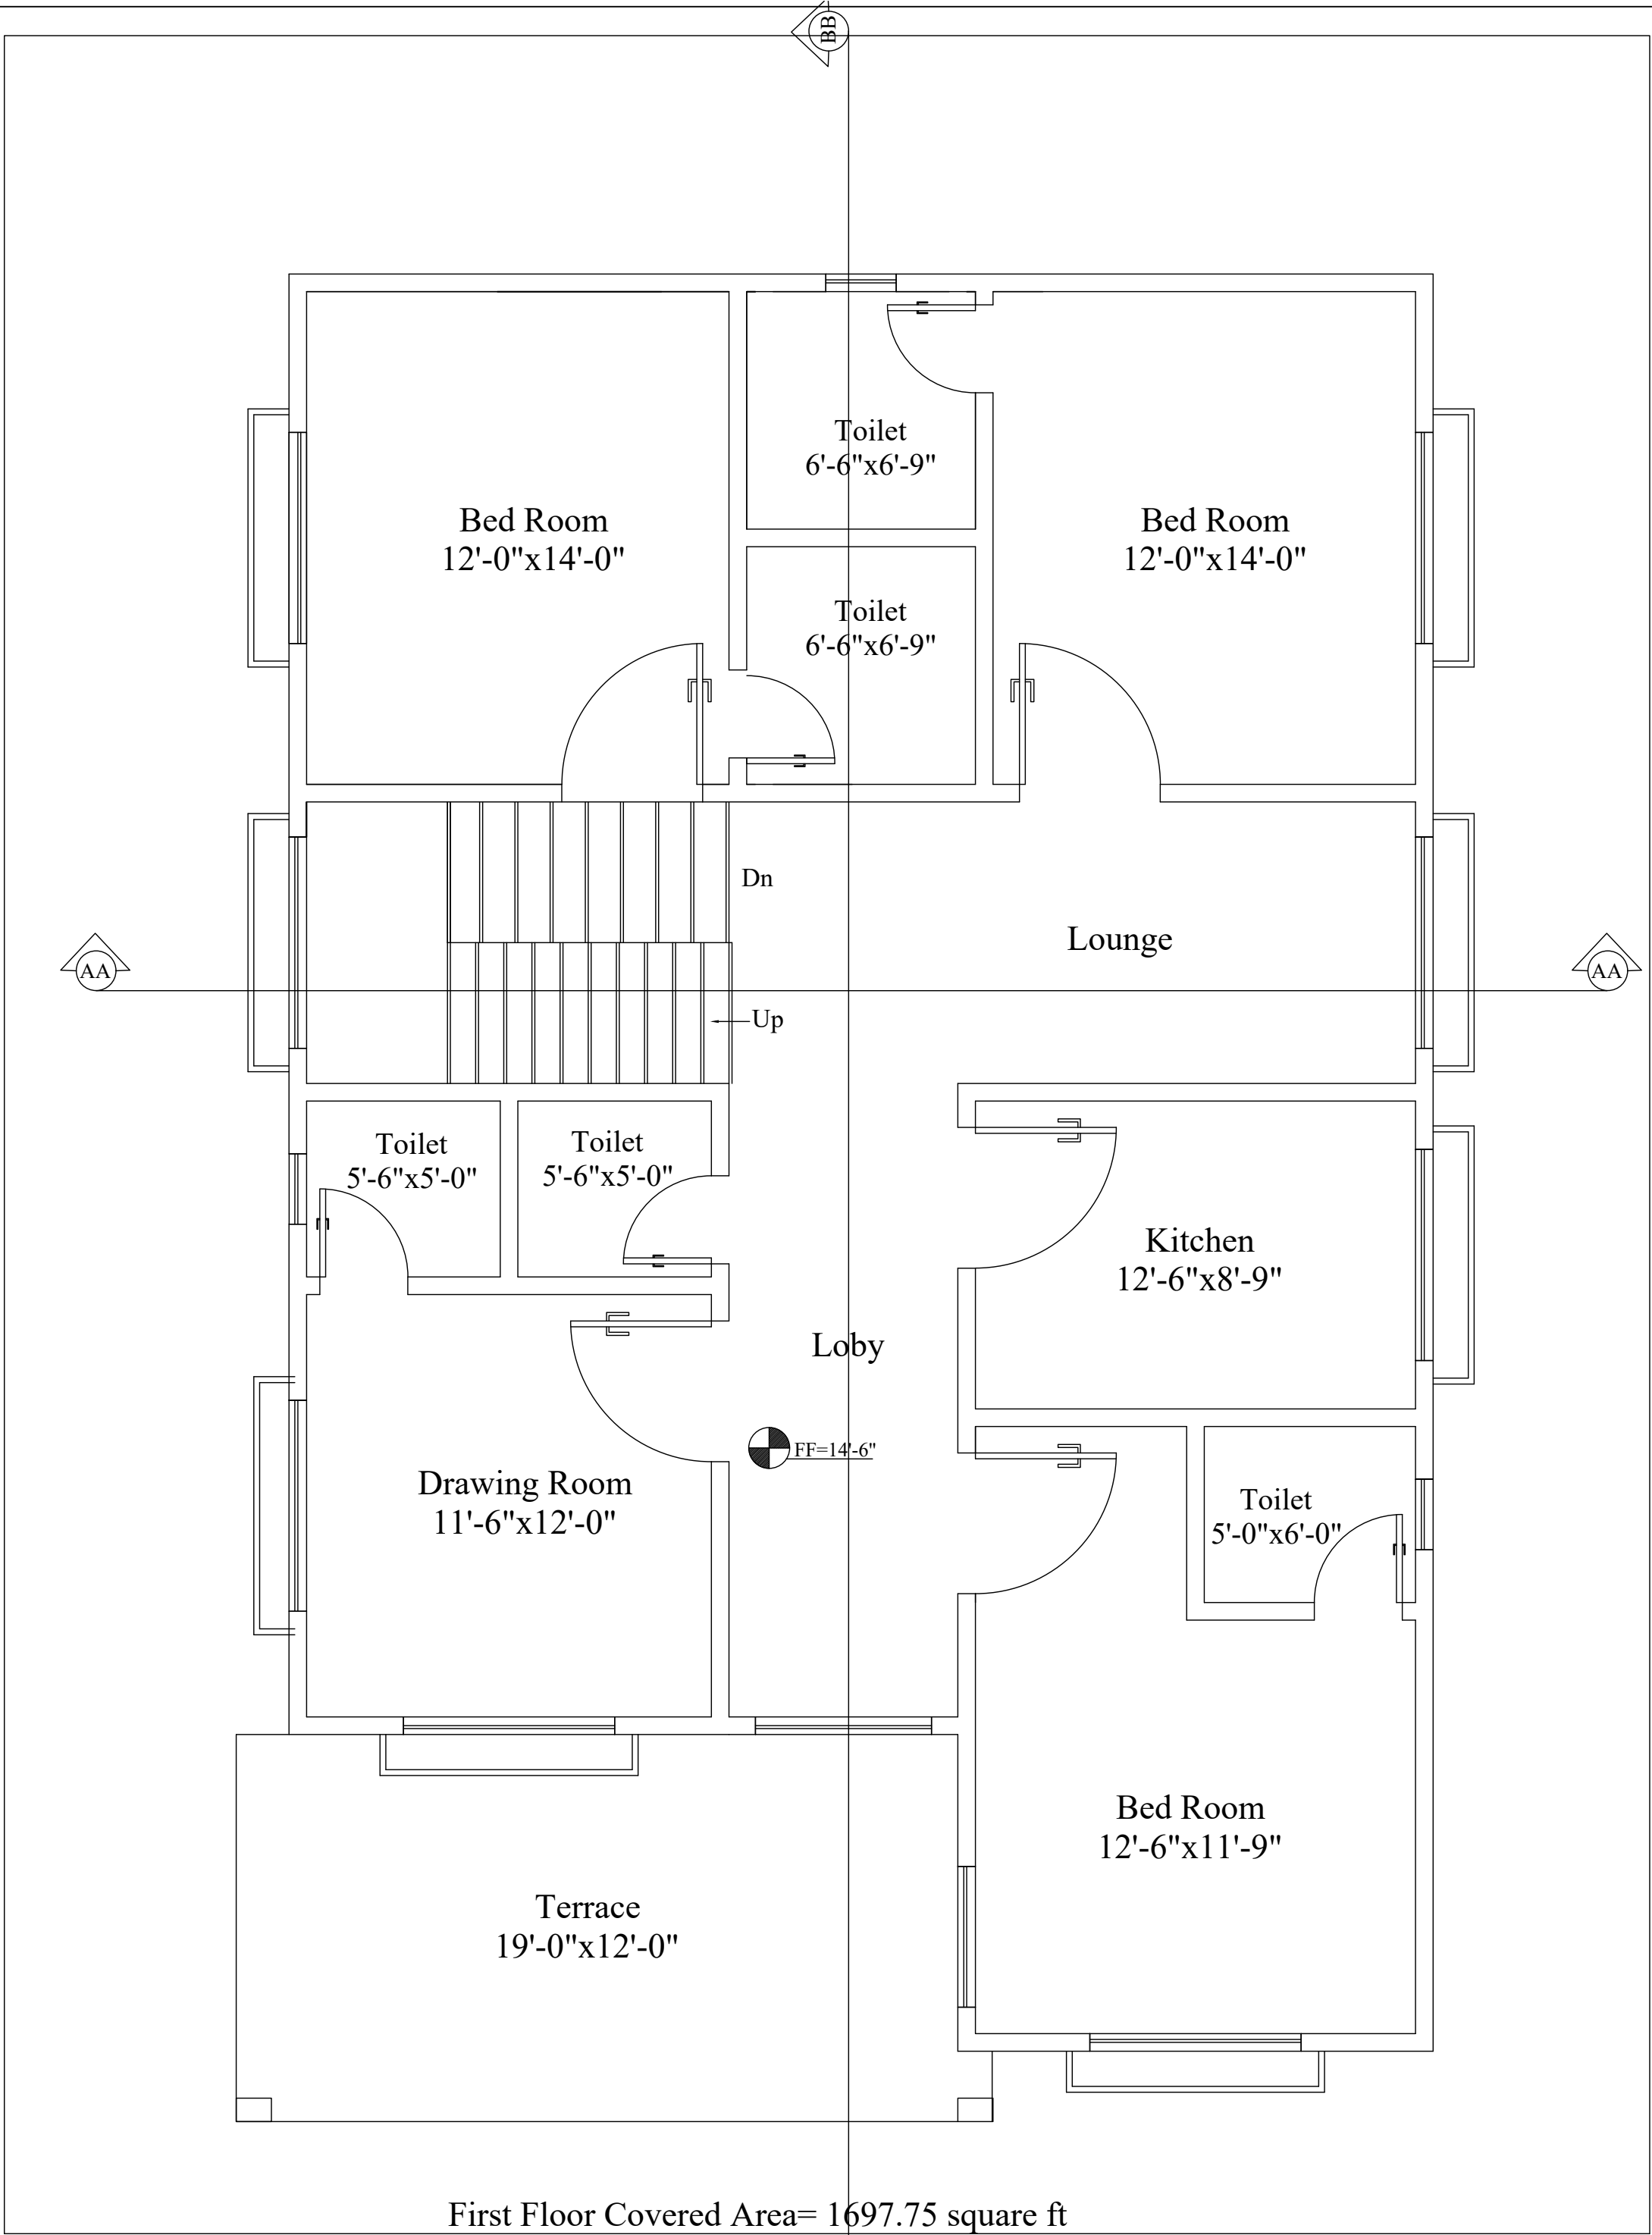

Project: Residential	Drawing:	Drawing Code:	Design By Wajid Khan: 0342-2421701
		S.No:	

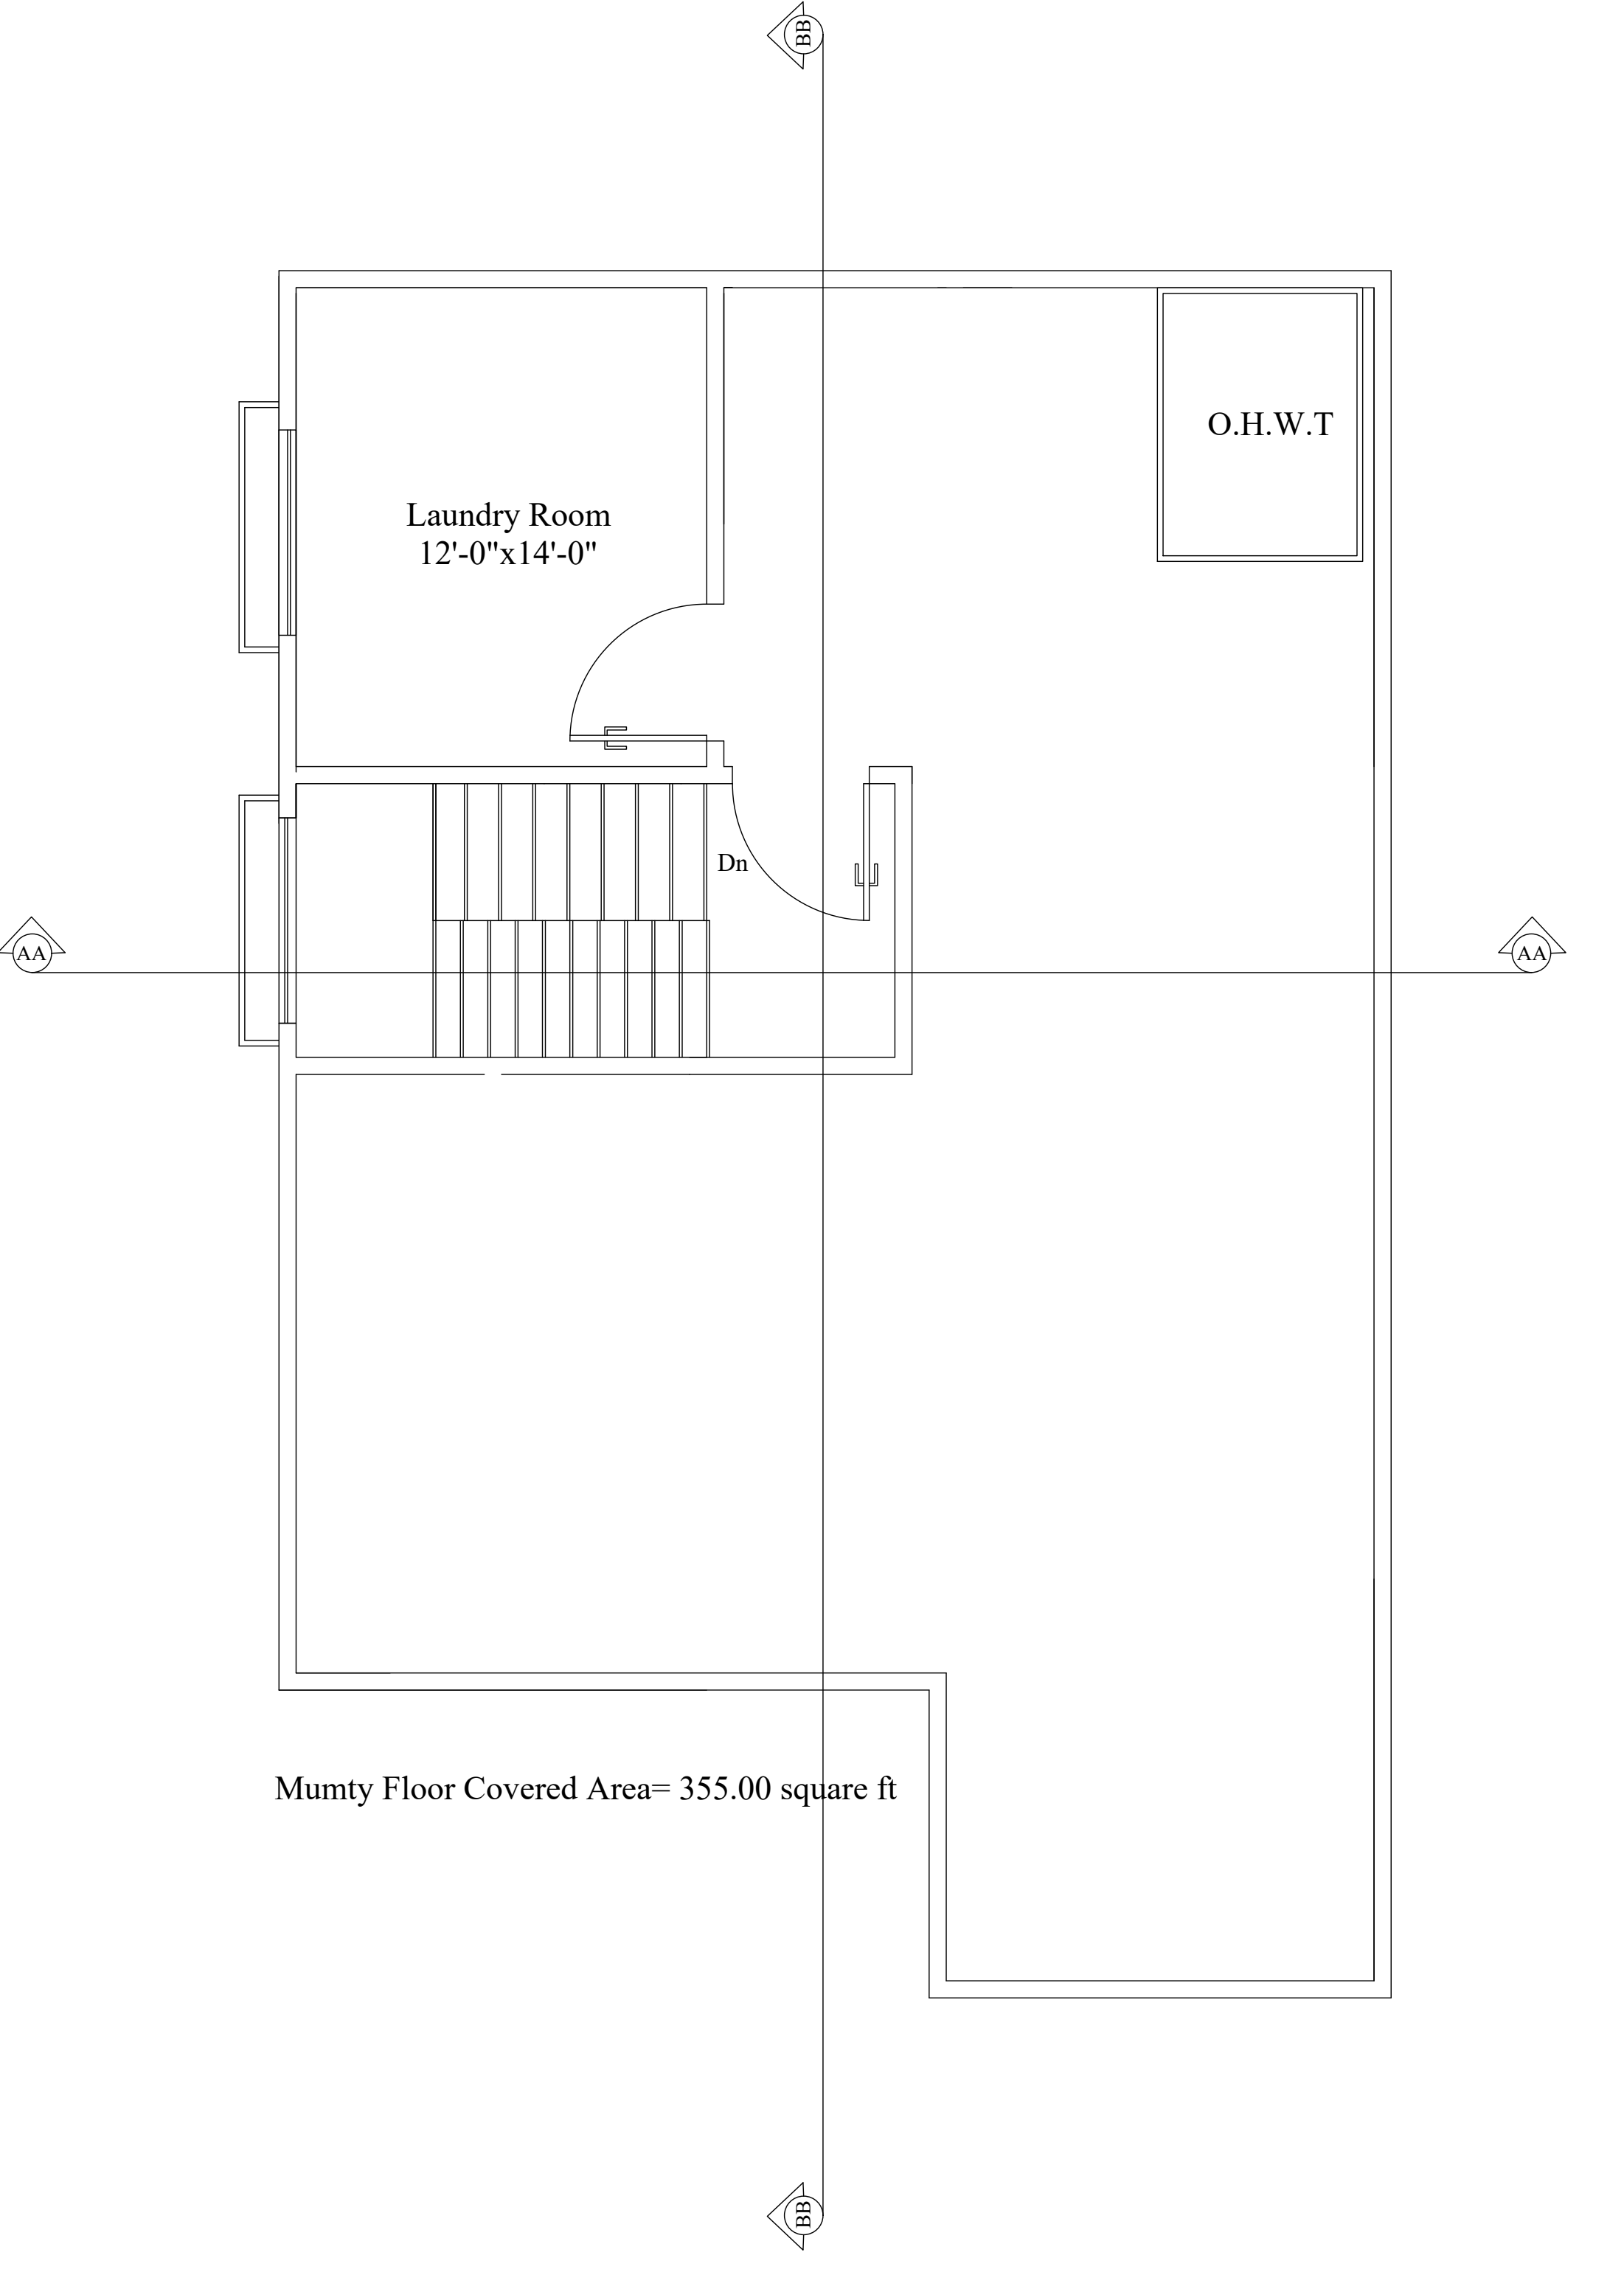

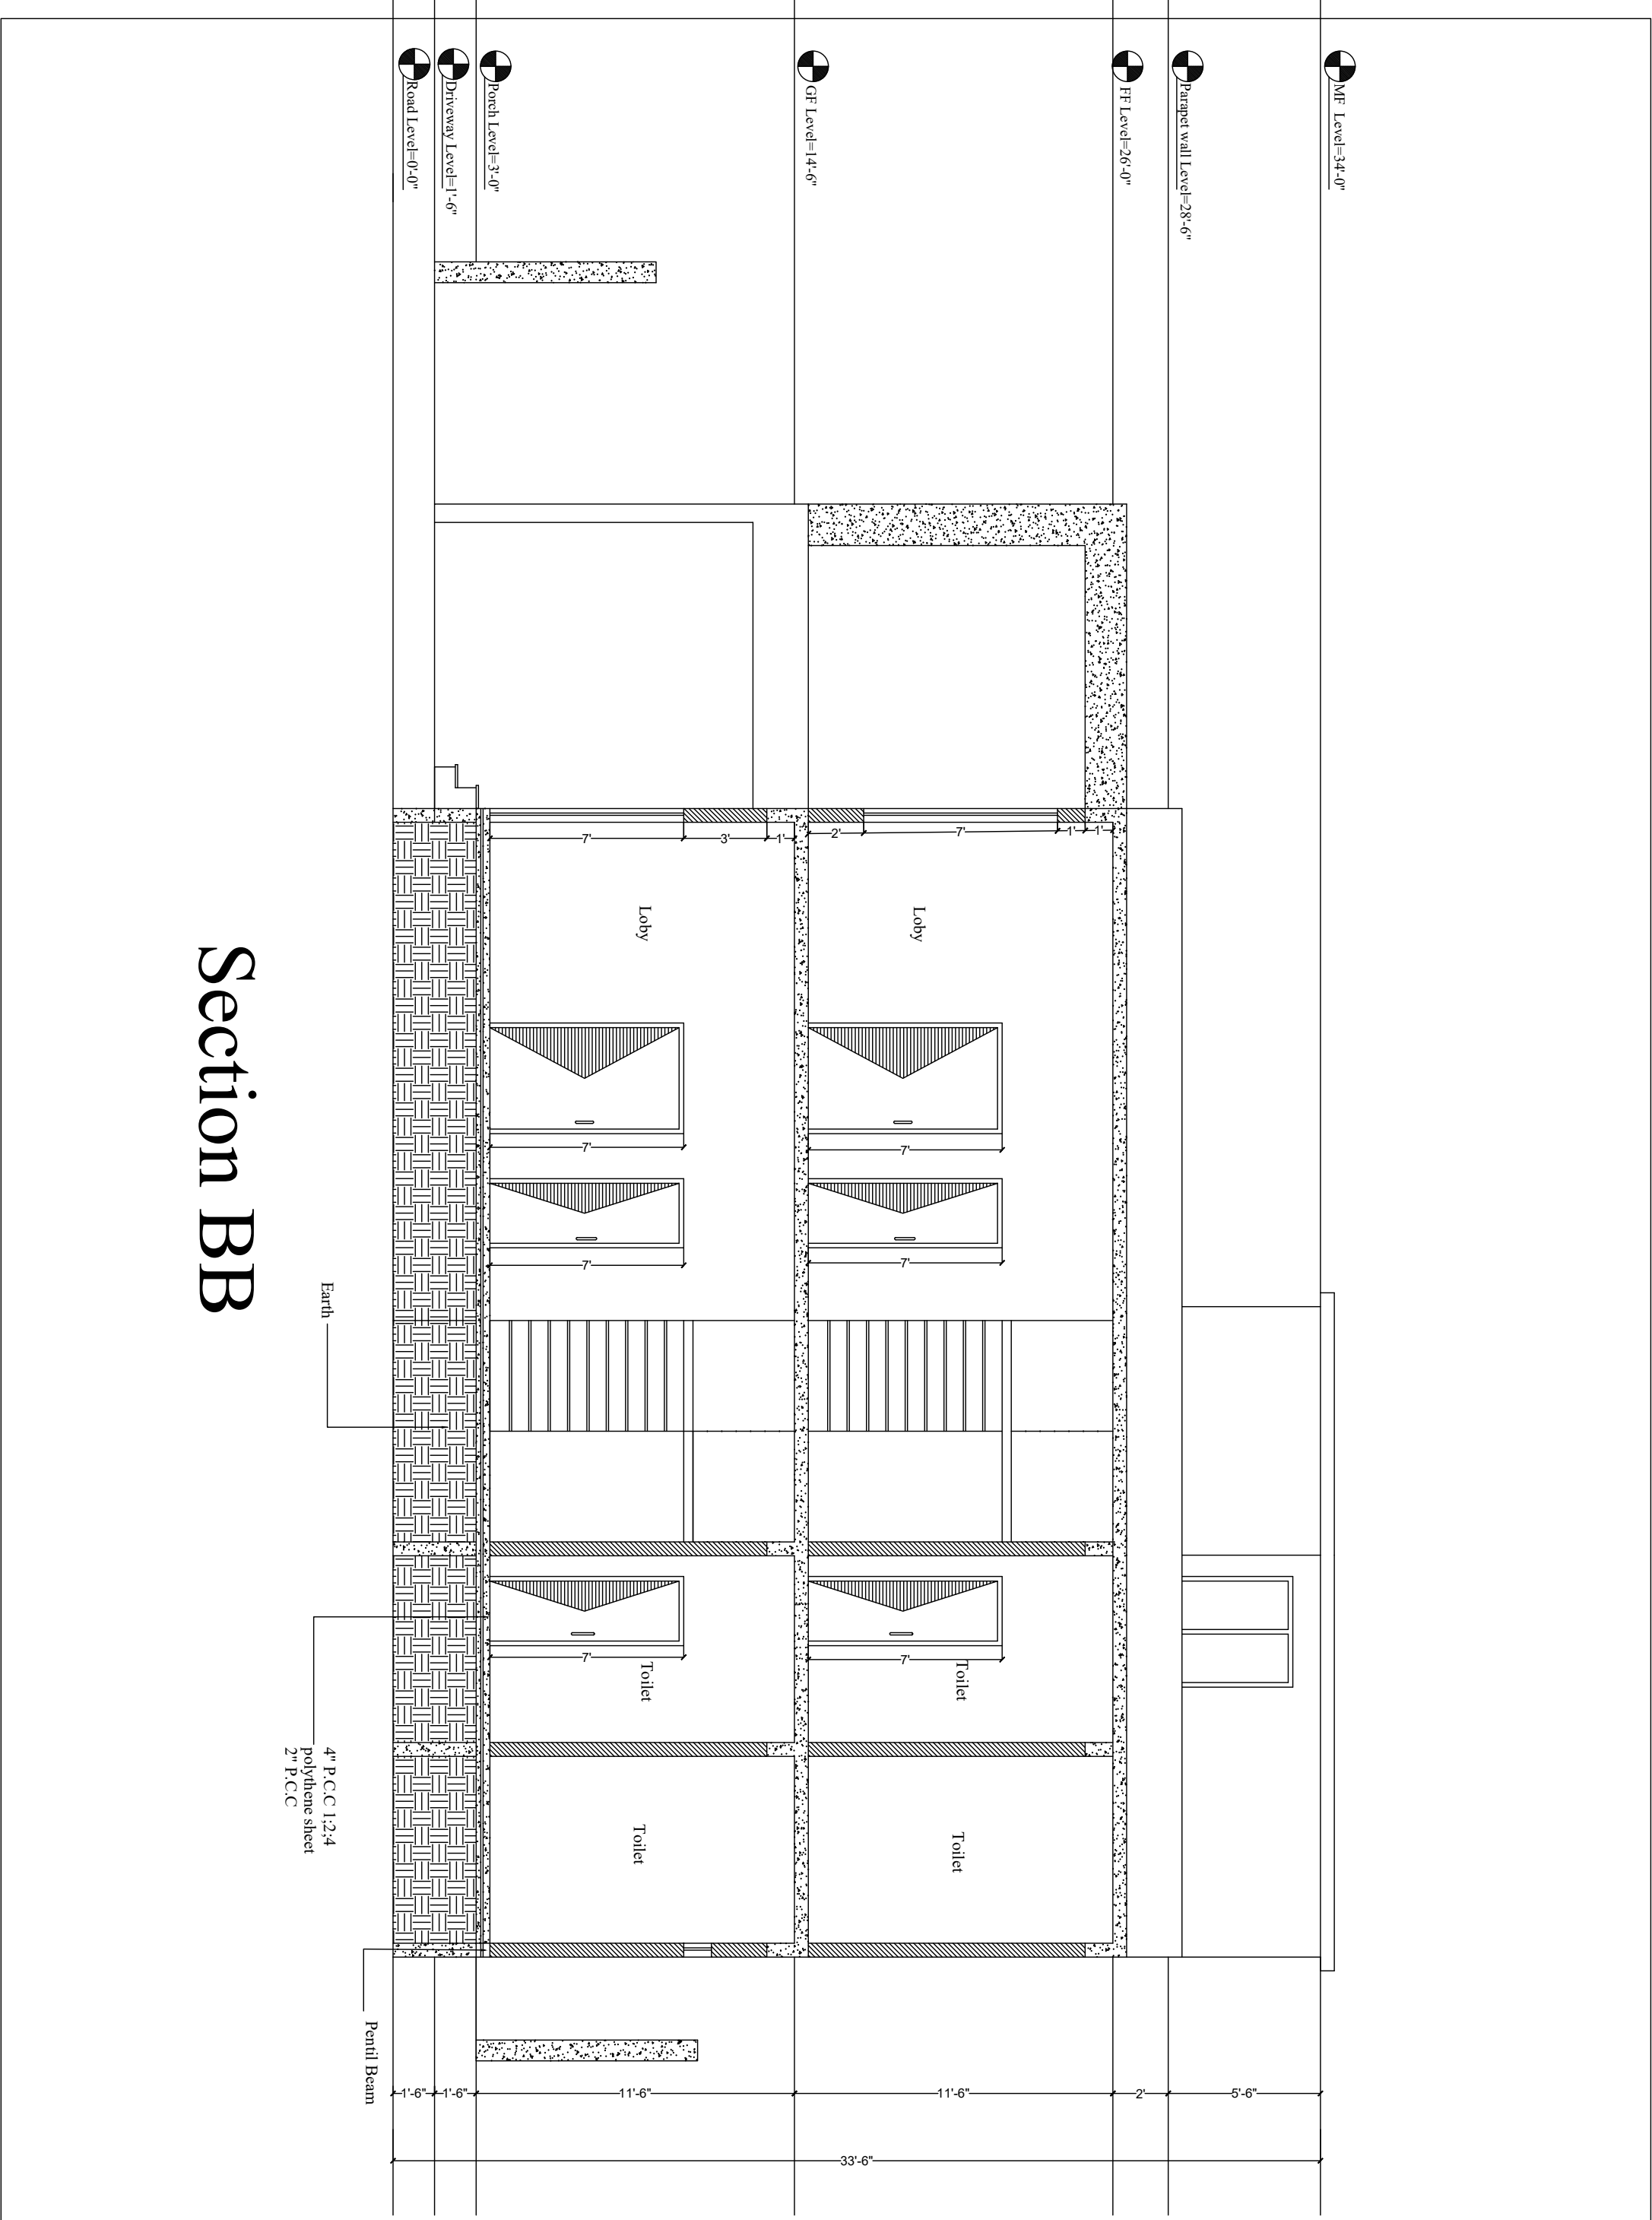

Section BB

Project: Residential	Drawing:	Drawing Code:	Design By Wajid Khan: 0342-2421701
		S.No:	

Electrification


LEGEND

SYMBOL	DESCRIPTION	INSTALLATION HIEGHT
	RECESSED DOWN LIGHTWITH 11 WATT ENERGY SAVER	SLAB MOUNTED
	HANGING LIGHT WITH 17 WATT ENERGY SAVER	SLAB MOUNTED
	SURFACE MOUNTED DOWN LIGHT WITH 13 WATT ENERGY SAVER	SLAB MOUNTED
	RECESSED 7 WATT SPOT LIGHT	SLAB MOUNTED
	OUT DOOR WALL BRACKET LIGHT WITH 23 WATT ENERGY SAVER	8' FROM F.F.L
	CHANDELIER	REF TO ARCHITECTURE
	TMS 118	REF TO ARCHITECTURE
	56" SWEEP CEILING FAN	SLAB MOUNTED
	12"PLASTIC BODY EXHAUST FAN DOUBLE ACTION	REF TO ARCHITECTURE
	SWITCH BOARD	42" FROM F.F.L
	1.5 TON SPLIT A.C	8.5' FROM F.FL
	DOUBLE WALL BRACKET	8' FROM F.FL
	SINGLE WALL BRACKET	8' FROM F.FL
	DISTRIBUTION UNIT	4' FROM F.F.L
	TELEPHONE JUNCTION BOX	4' FROM F.F.L
	TV JUNCTION BOX	4' FROM F.F.L
	10AMP INTERNATIONAL SWITCH SOCKET	12" FROM F.F.L
	TV OUTLET	12" FROM F.FL
	TELEPHONE OUTLET	12" FROM F.FL
	LED 56"	REF TO ARCHITECTURE
	SINGLE GANG SWITCH	
	DOUBLE GANG SWITCH	
	5A, 220V, 2-PIN+E SWITCH-SOCKET UNIT+15A 3-PIN SWITCH SOCKET UNIT	0'-8"-0" F.F.L
	POWER PLUG	1'-6"-0" F.F.L

GENERAL NOTES:

- 01- ALL WIRING OF LIGHTING AND POWER SHALL BE WITH SINGLE CORE PVC INSULATED WIRES FOR SINGLE PHASE CIRCUIT. THE VOLTAGE GRADE OF WIRE SHALL BE 450/750V, WHERE AS FOR THREE PHASE CIRCUIT IT WILL BE 600/1000 VOLTS.
- 02- CIRCUIT WIRING SHALL BE WITH THE FOLLOWING SIZE OF WIRES UNLESS OTHERWISE INDICATED.
- a) DB TO SWITCH BOARD / 1ST LIGHT----- 2x2.5 sq.mm + ECC 1x2.5 sq.mm
 - b) SWITCH BOARD TO LIGHT POINT----- 1x1.5 sq.mm + ECC 1x2.5 sq.mm AS NEUTRAL COMMON FOR ALL LIGHTS FIXTURE ON ONE CIRCUIT.
 - c) 5A 2&3 PIN SWITCH SOCKET UNIT ----- 2 x 2.5sq.mm + ECC 1x2.5sq.mm
 - d) 13A 3-PIN SWITCH SOCKET UNIT ----- 2 x 4 sq.mm + ECC 1 x 4 sq.mm FOR COMPUTER POWER
- 03- CONDUIT UNDER FLOOR SHALL HAVE A MINIMUM DEPTH OF 25mm MEASURED FROM FINISH FLOOR LEVEL TO TOP OF CONDUIT.
- 04- MINIMUM SIZE OF CONDUIT SHALL BE 20mm Ø, UNLESS OTHERWISE INDICATED.
- 05- THE ELECTRICAL RESISTANCE OF ECC TOGETHER WITH EARTH LEAD AND ELECTRODE SHALL NOT EXCEED ONE OHM. THE CONTRACTOR SHALL OBTAIN INSTRUCTIONS FROM CONSULTANT FOR ANY RECTIFICATION.
- 06- BACK BOXES FOR SWITCHES, SOCKETS AND TELEPHONE ETC. SHALL BE MADE WITH 16SWG SHEET STEEL.
- 07- WIRE AS ECC SHALL BE GREEN OR GREEN/YELLOW IN COLOR.
- 08- RUNNING LENGTHS SHOWN IN B.O.Q ARE NOT EXACT CONTRACTOR SHALL HAVE TO TAKE MEASUREMENTS BEFORE PURCHASING THE MATERIAL.
- 09- CONDUIT AND CABLES TO BE LAID UNDER FLOOR SHALL BE IN COORDINATION WITH OTHERS SERVICES.
- 10- FOR TELEPHONE WIRING, CAT-V CABLE SHOULD BE USED .
- 11- FOR DATA NETWORKING CAT-VI CABLE SHOULD BE USED .
- 12- WIRING FOR CCTV SYSTEM SHALL BE RG-6 COAXIAL CABLE
- 13- WIRING FOR FIRE ALARM SYSTEM SHALL BE 2C,1.5 sq.mm

Project: Residential	Drawing:	Drawing Code:	Design By Wajid Khan: 0342-2421701
		S.No:	

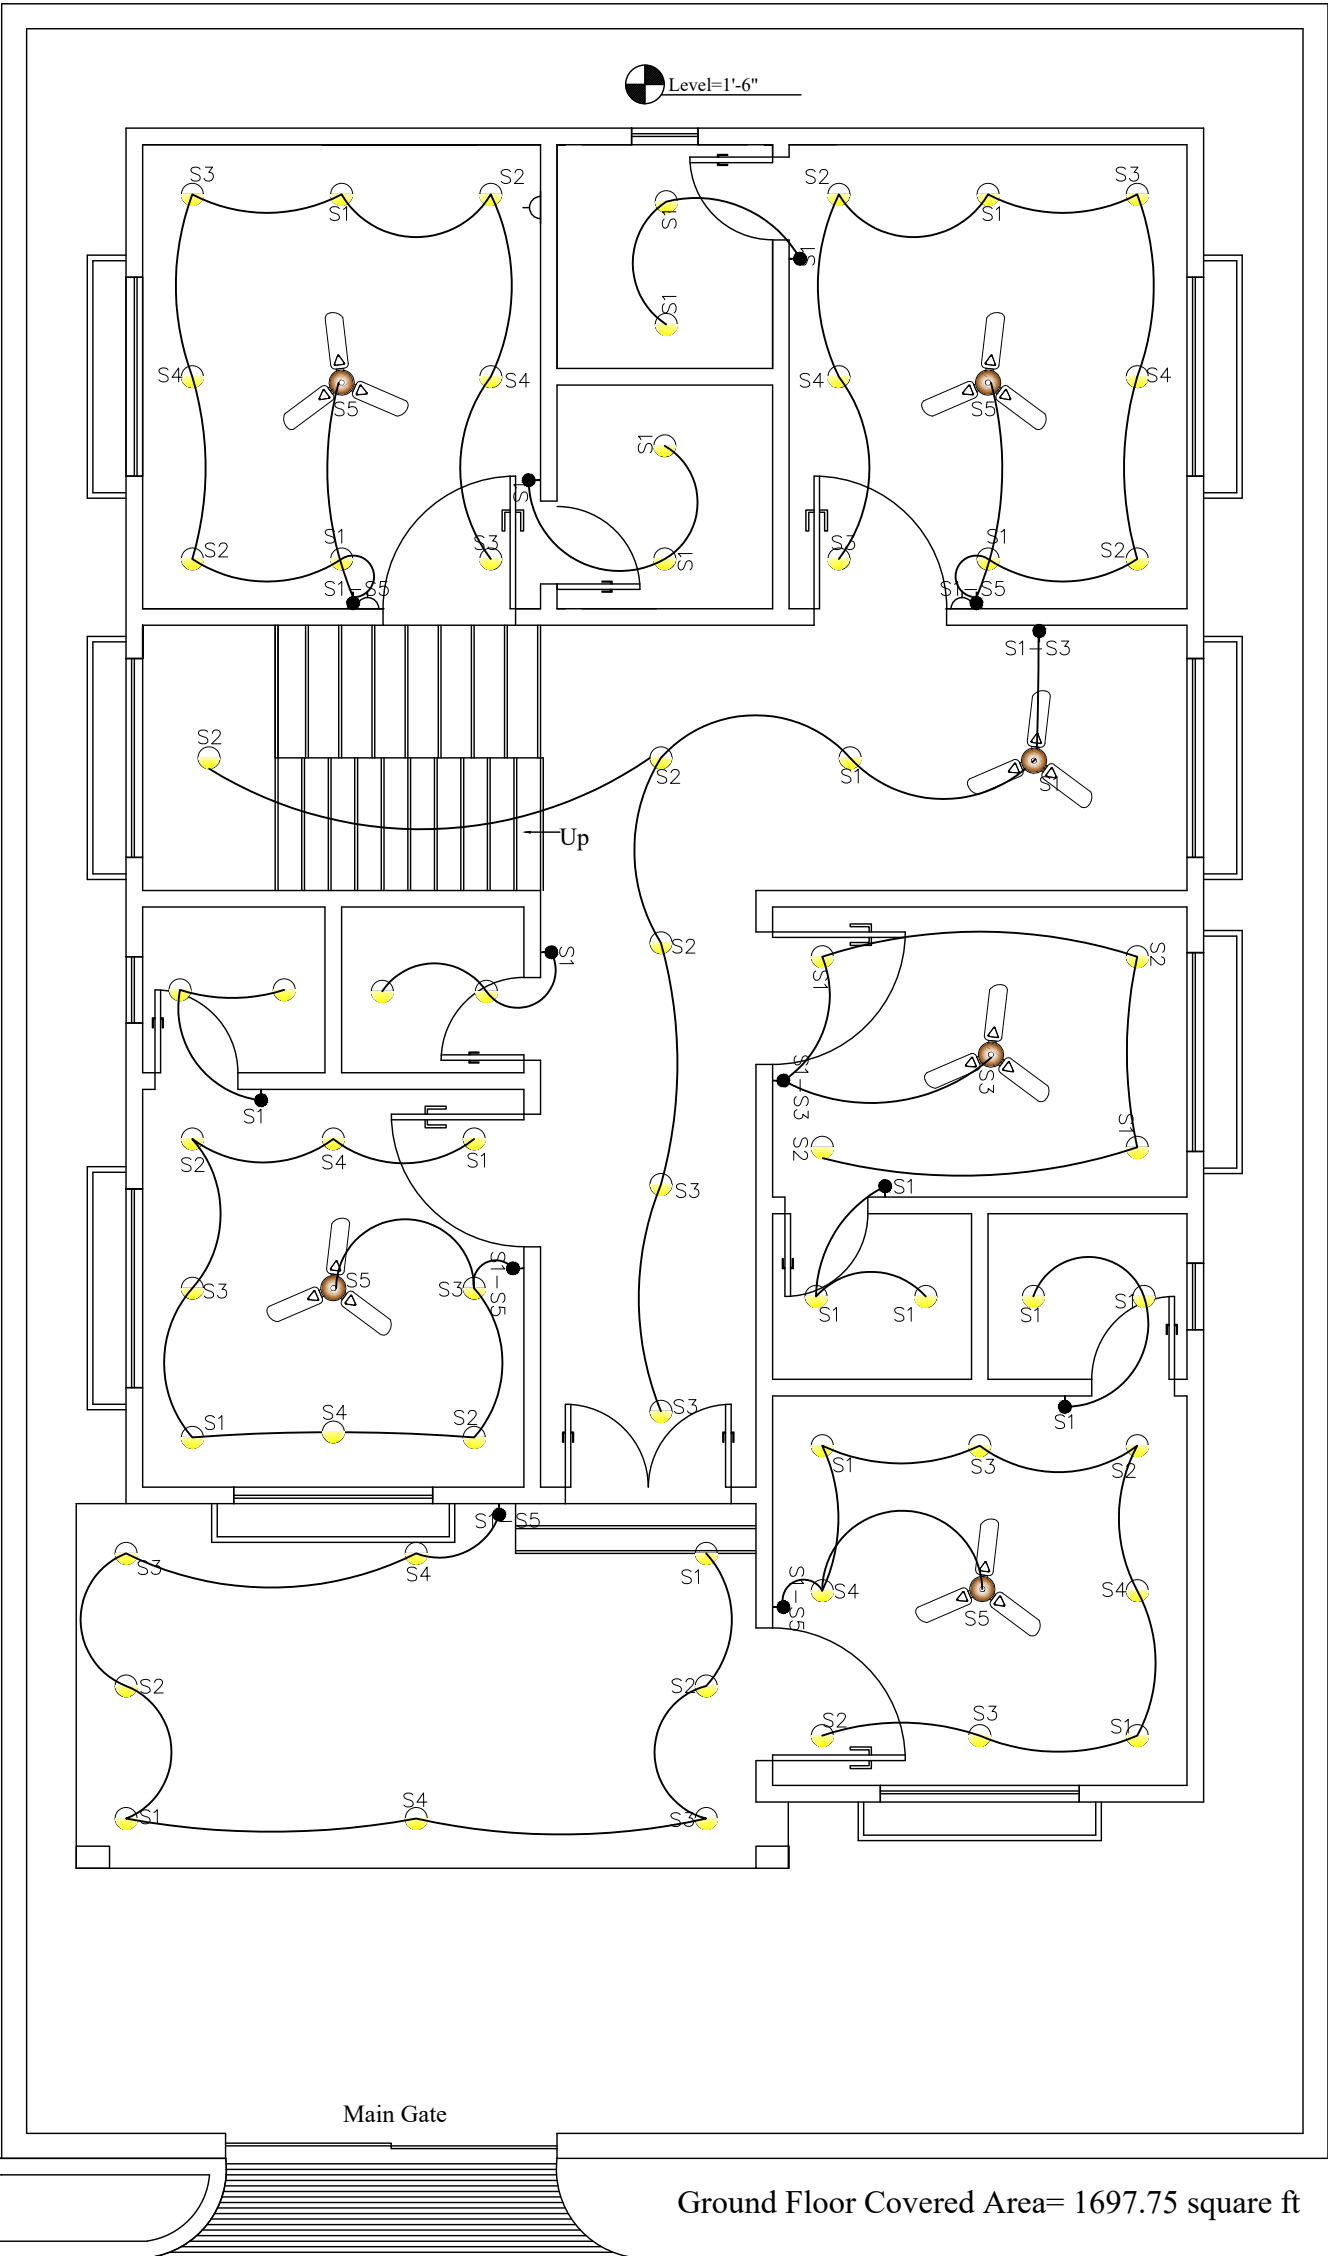


Road Level=0'-0"

Project:
Residential

Drawing:


Drawing Code:
S.No:

Design By
Wajid Khan: 0342-2421701

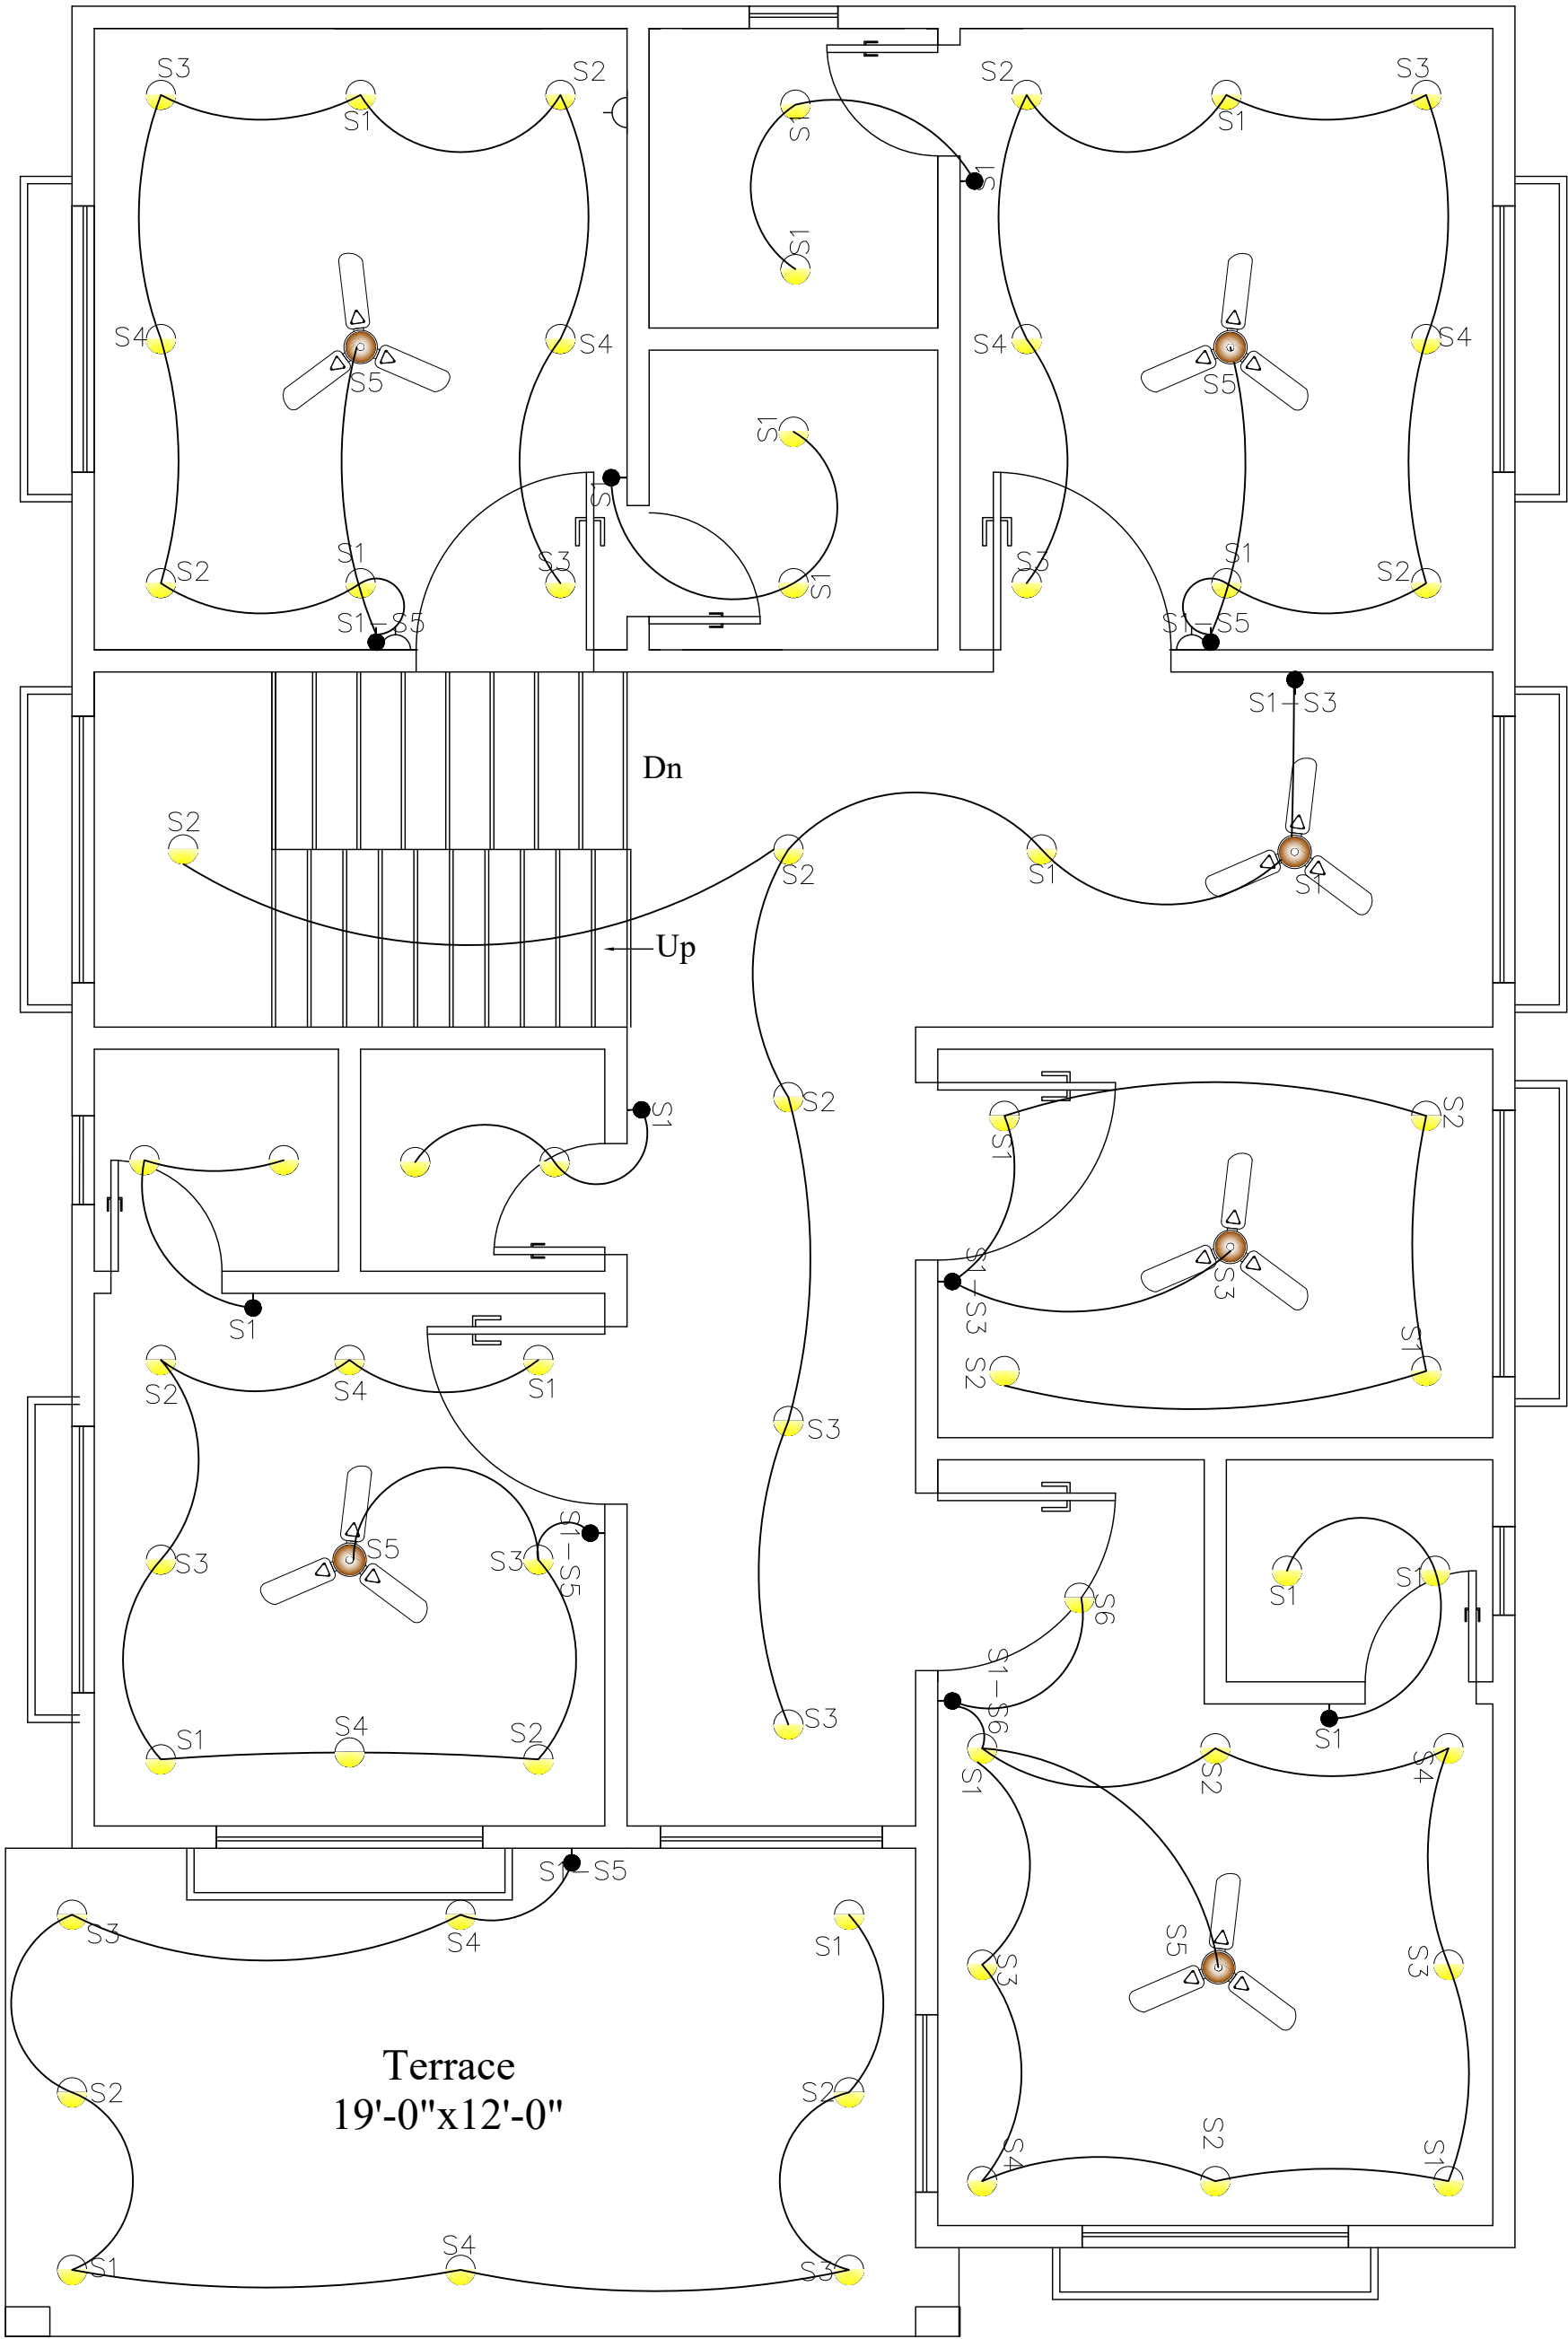


First Floor Covered Area= 1697.75 square ft

Project: Residential	Drawing:	Drawing Code:	Design By Wajid Khan: 0342-2421701
		S.No:	

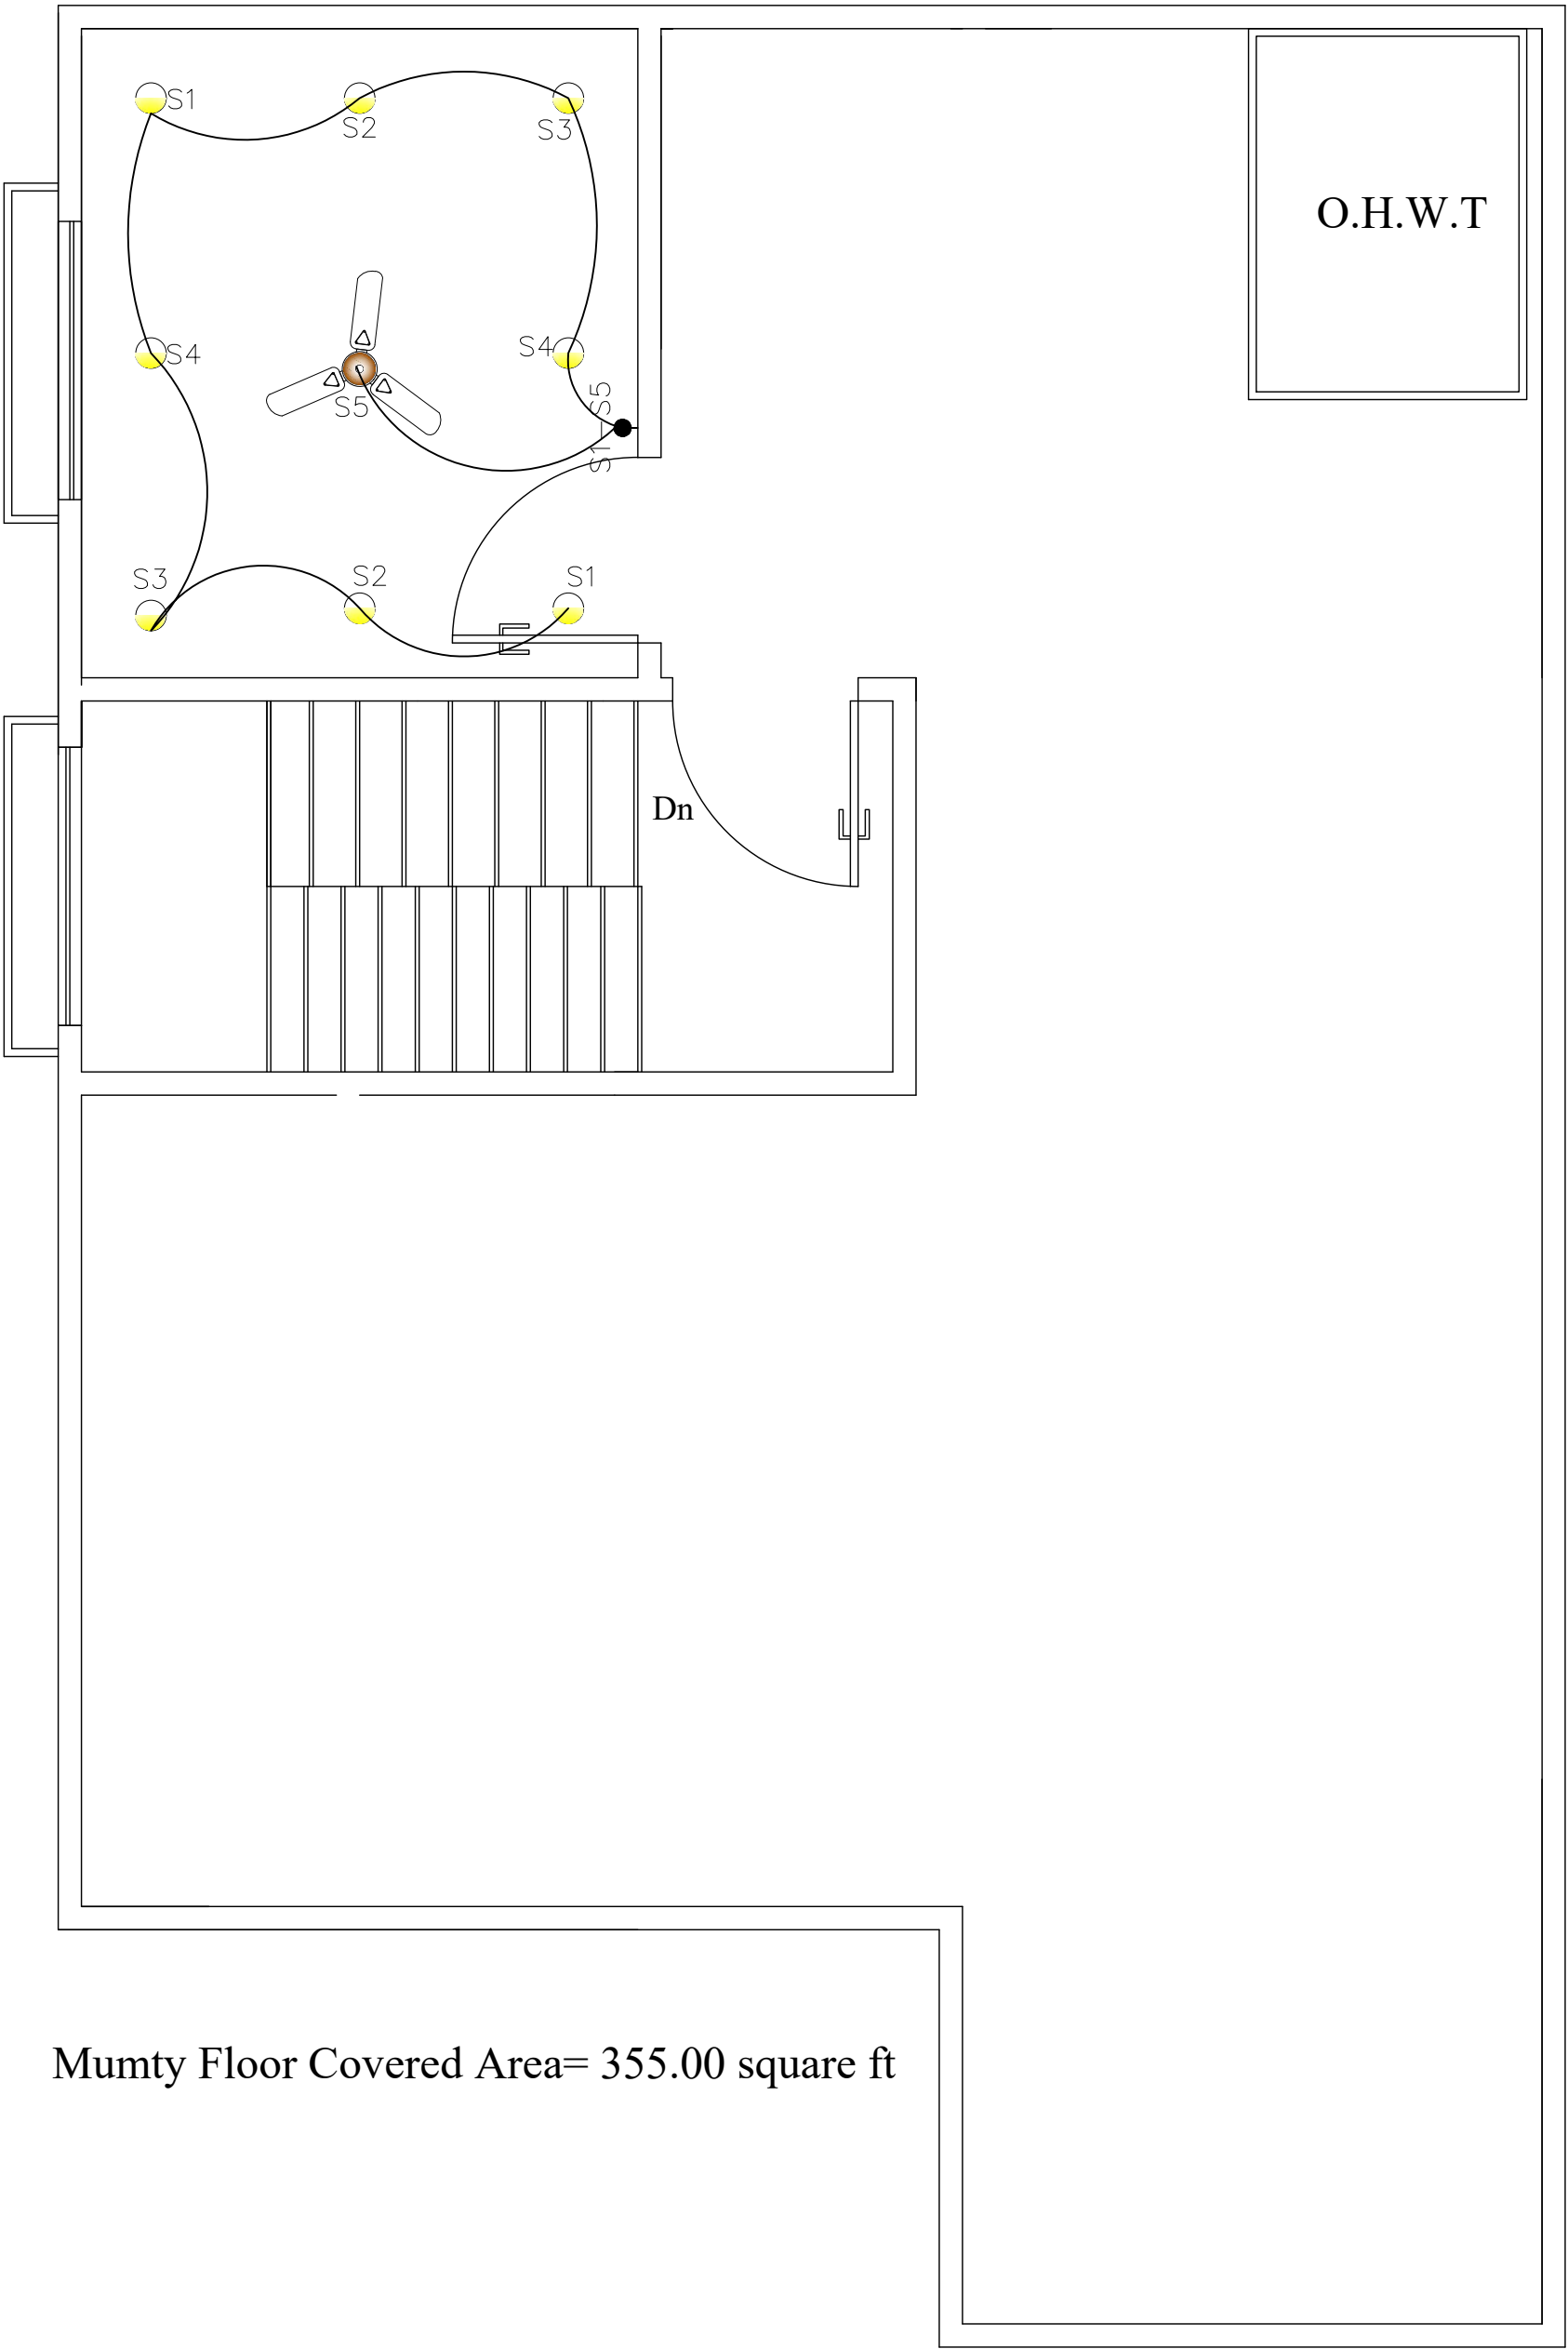


Mumty Floor Covered Area= 355.00 square ft

Project: Residential	Drawing:	Drawing Code:	Design By Wajid Khan: 0342-2421701
		S.No:	

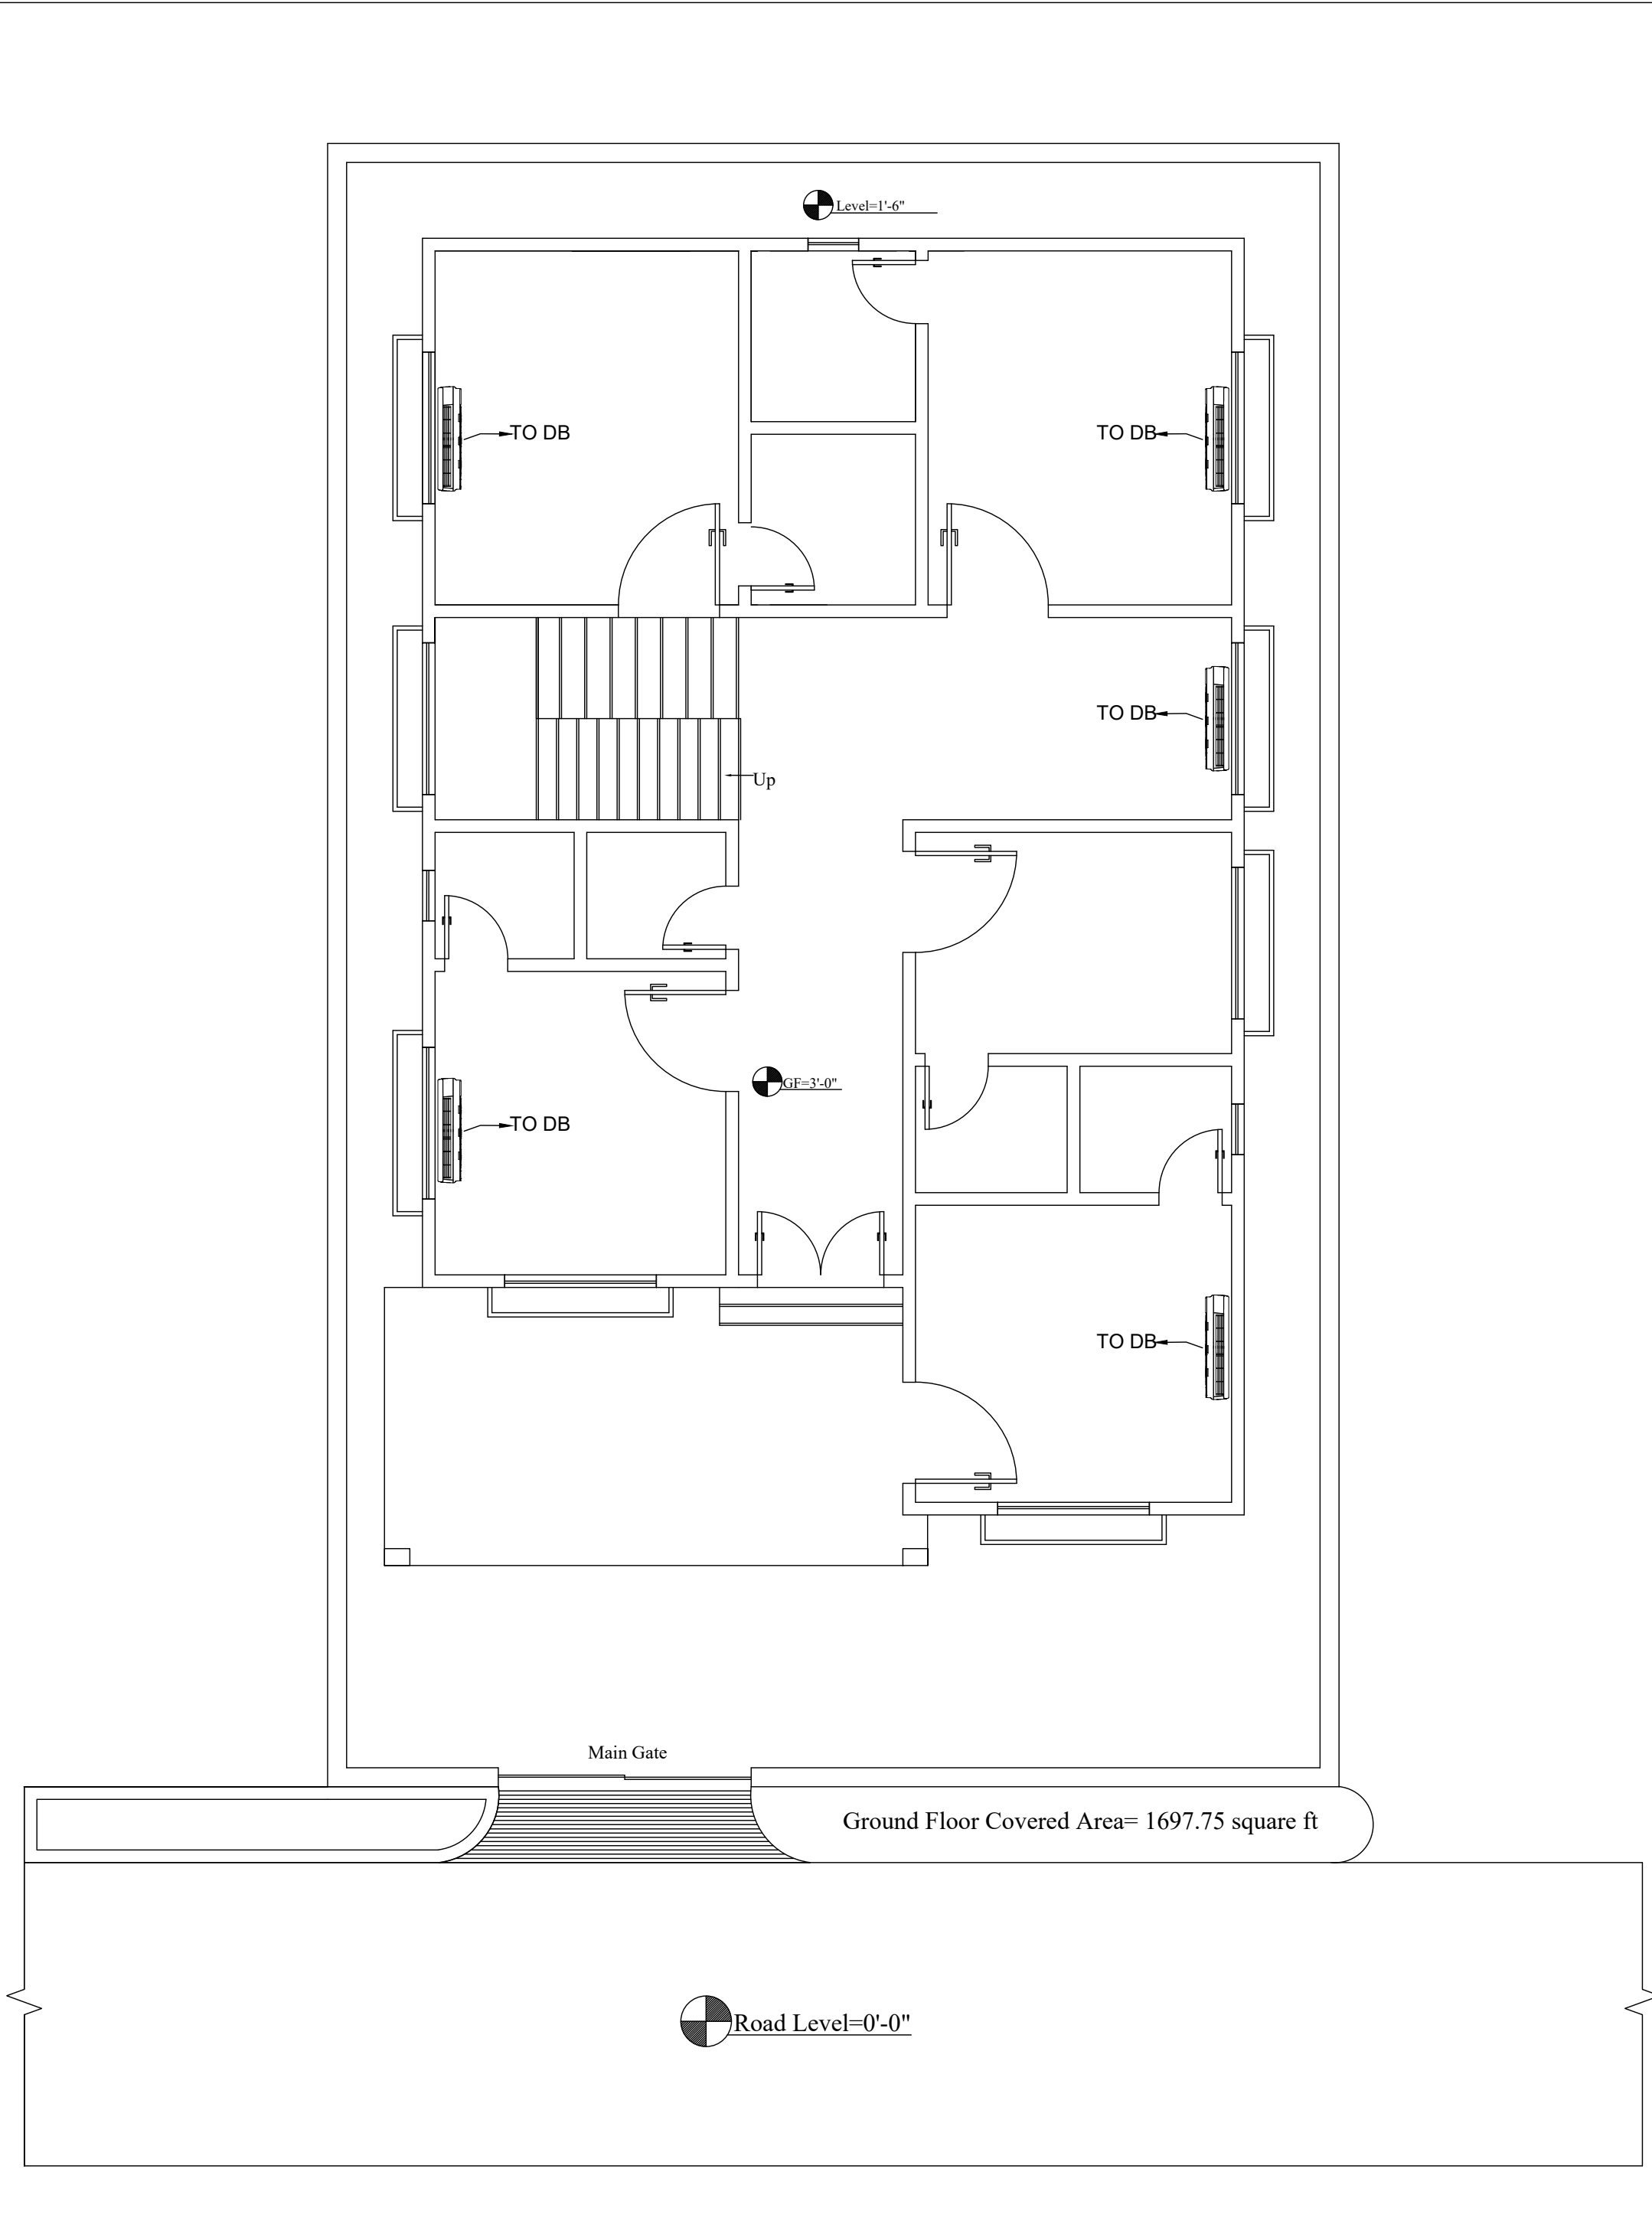


Project: Residential	Drawing:	Drawing Code:	Design By Wajid Khan: 0342-2421701
		S.No:	

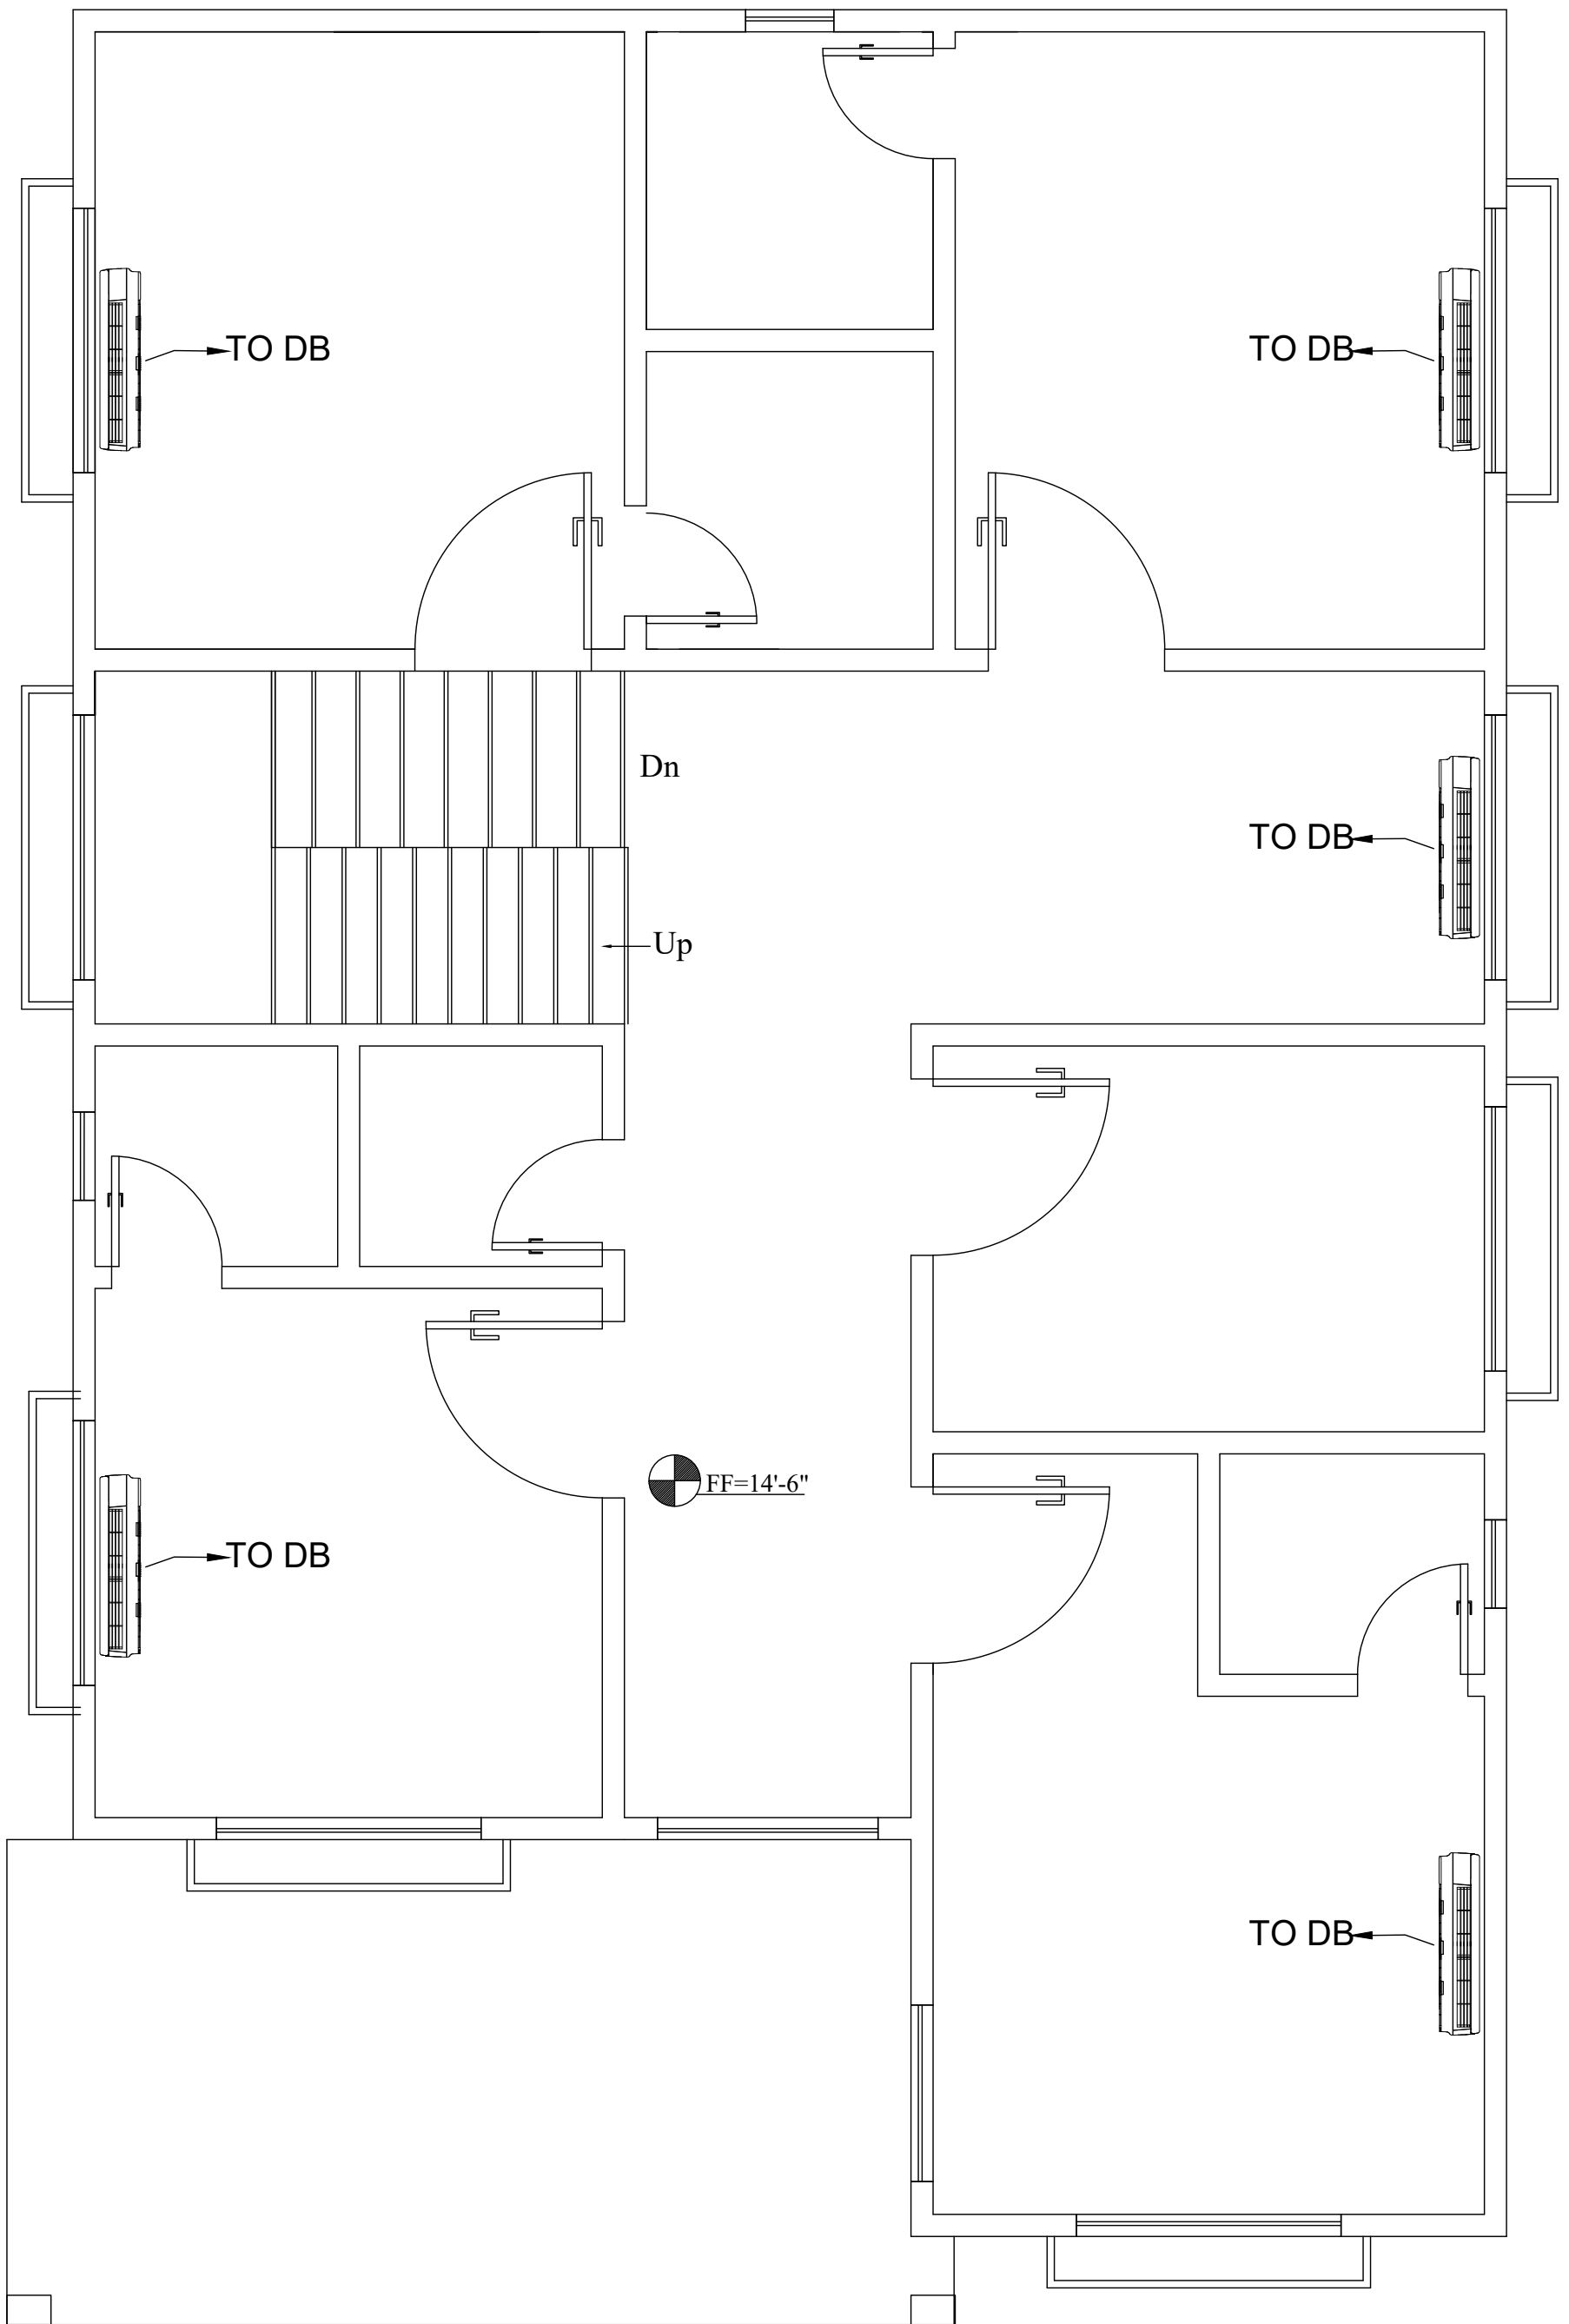

First Floor Covered Area= 1697.75 square ft


Project: Residential	Drawing:	Drawing Code:	Design By Wajid Khan: 0342-2421701
		S.No:	

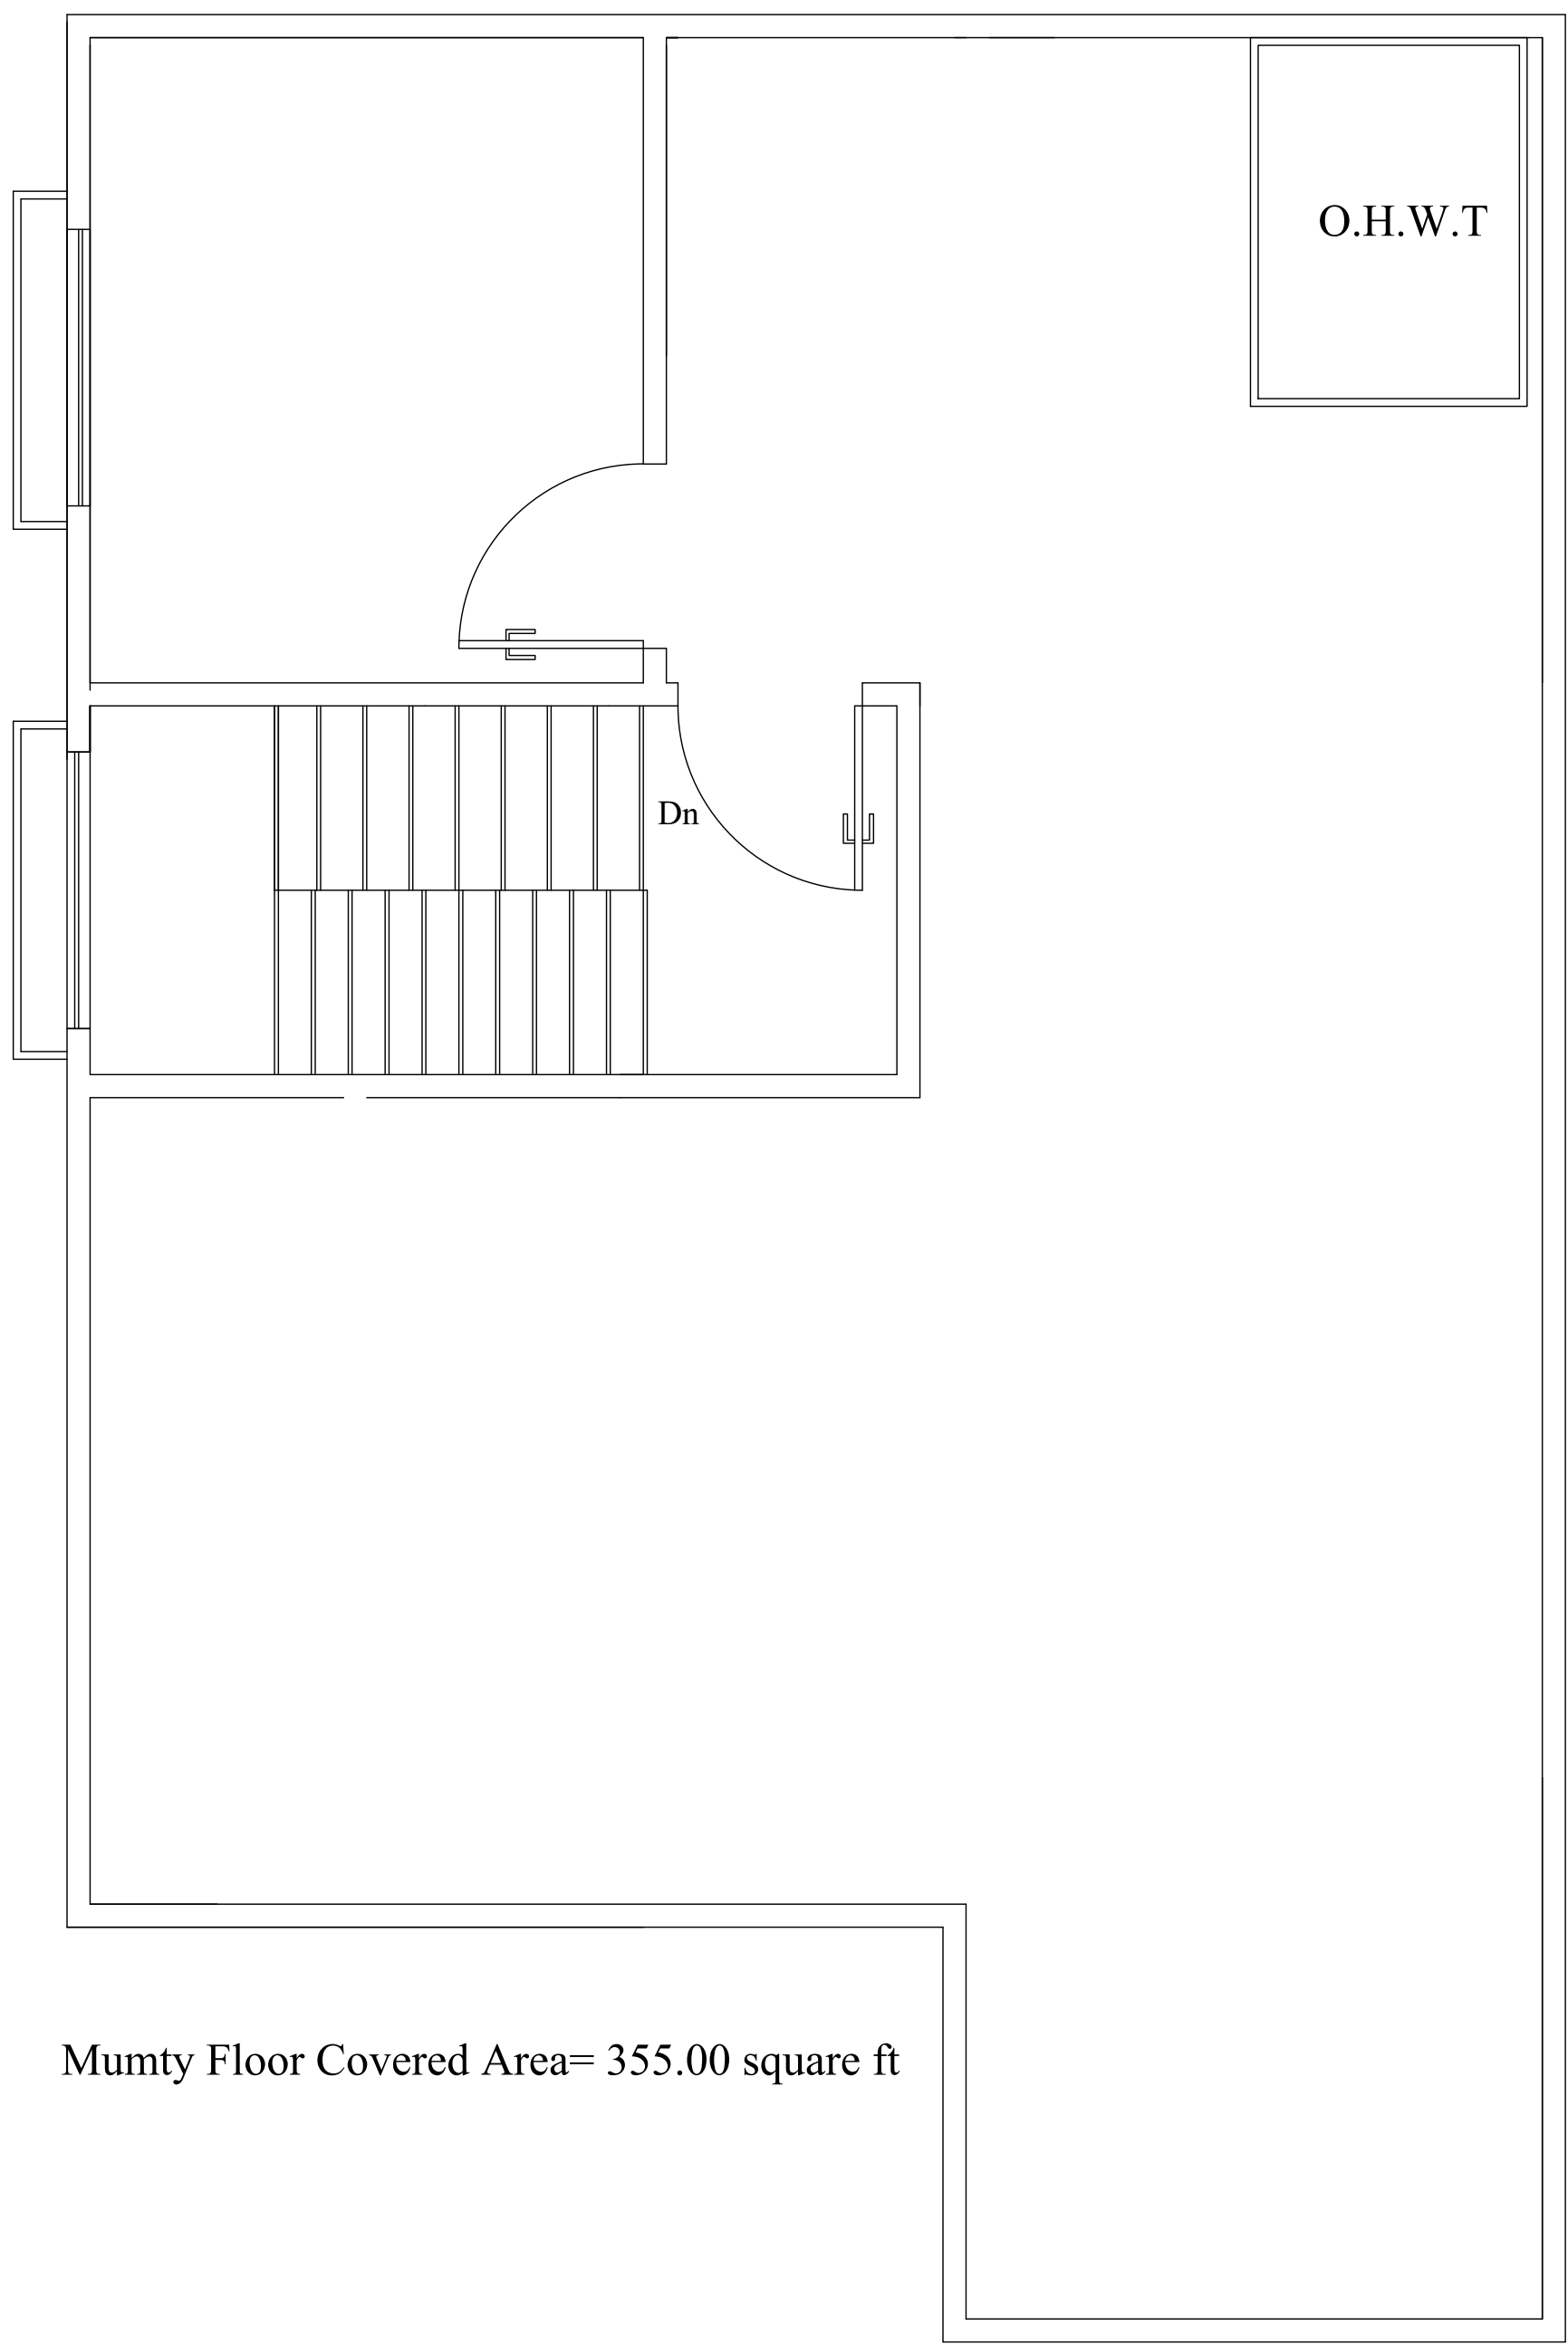

Mumty Floor Covered Area= 355.00 square ft

Project: Residential	Drawing:	Drawing Code:	Design By Wajid Khan: 0342-2421701
		S.No:	

Public Health

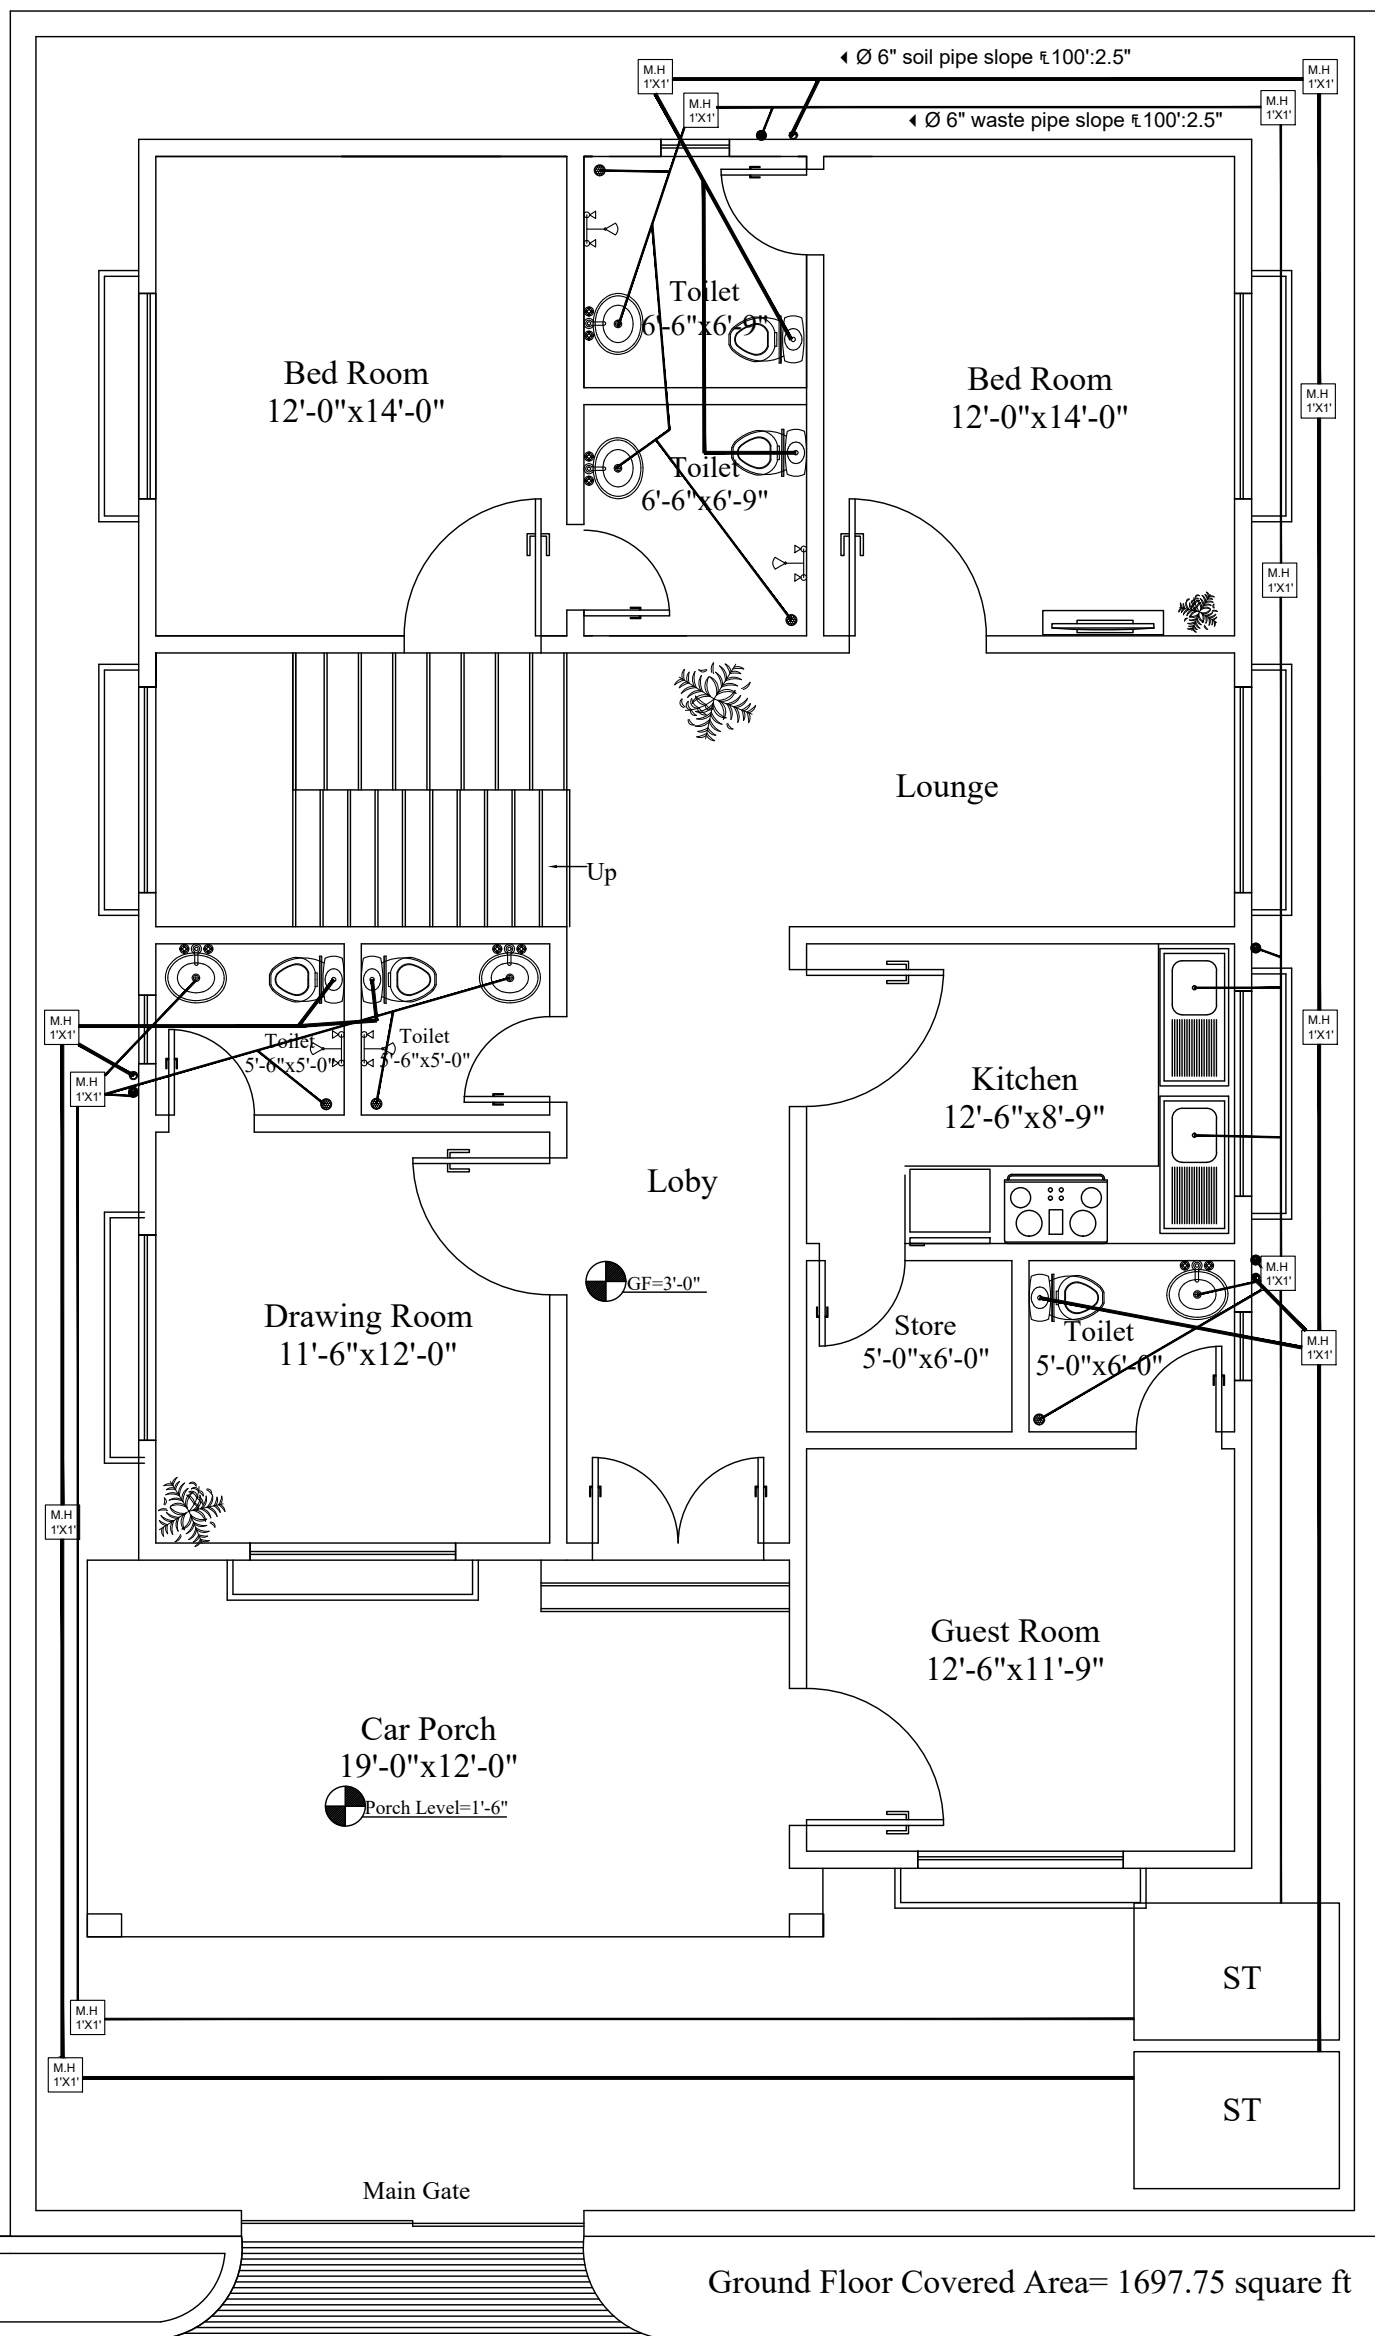

Road Level=0'-0"

Project:
Residential


Drawing:

Drawing Code:

S.No:


Design By

Wajid Khan: 0342-2421701

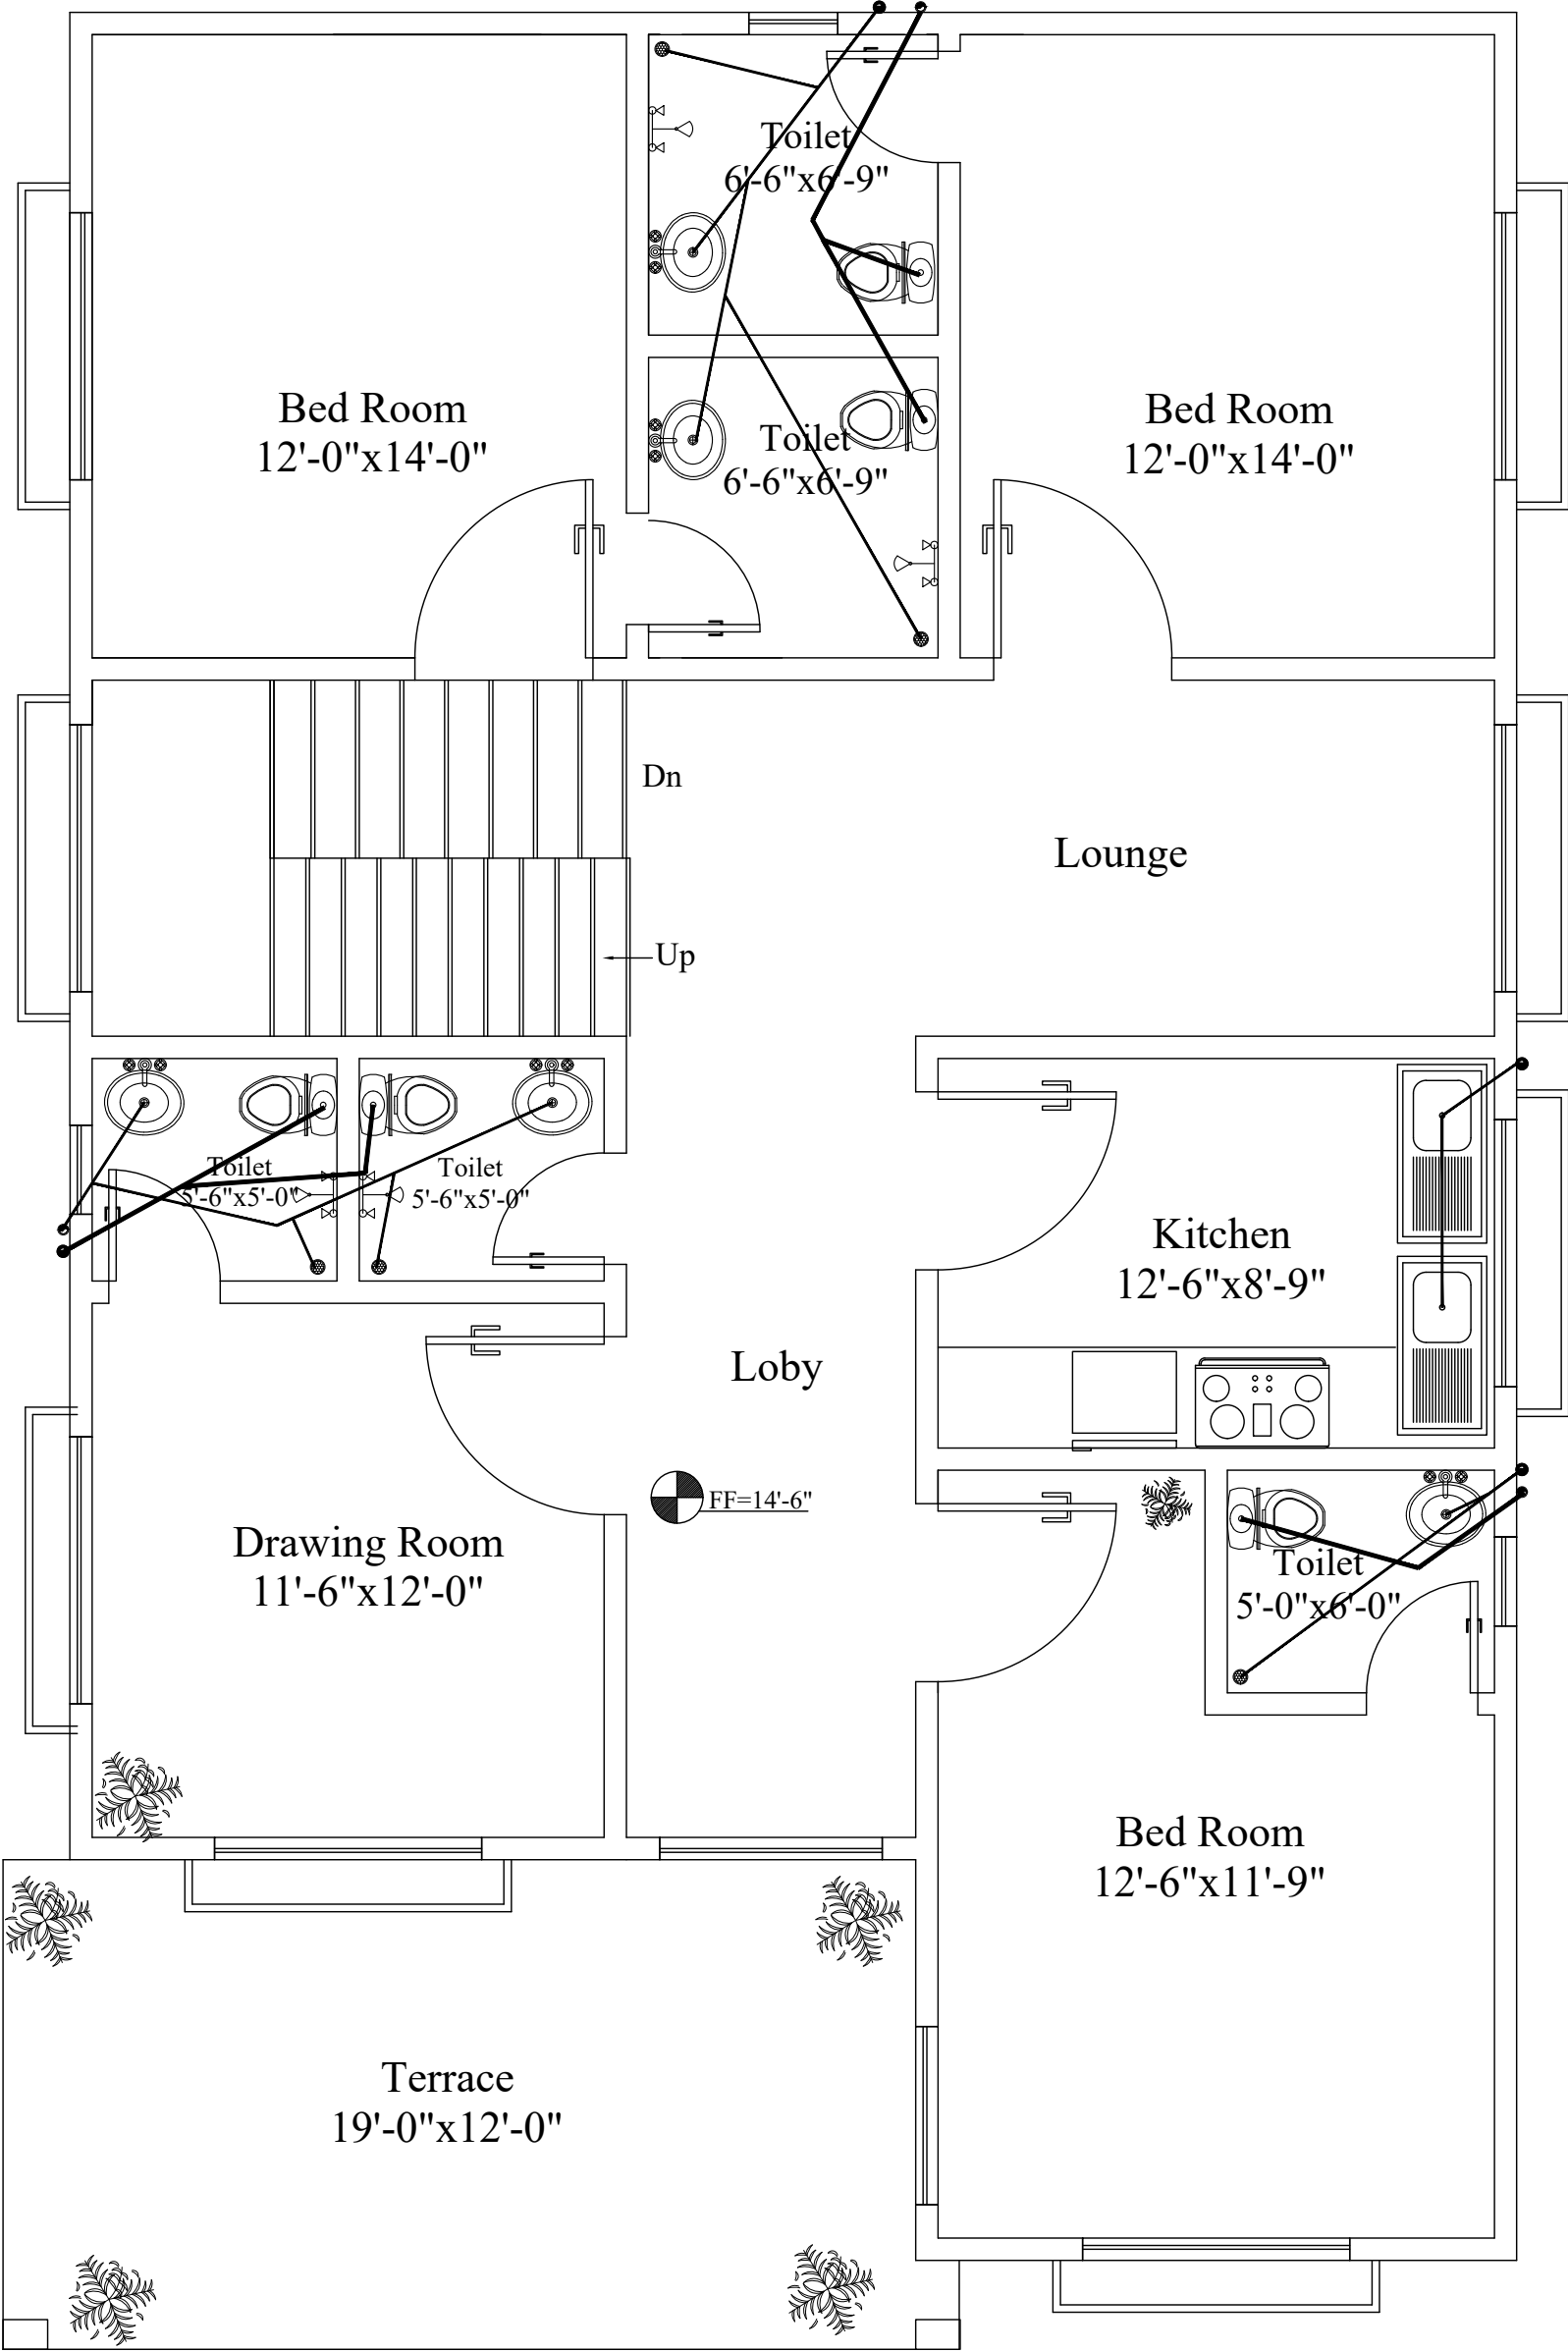

First Floor Covered Area= 1697.75 square ft

Project: Residential	Drawing:	Drawing Code:	Design By Wajid Khan: 0342-2421701
		S.No:	

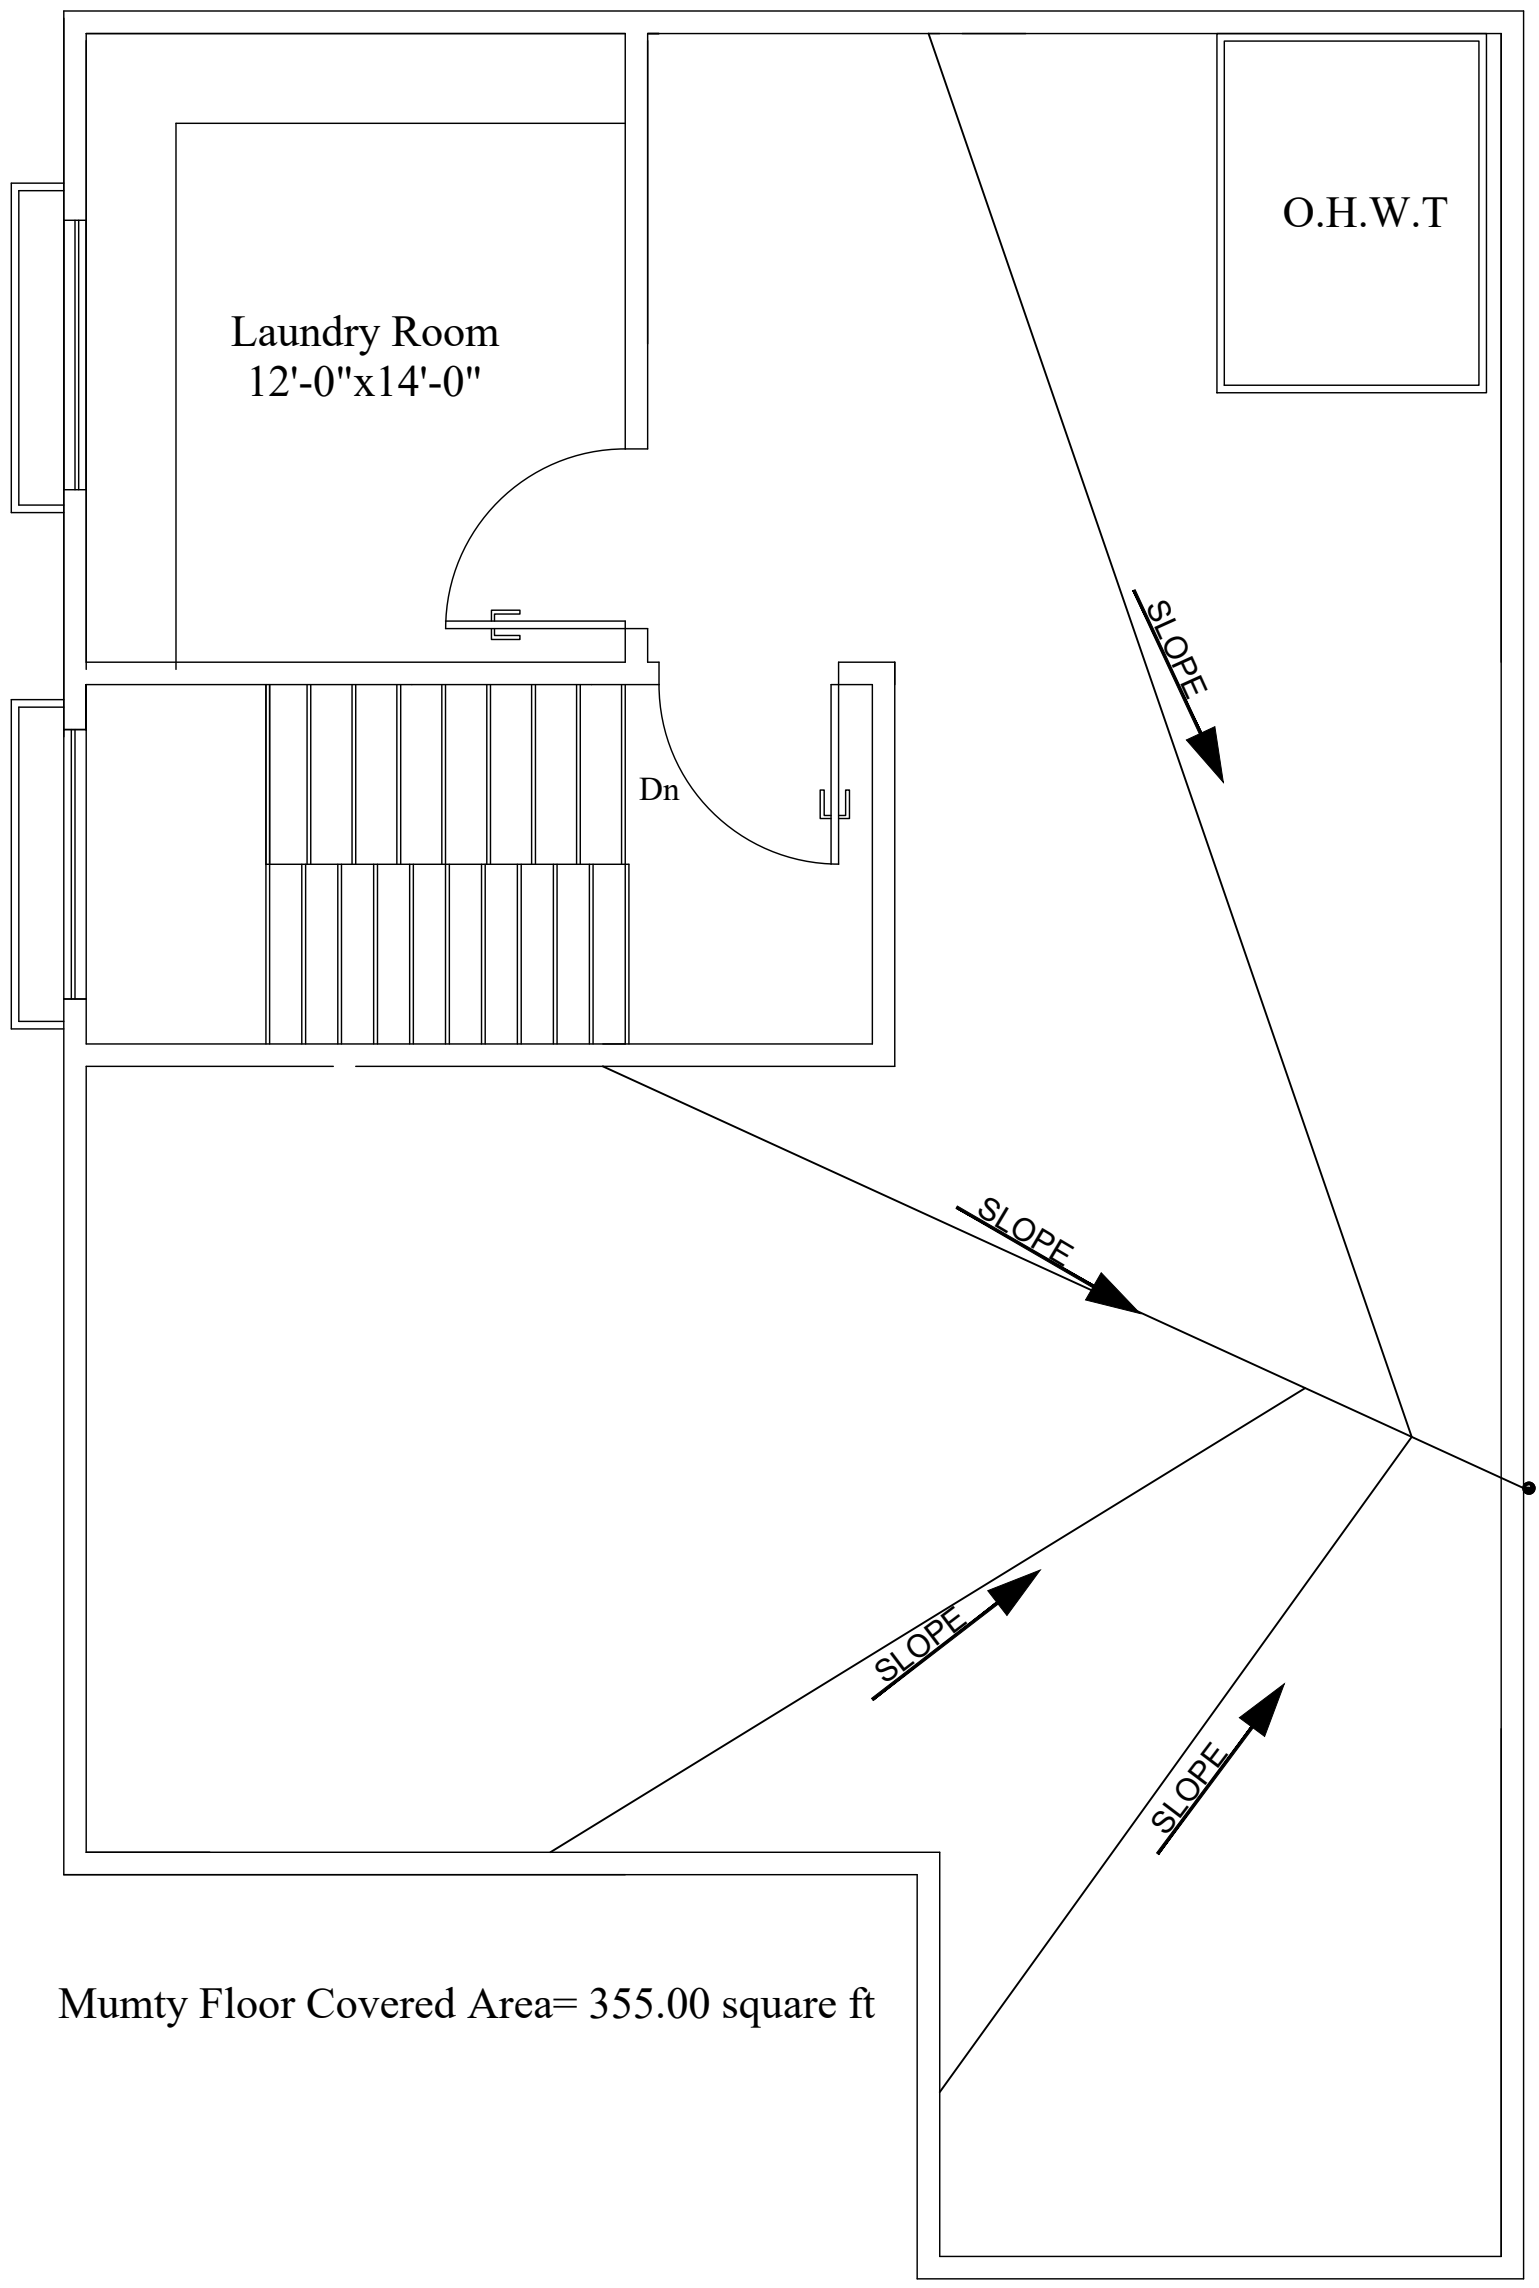

Project: Residential	Drawing:	Drawing Code:	Design By Wajid Khan: 0342-2421701
		S.No:	